




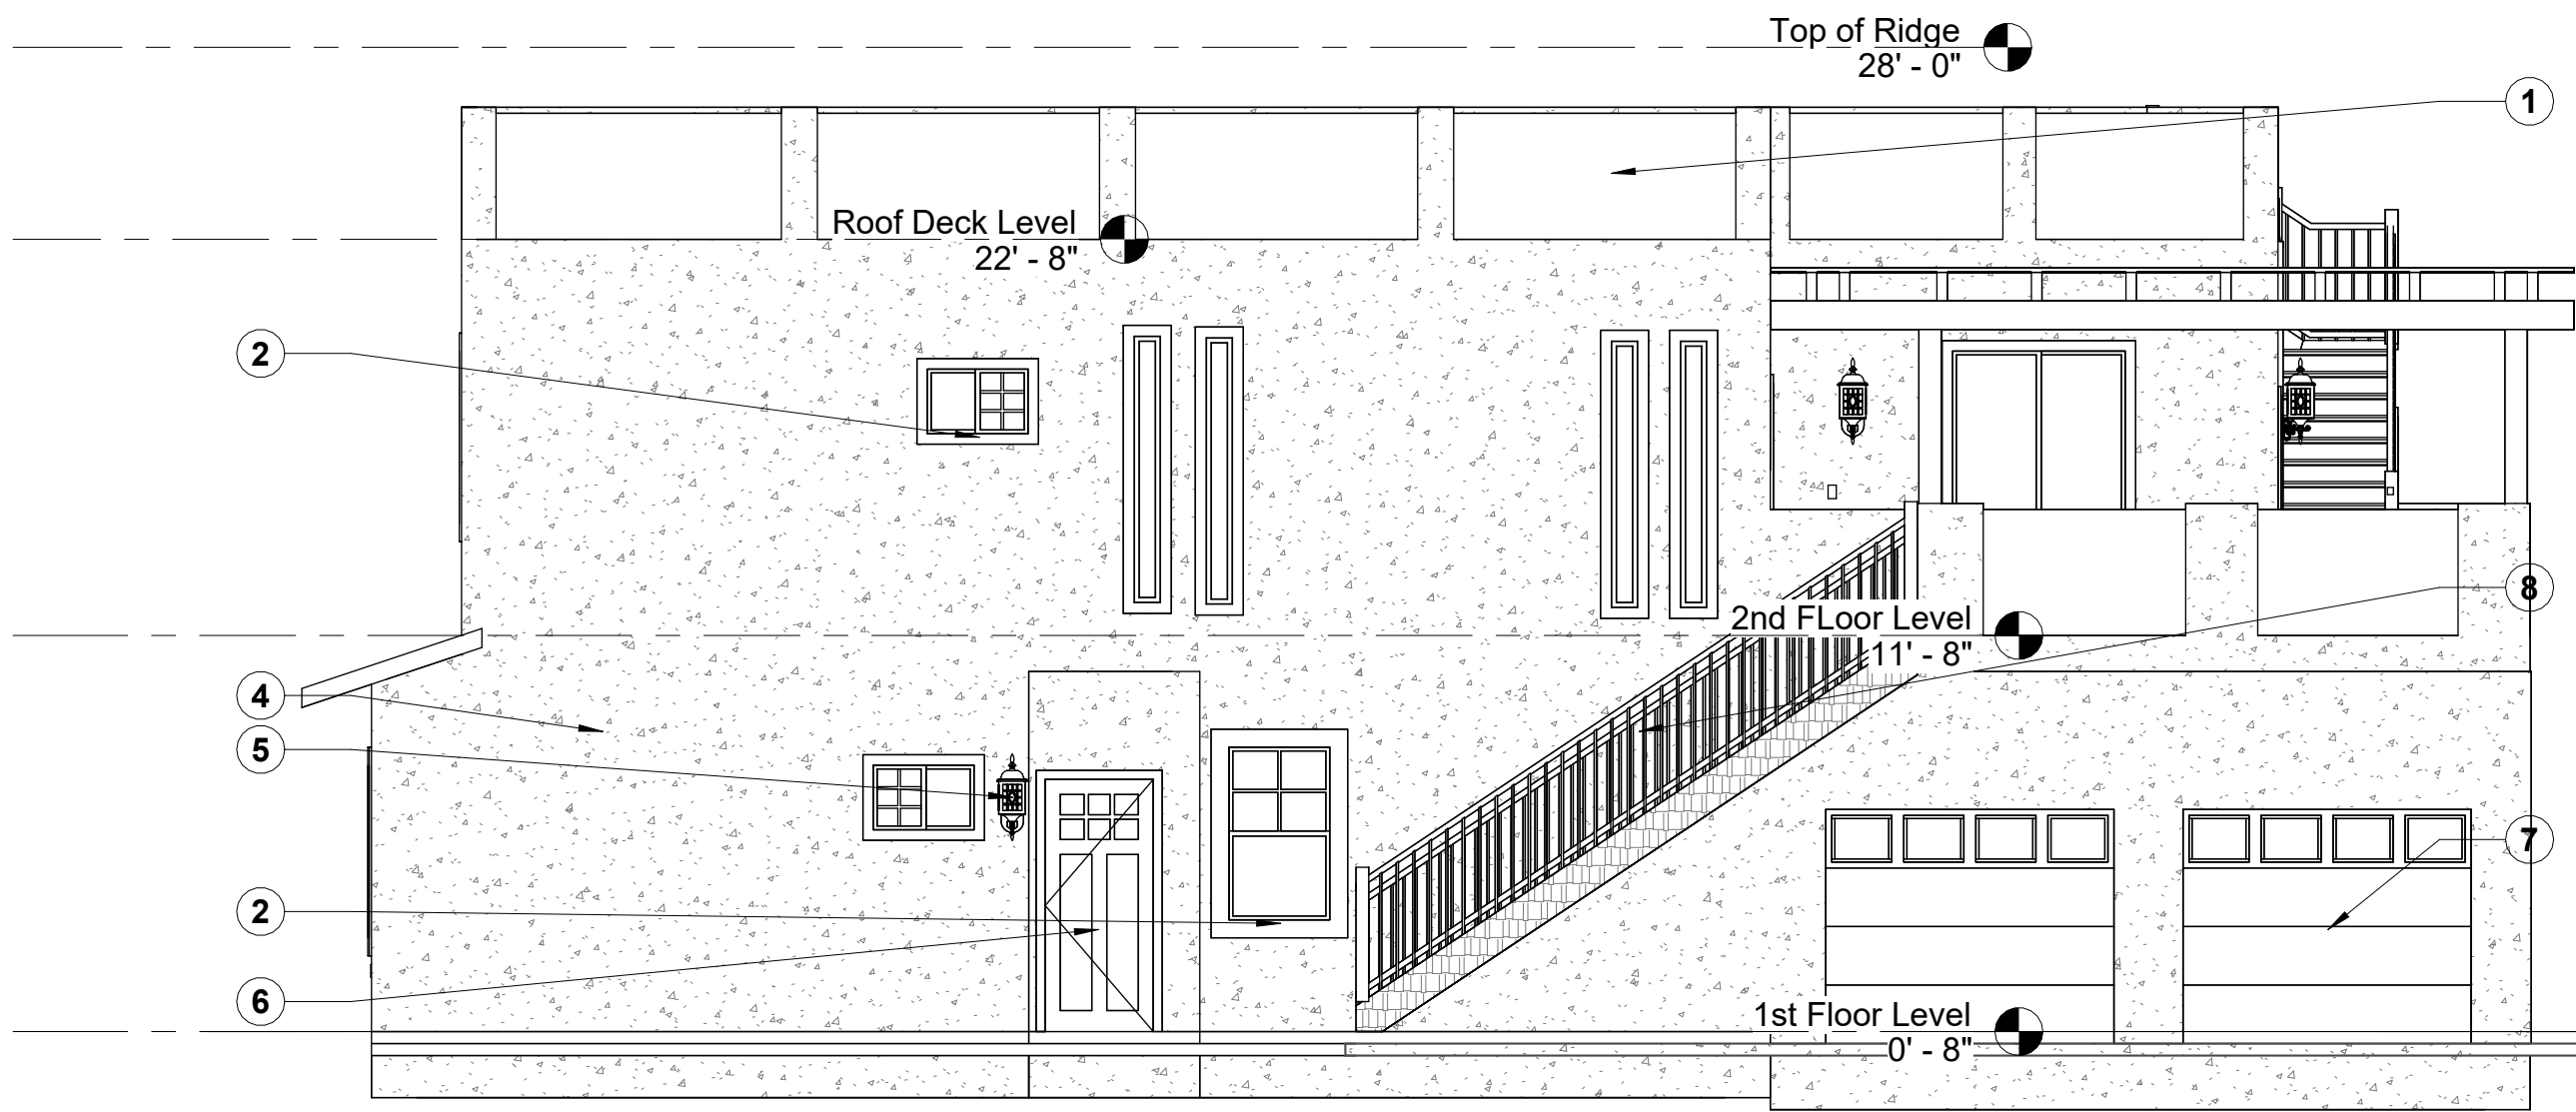


1 *South Elev.*
3/16" = 1'-0"

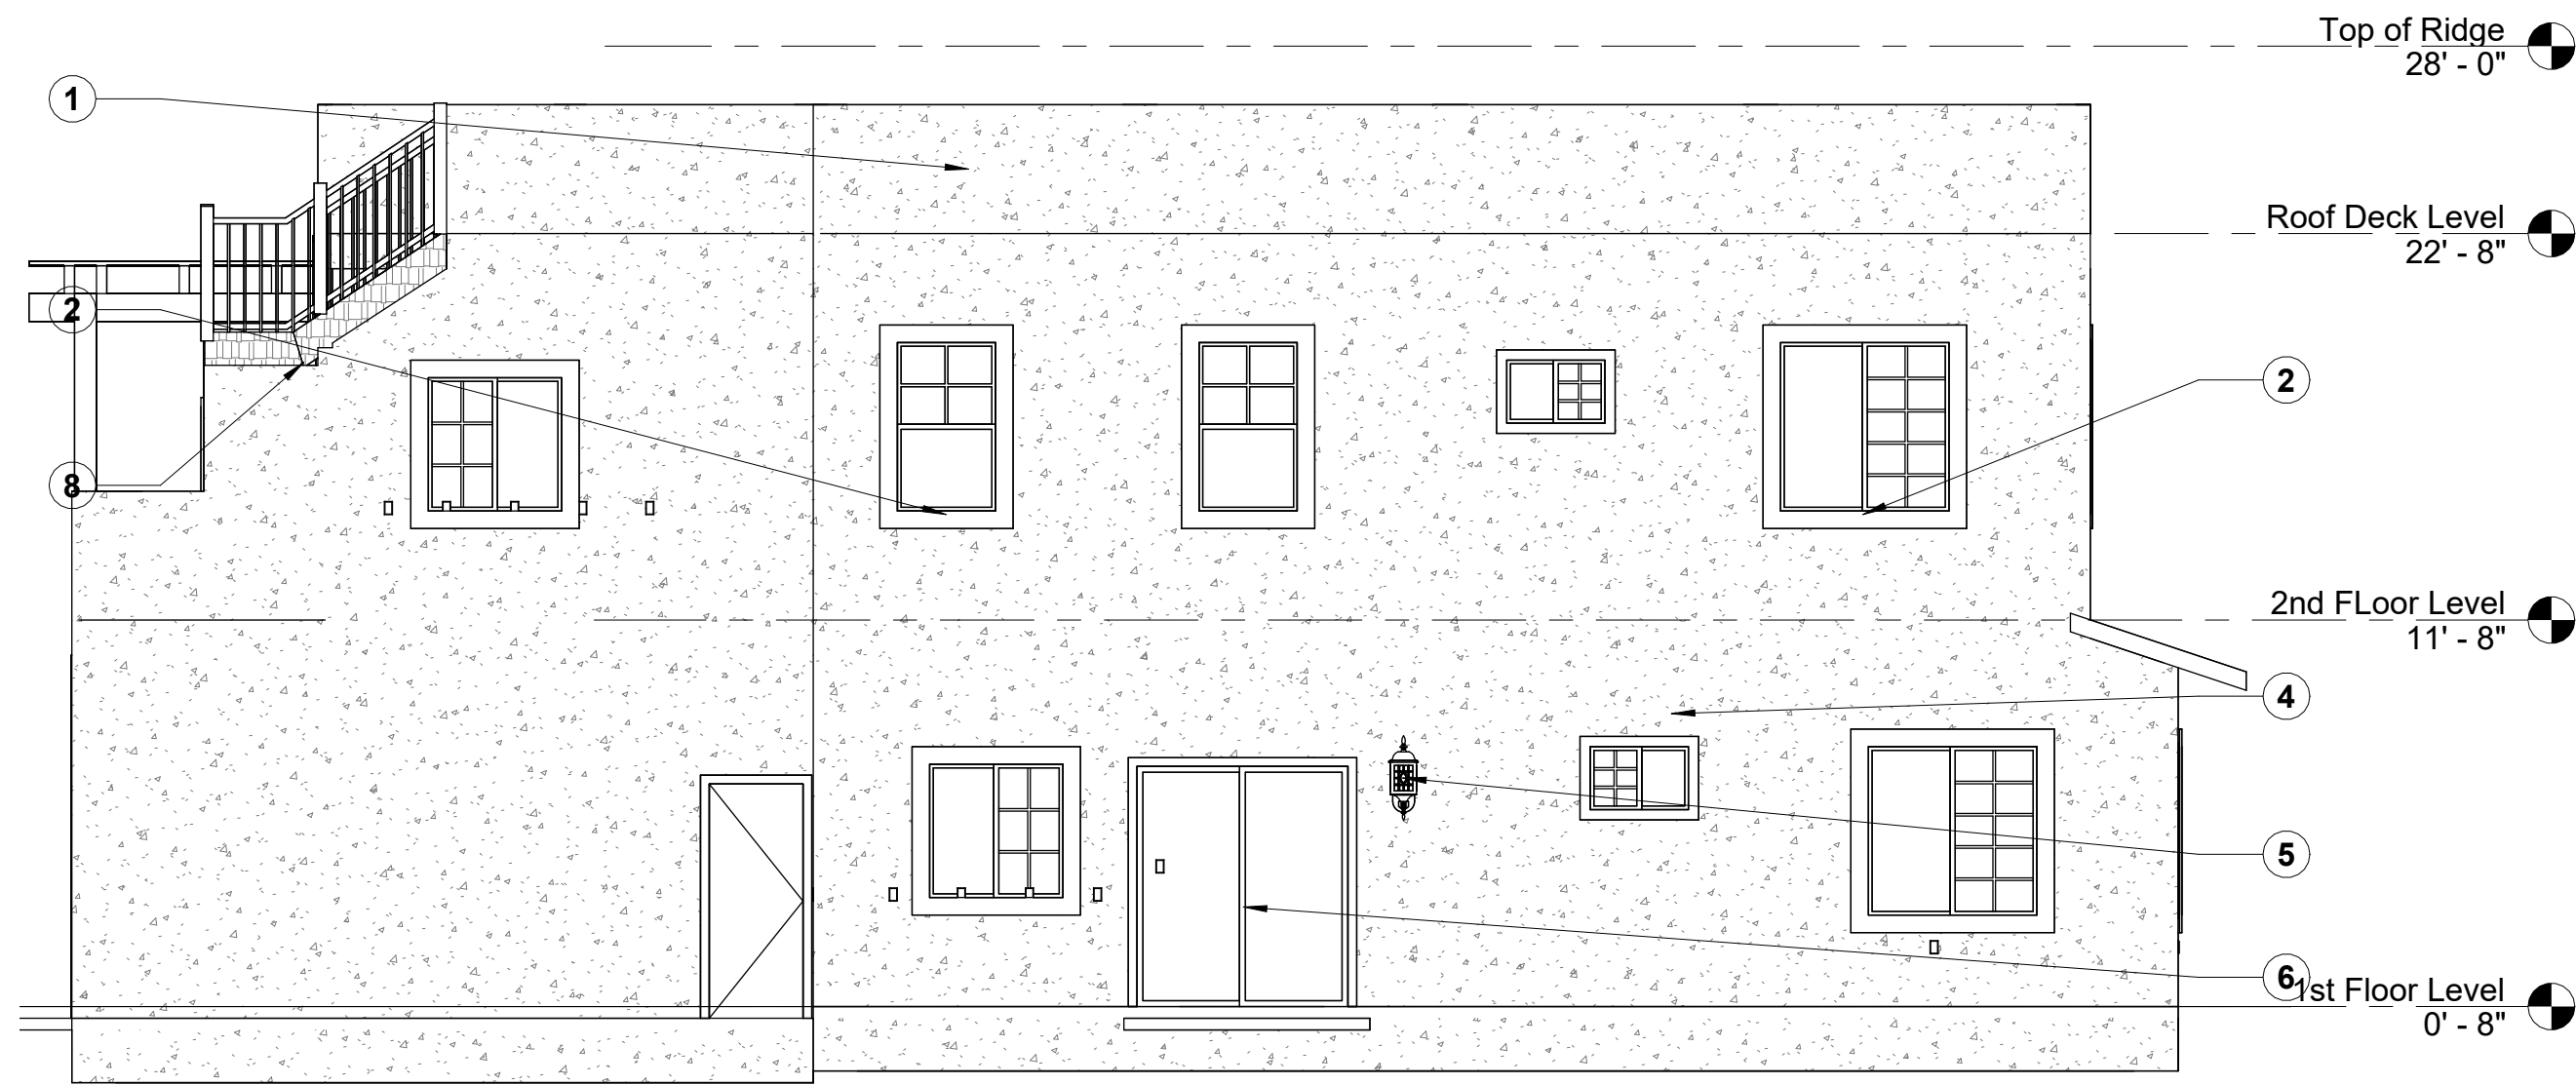

2 *North Elev.*
3/16" = 1'-0"

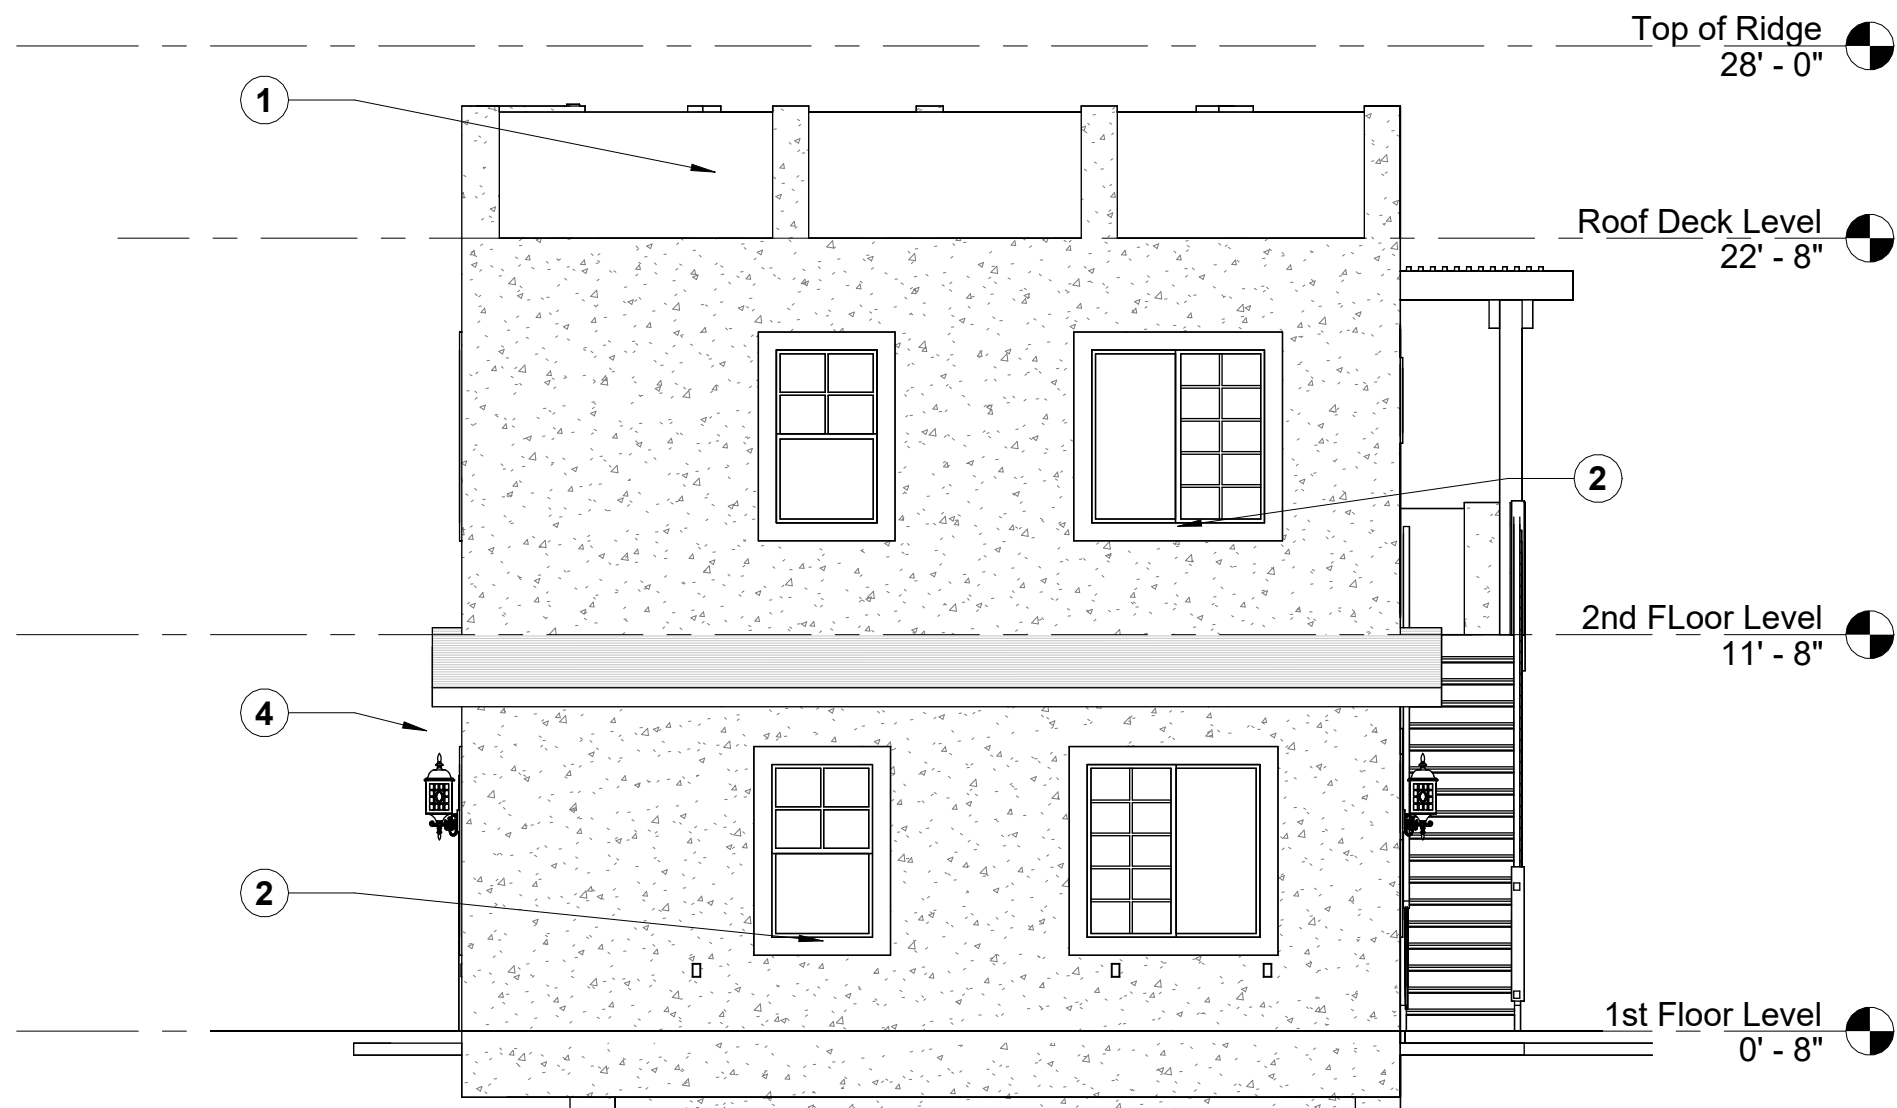

3 *West Elev.*
3/16" = 1'-0"

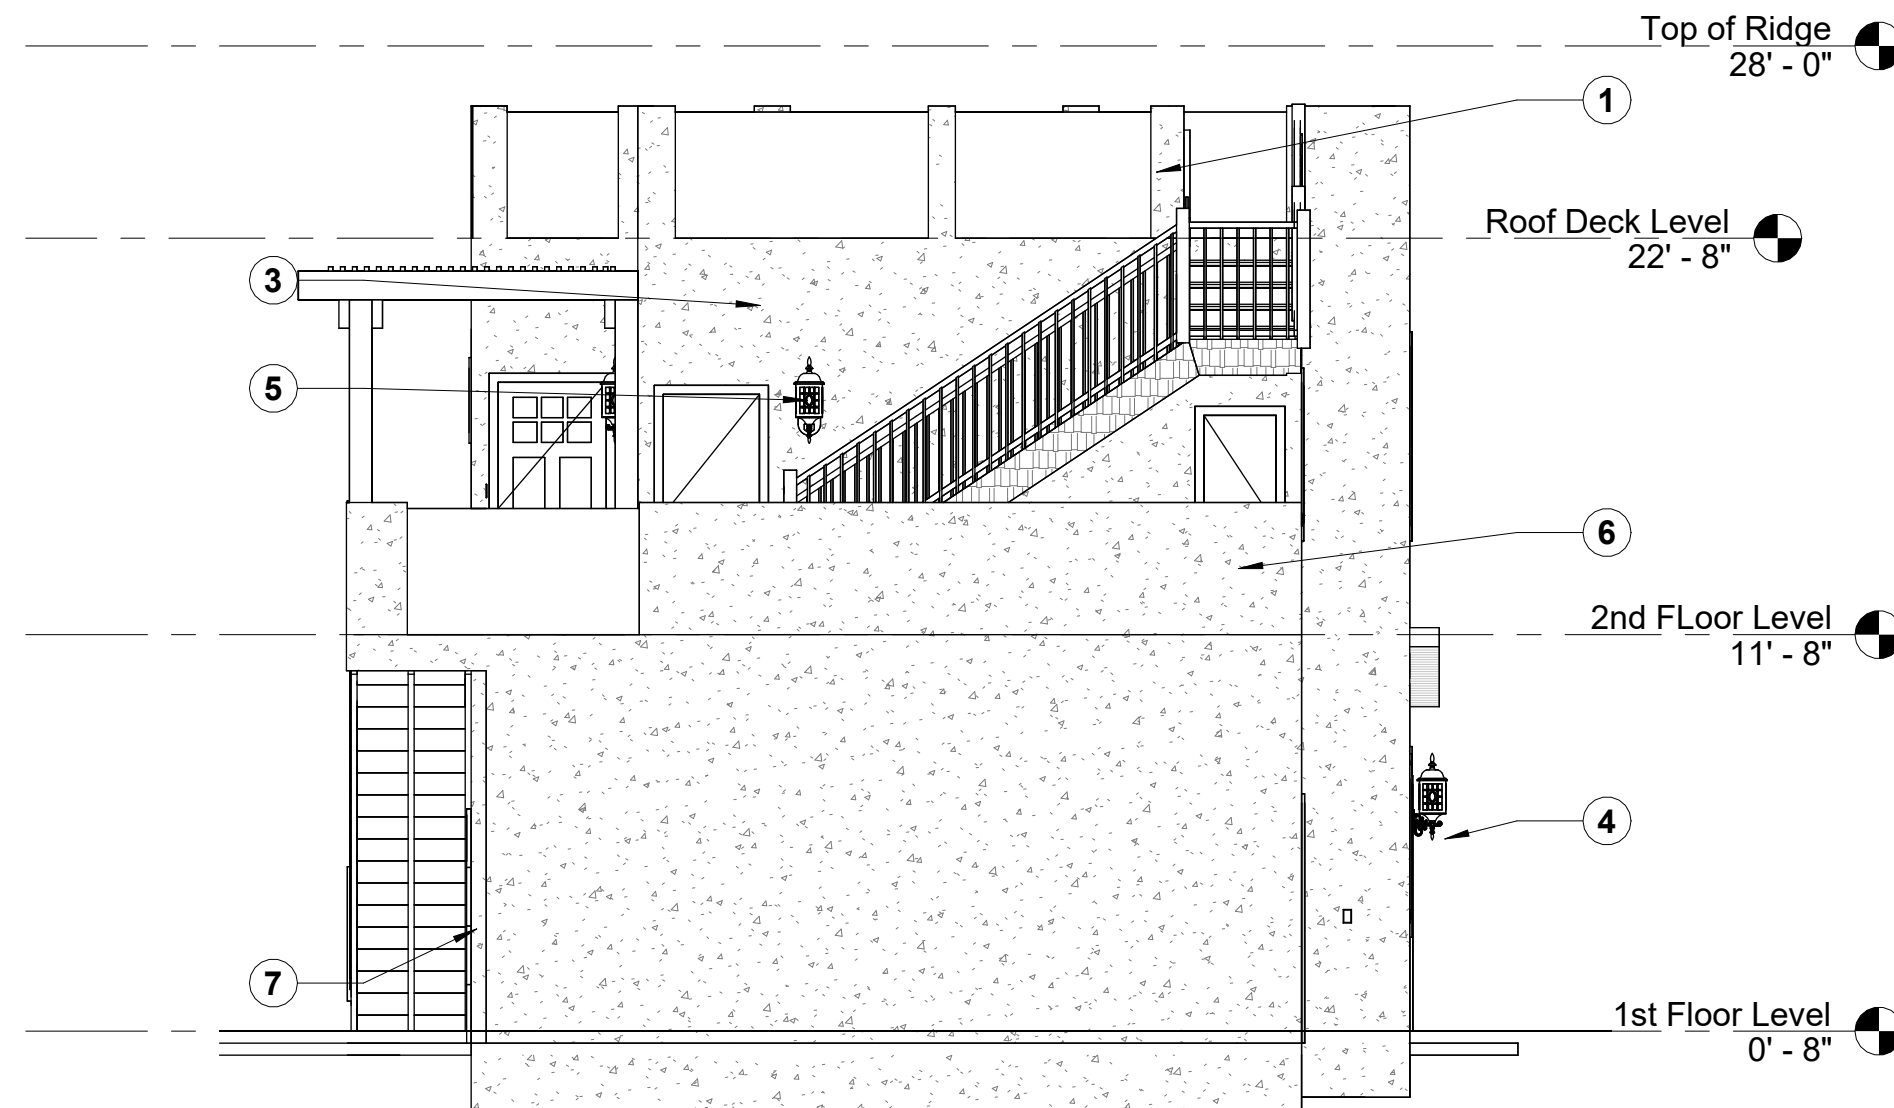

4 *East Elev.*
3/16" = 1'-0"

KEYNOTES:

- 42" HIGH GUARDRAIL @ ROOF DECK
- WINDOW PER SCHEDULE
- OPEN WOOD TRELLIS @ ROOF DECK
- STUCCO AT EXTERIOR WALL TO MATCH EXISTING
- EXTERIOR LIGHT
- EXTERIOR DOOR PER SCHEDULE
- SECTIONAL GARAGE DOOR
- EXTERIOR MTL STAIR W/ 42" GUARDRAIL