




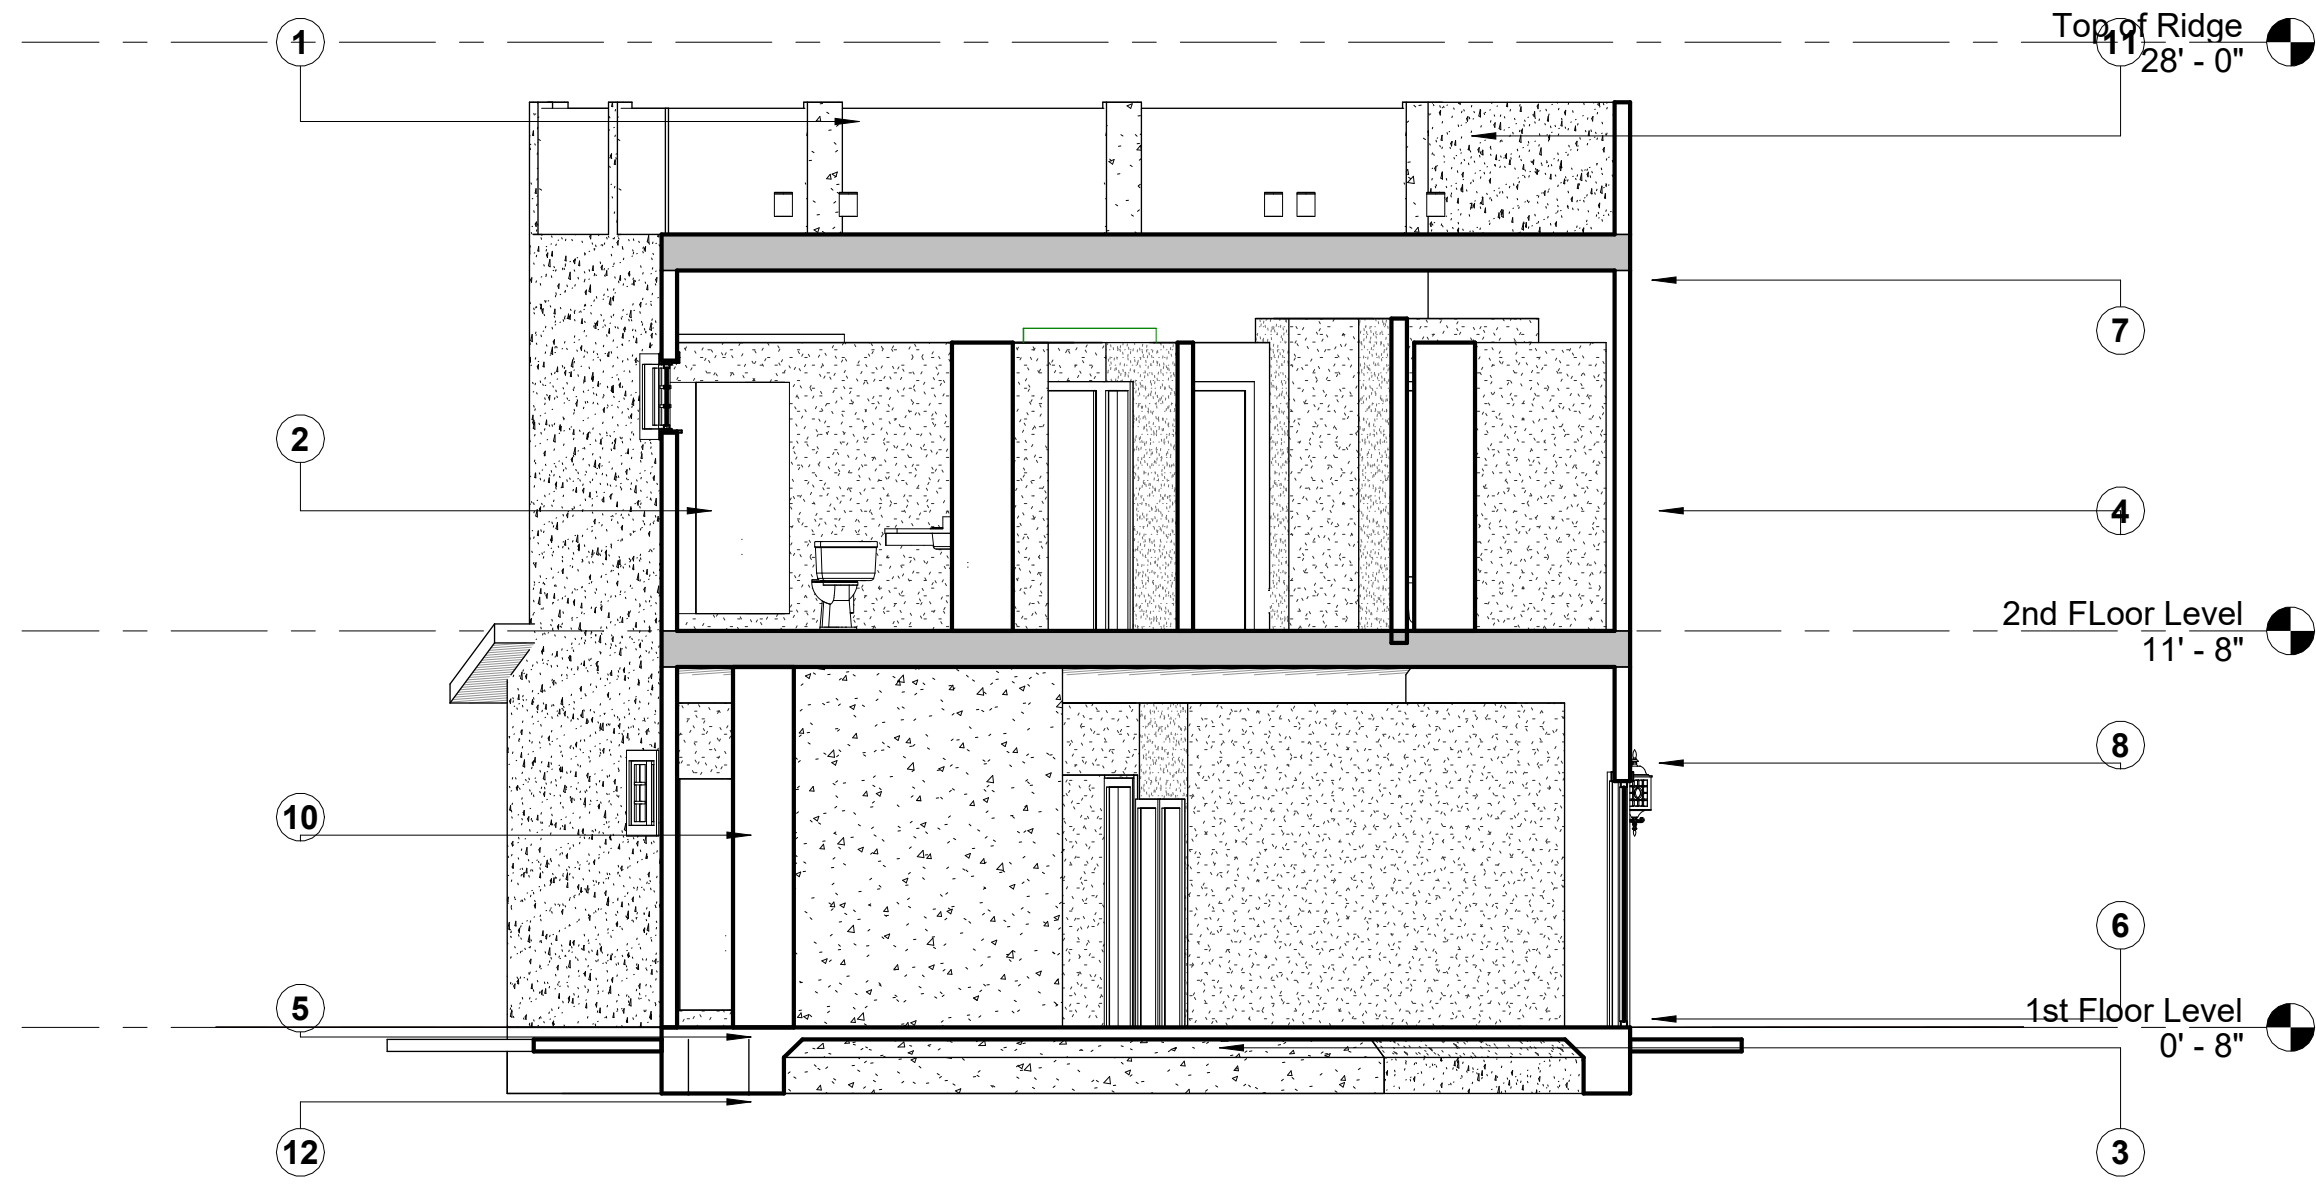

1 Section 1
3/16" = 1'-0"

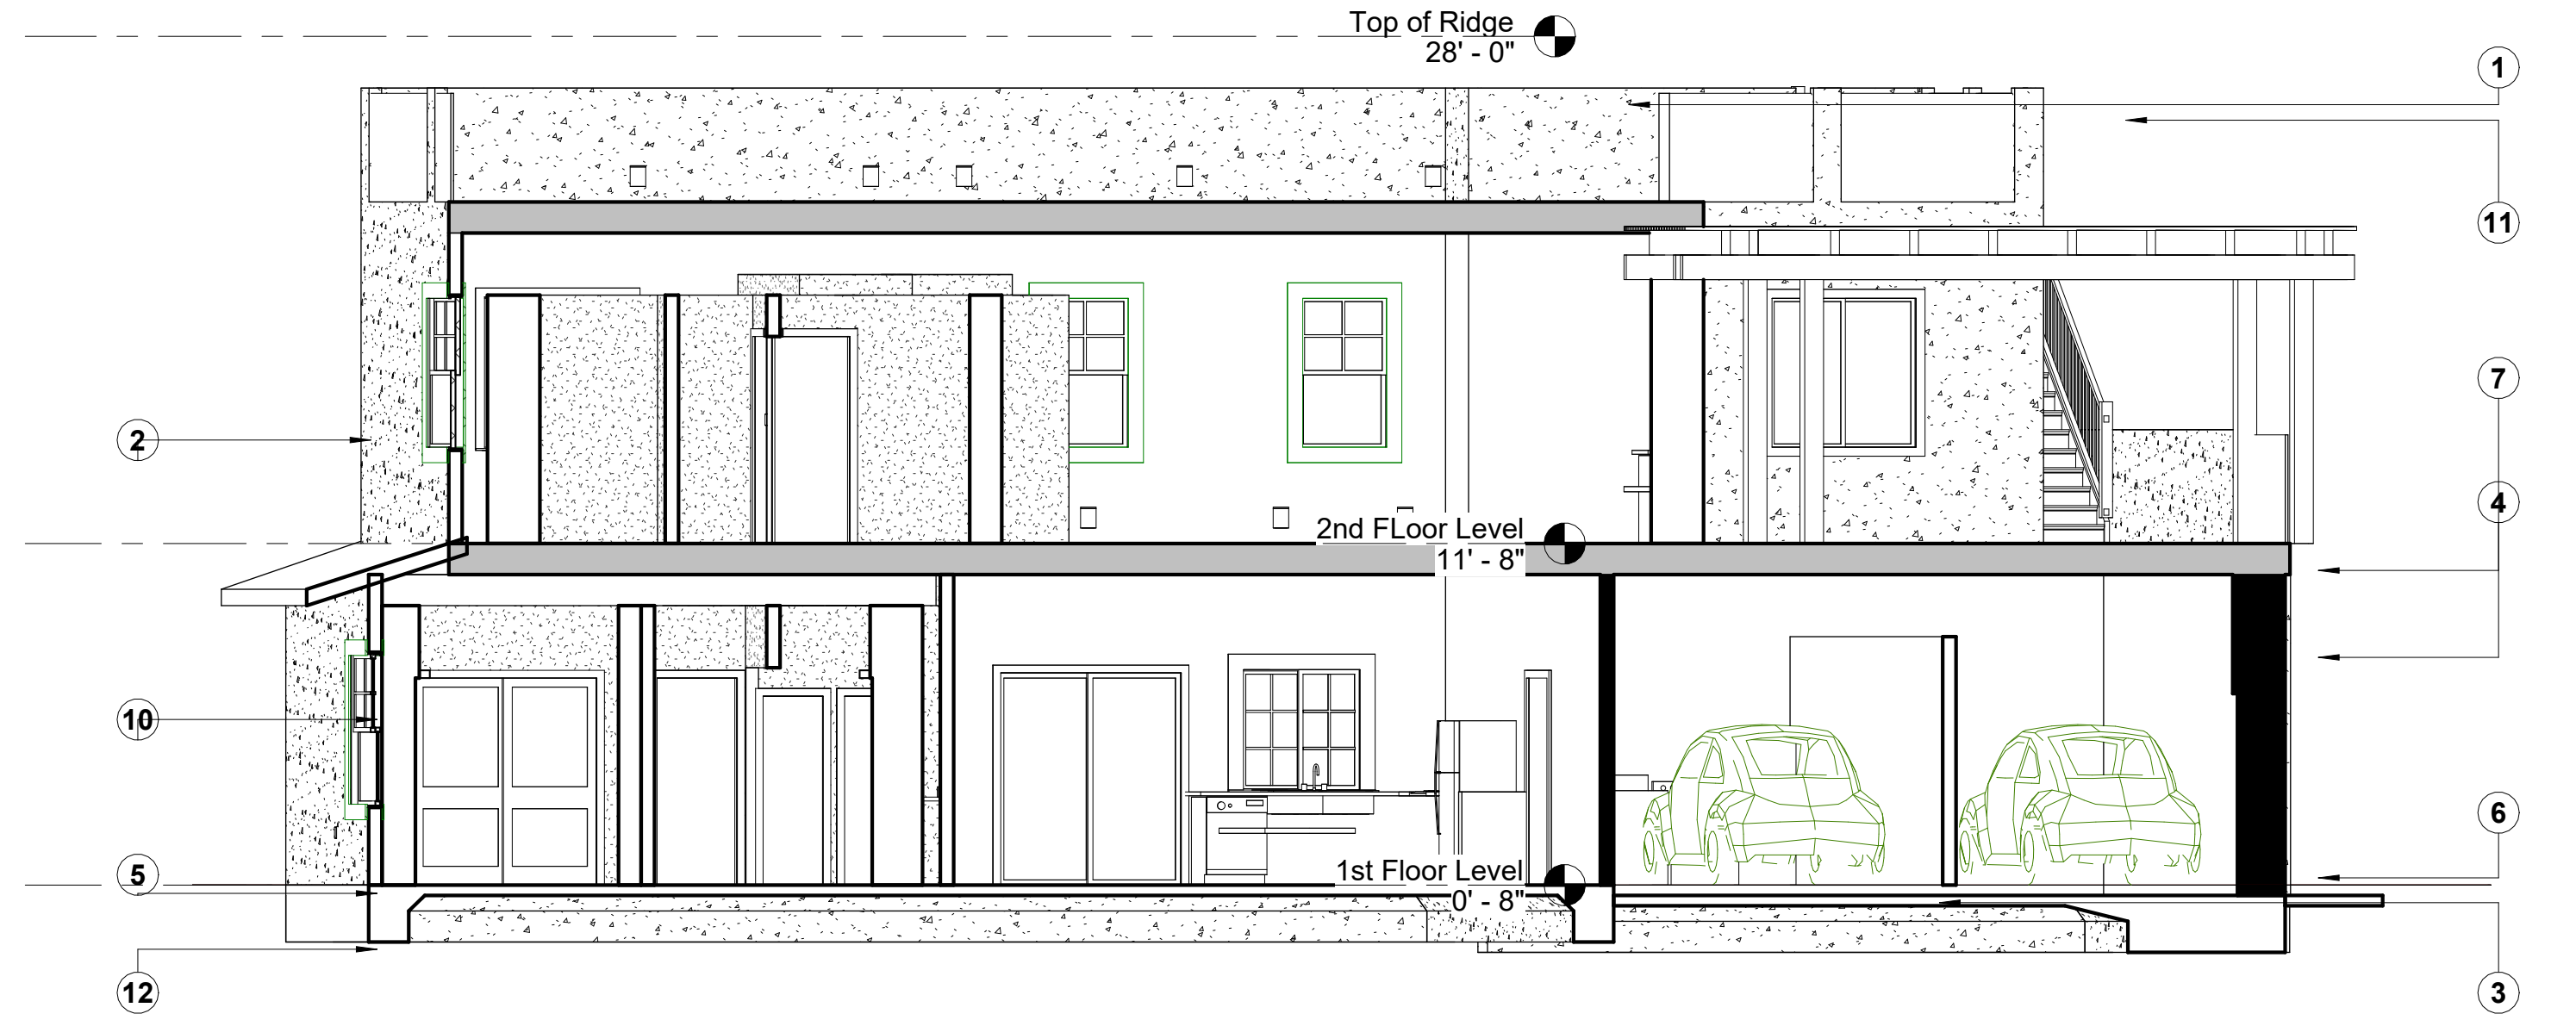

3 Section 3
3/16" = 1'-0"

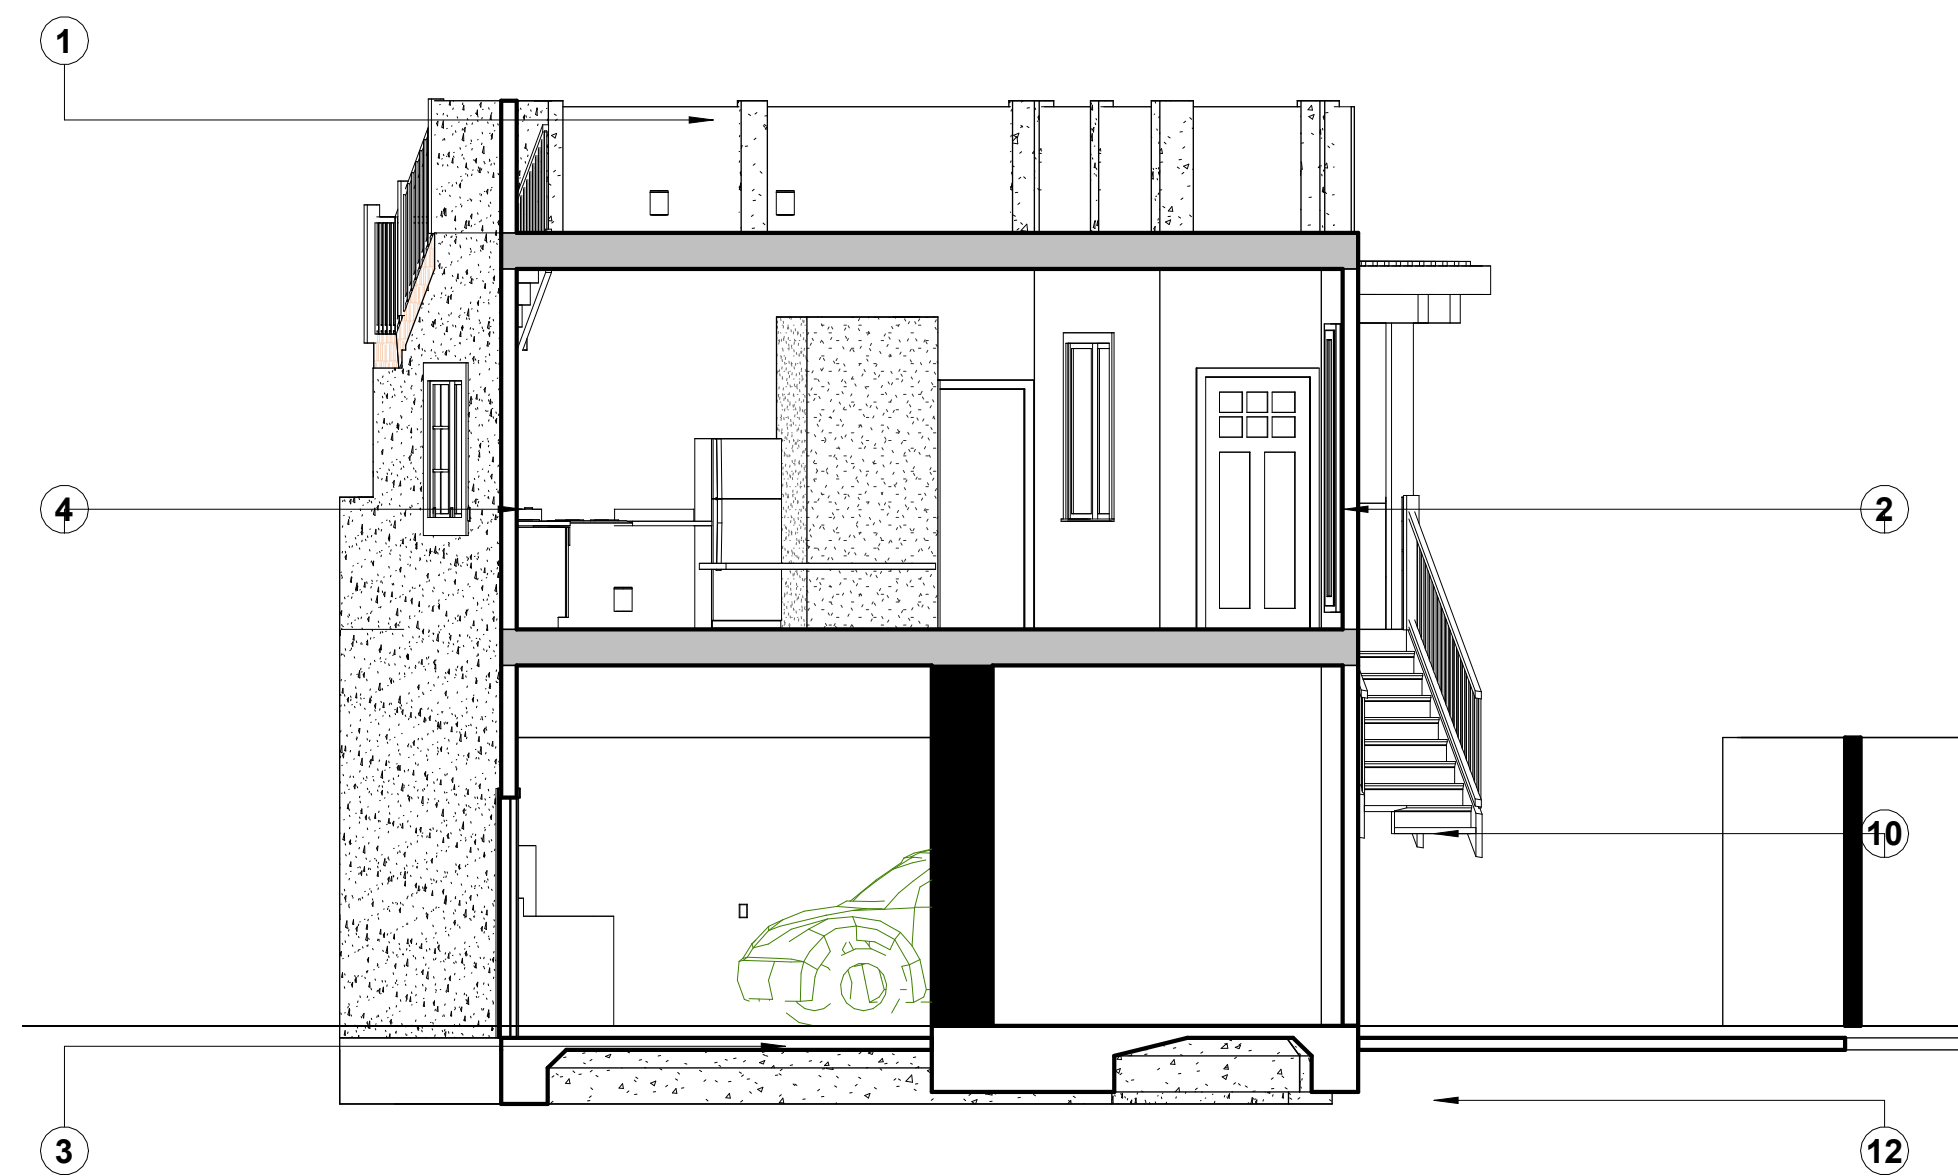

2 Section 2
3/16" = 1'-0"



4 Section 4
3/16" = 1'-0"

KEYNOTES

- | | |
|---------------------------------|------------------------------|
| 1 CLASS A ROOF DECK SYSTEM | 8 2x4 STUDS @ 16" O.C. |
| 2 STUCCO @ EXTERIOR | 9 ROOF/FLR JOISTS PER PLAN |
| 3 4" MIN. CONC. SLAB ON GRADE | 10 R-15 BATT INSULATION |
| 4 1/2" GYP. BD. | 11 R-30 BATT INSULATION |
| 5 WEEP SCREED | 12 FOOTING PER DETAIL ON SD1 |
| 6 PRESSURE TREATED BOTTOM PLATE | 13 |
| 7 DOUBLE TOP PLATE | 14 |