


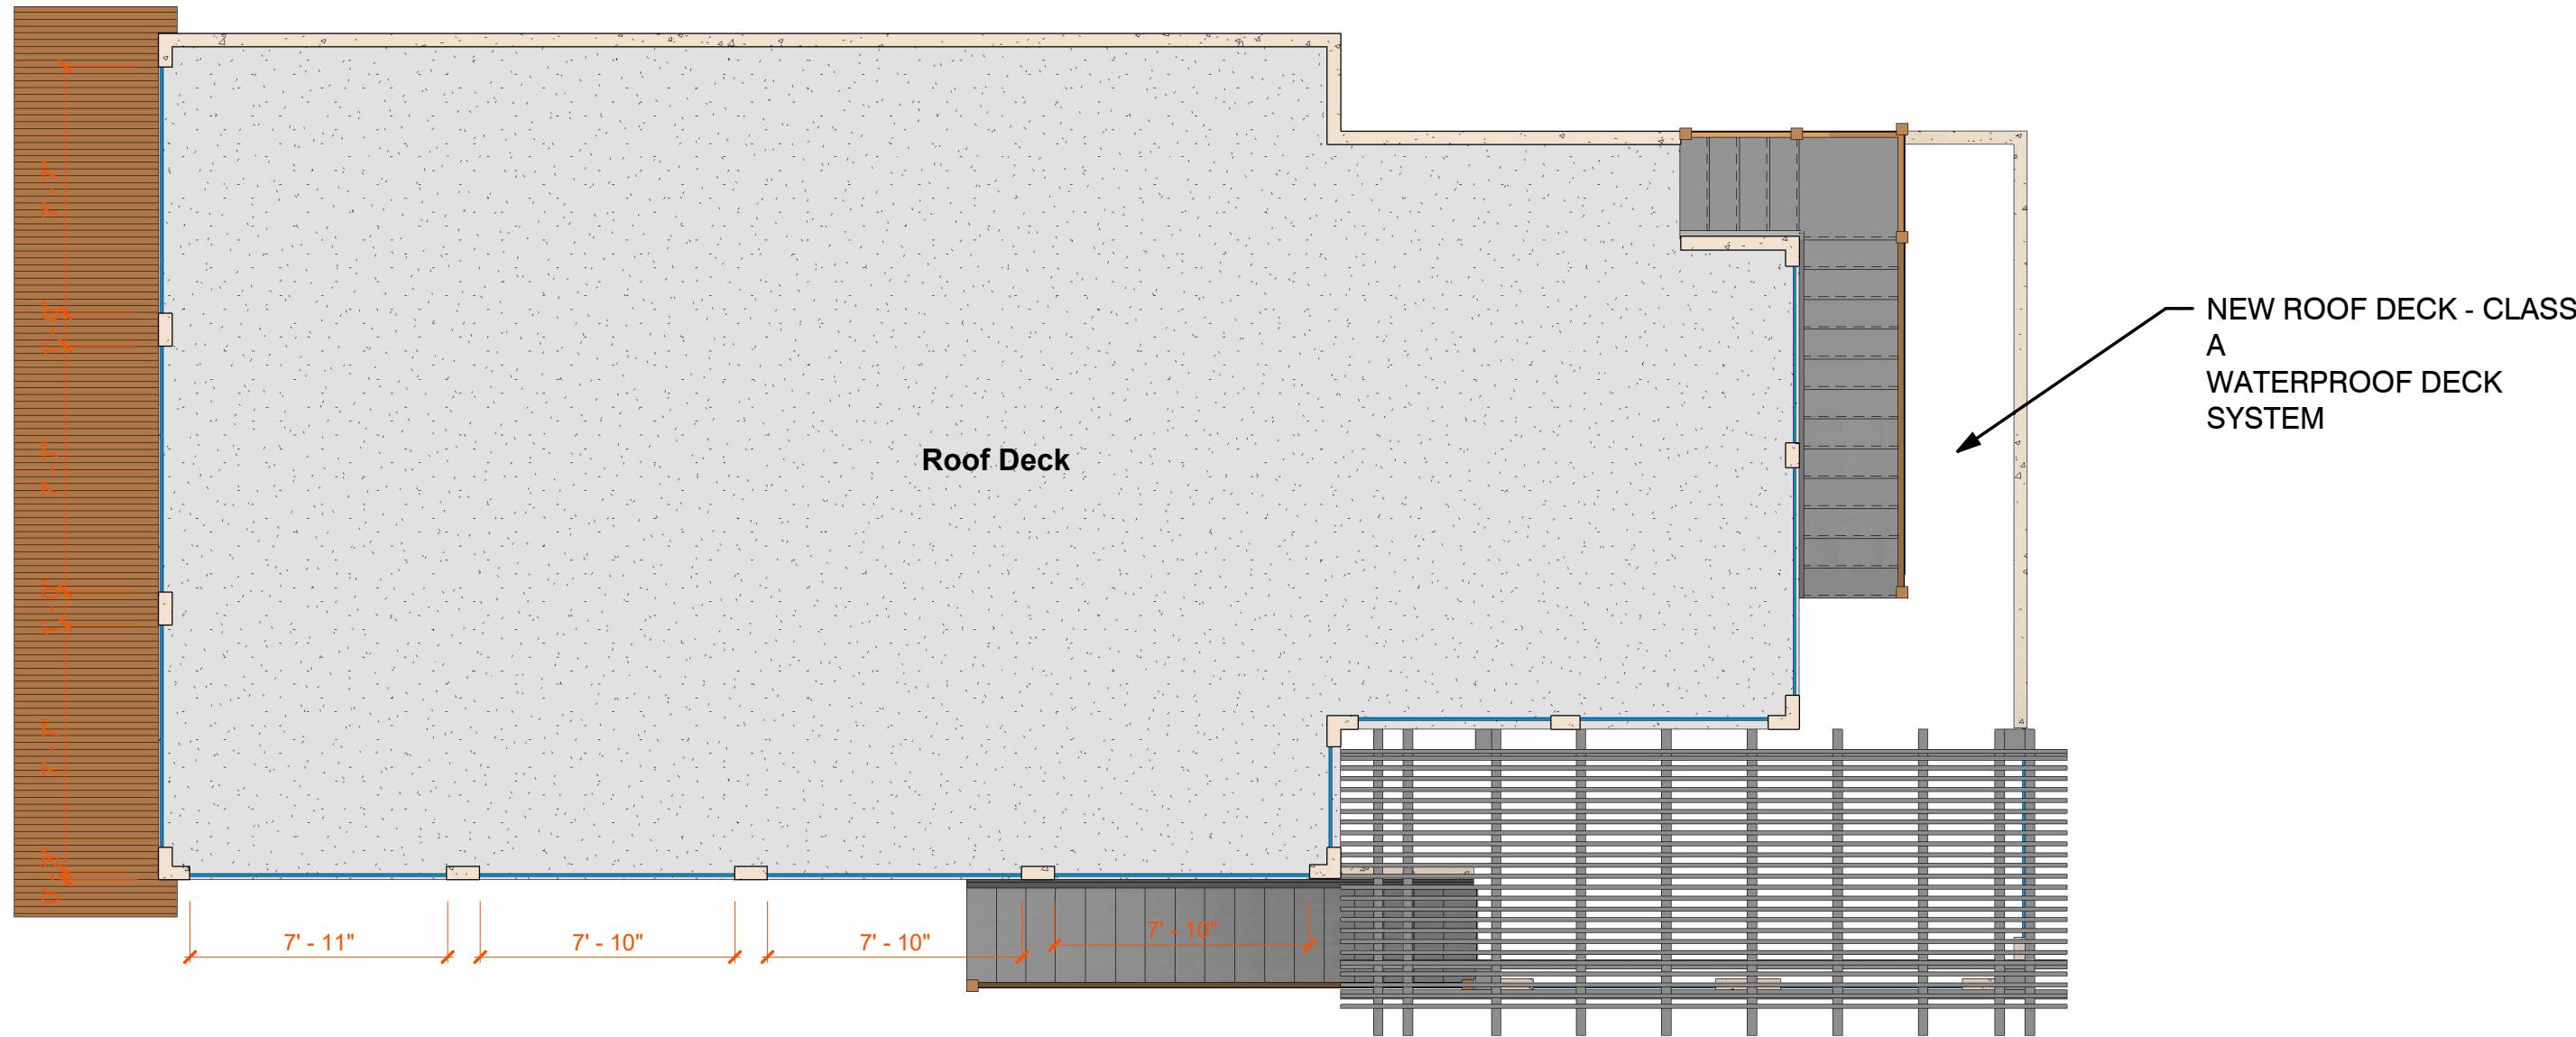

1 *Roof Plan*
3/16" = 1'-0"

NOTES: ROOF DECK SHALL BE SLOPED
MIN. 1/4" PER FOOT
TO ROOF DRAINS. PROVIDE EMERGENCY
OVERFLOW
DRAINS / SCUPPERS PER CRC R903.4.1.

ROOF MATERIALS INFO:
ROOF DECK: CLASS A FIRE-RATED WALKABLE WATERPROOF
DECK SYSTEM (ICC-ES LISTED), INSTALLED PER
MANUFACTURER SPECIFICATION.
SLOPE 1/4" PER FOOT MIN. TO ROOF DRAINS.
PROVIDE OVERFLOW DRAINS / SCUPPERS PER CRC R903.4.1

GUARDRAIL: 42" HIGH MIN. AT ROOF DECK PERIMETER.
OPENINGS SHALL REJECT A 4" SPHERE PER CRC R312.

OPEN WOOD TRELLIS: PER PLAN. PRESSURE TREATED OR
NATURALLY DURABLE WOOD.



Revision Dates		
1		08.15.24
2		01.01.25

SHEET TITLE
Roof Plan

Drawing Date 08.27.26
Check By
Drawn By FRANCIS N.
Scale As indicated
Job Number 022225
Sheet Number