


Steven Truong Res-New ADU
6633 Electric Ave
La Jolla, CA 92037




Revision Dates	
1	08.15.24
2	01.01.25
SHEET TITLE	
Foundation / Framing Plan	
Drawing Date	
08.27.26	
Check By	
-	
Drawn By	
FRANCIS N.	
Scale	
1/4" = 1'-0"	
Job Number	
022225	
Sheet Number	


S101

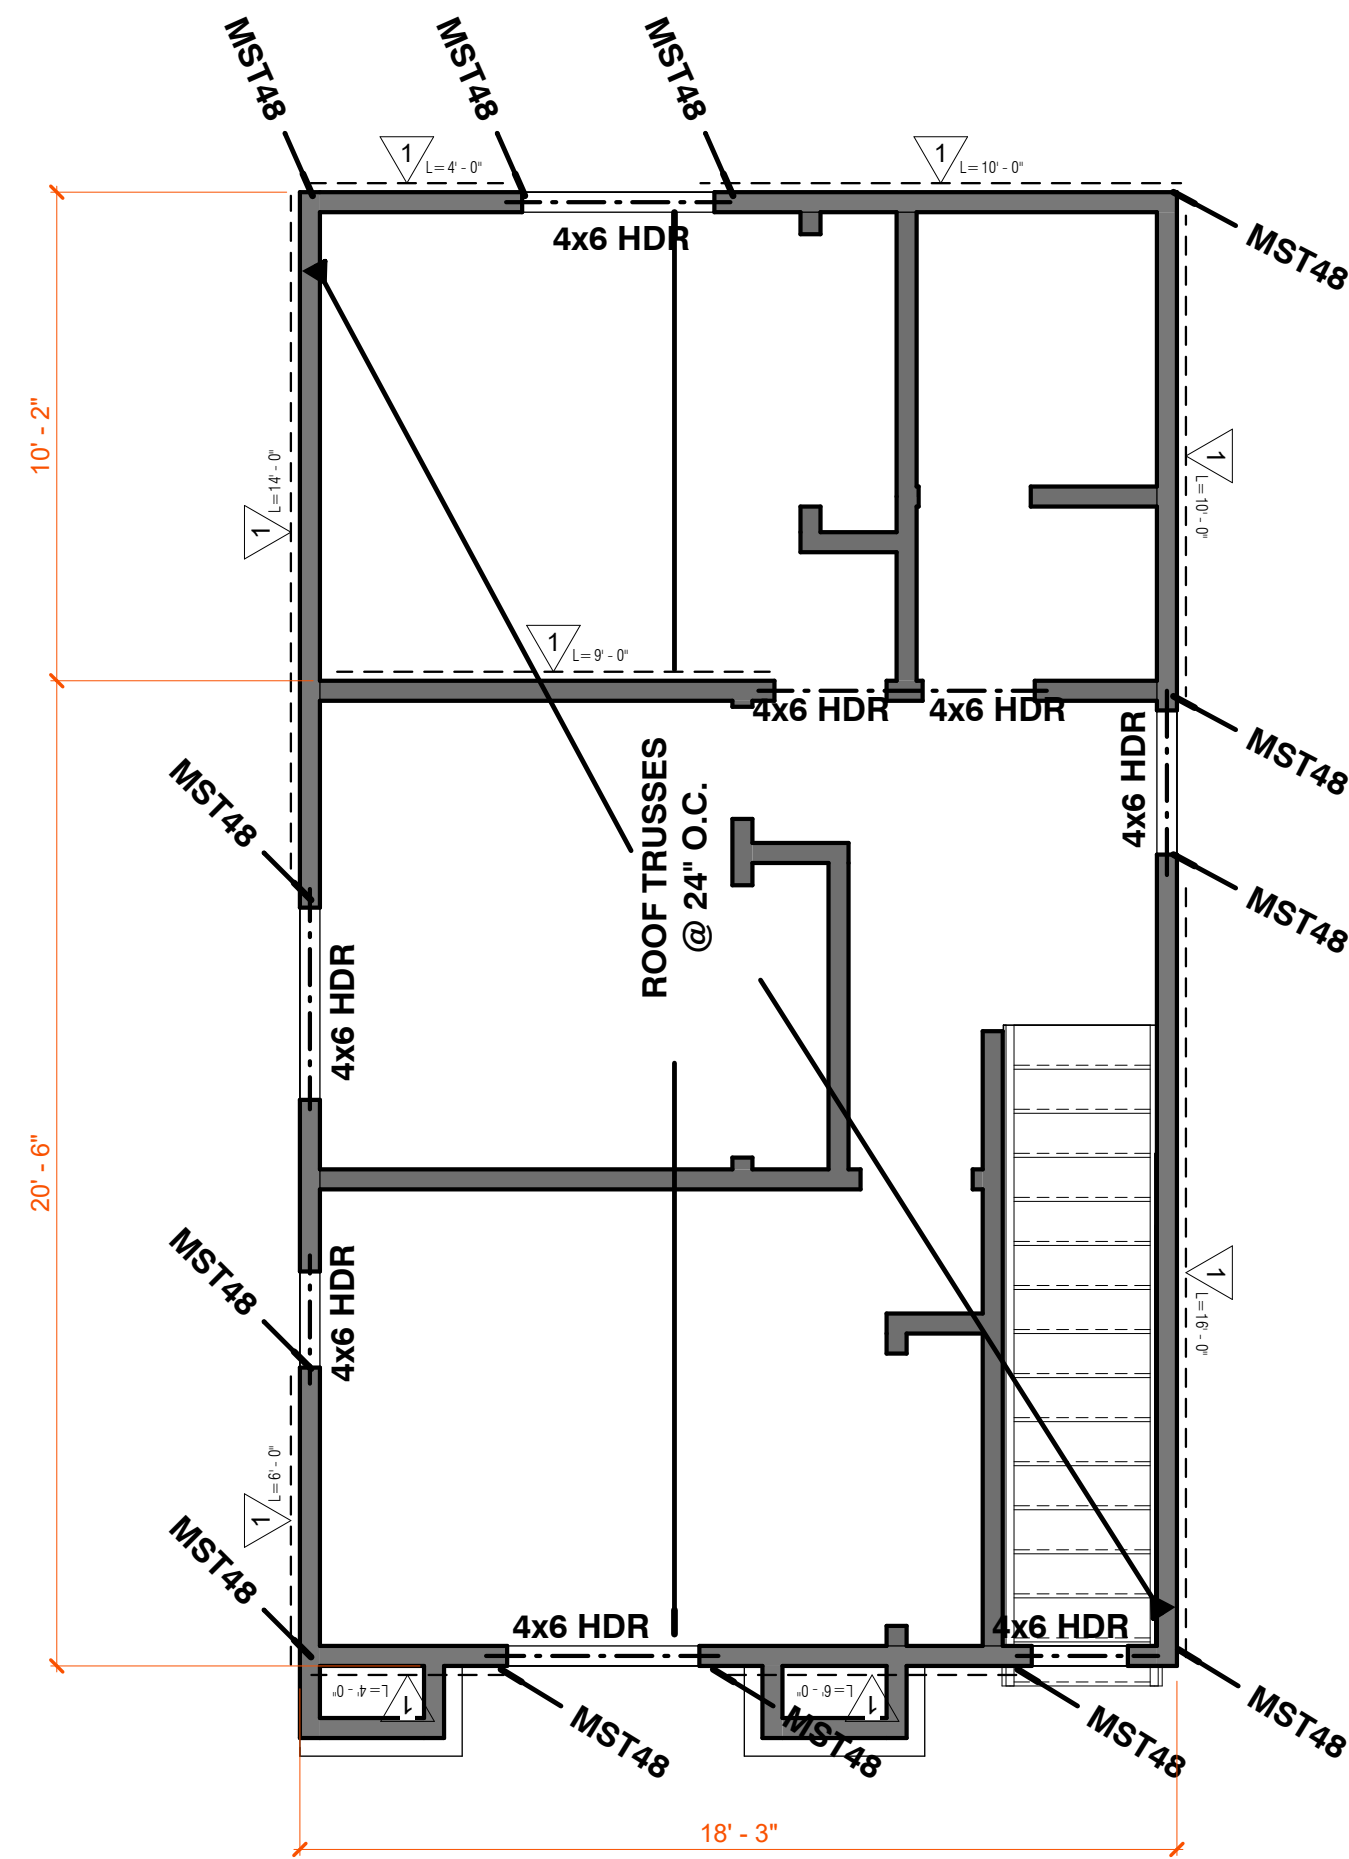

2 *2nd Floor Framing Plan*

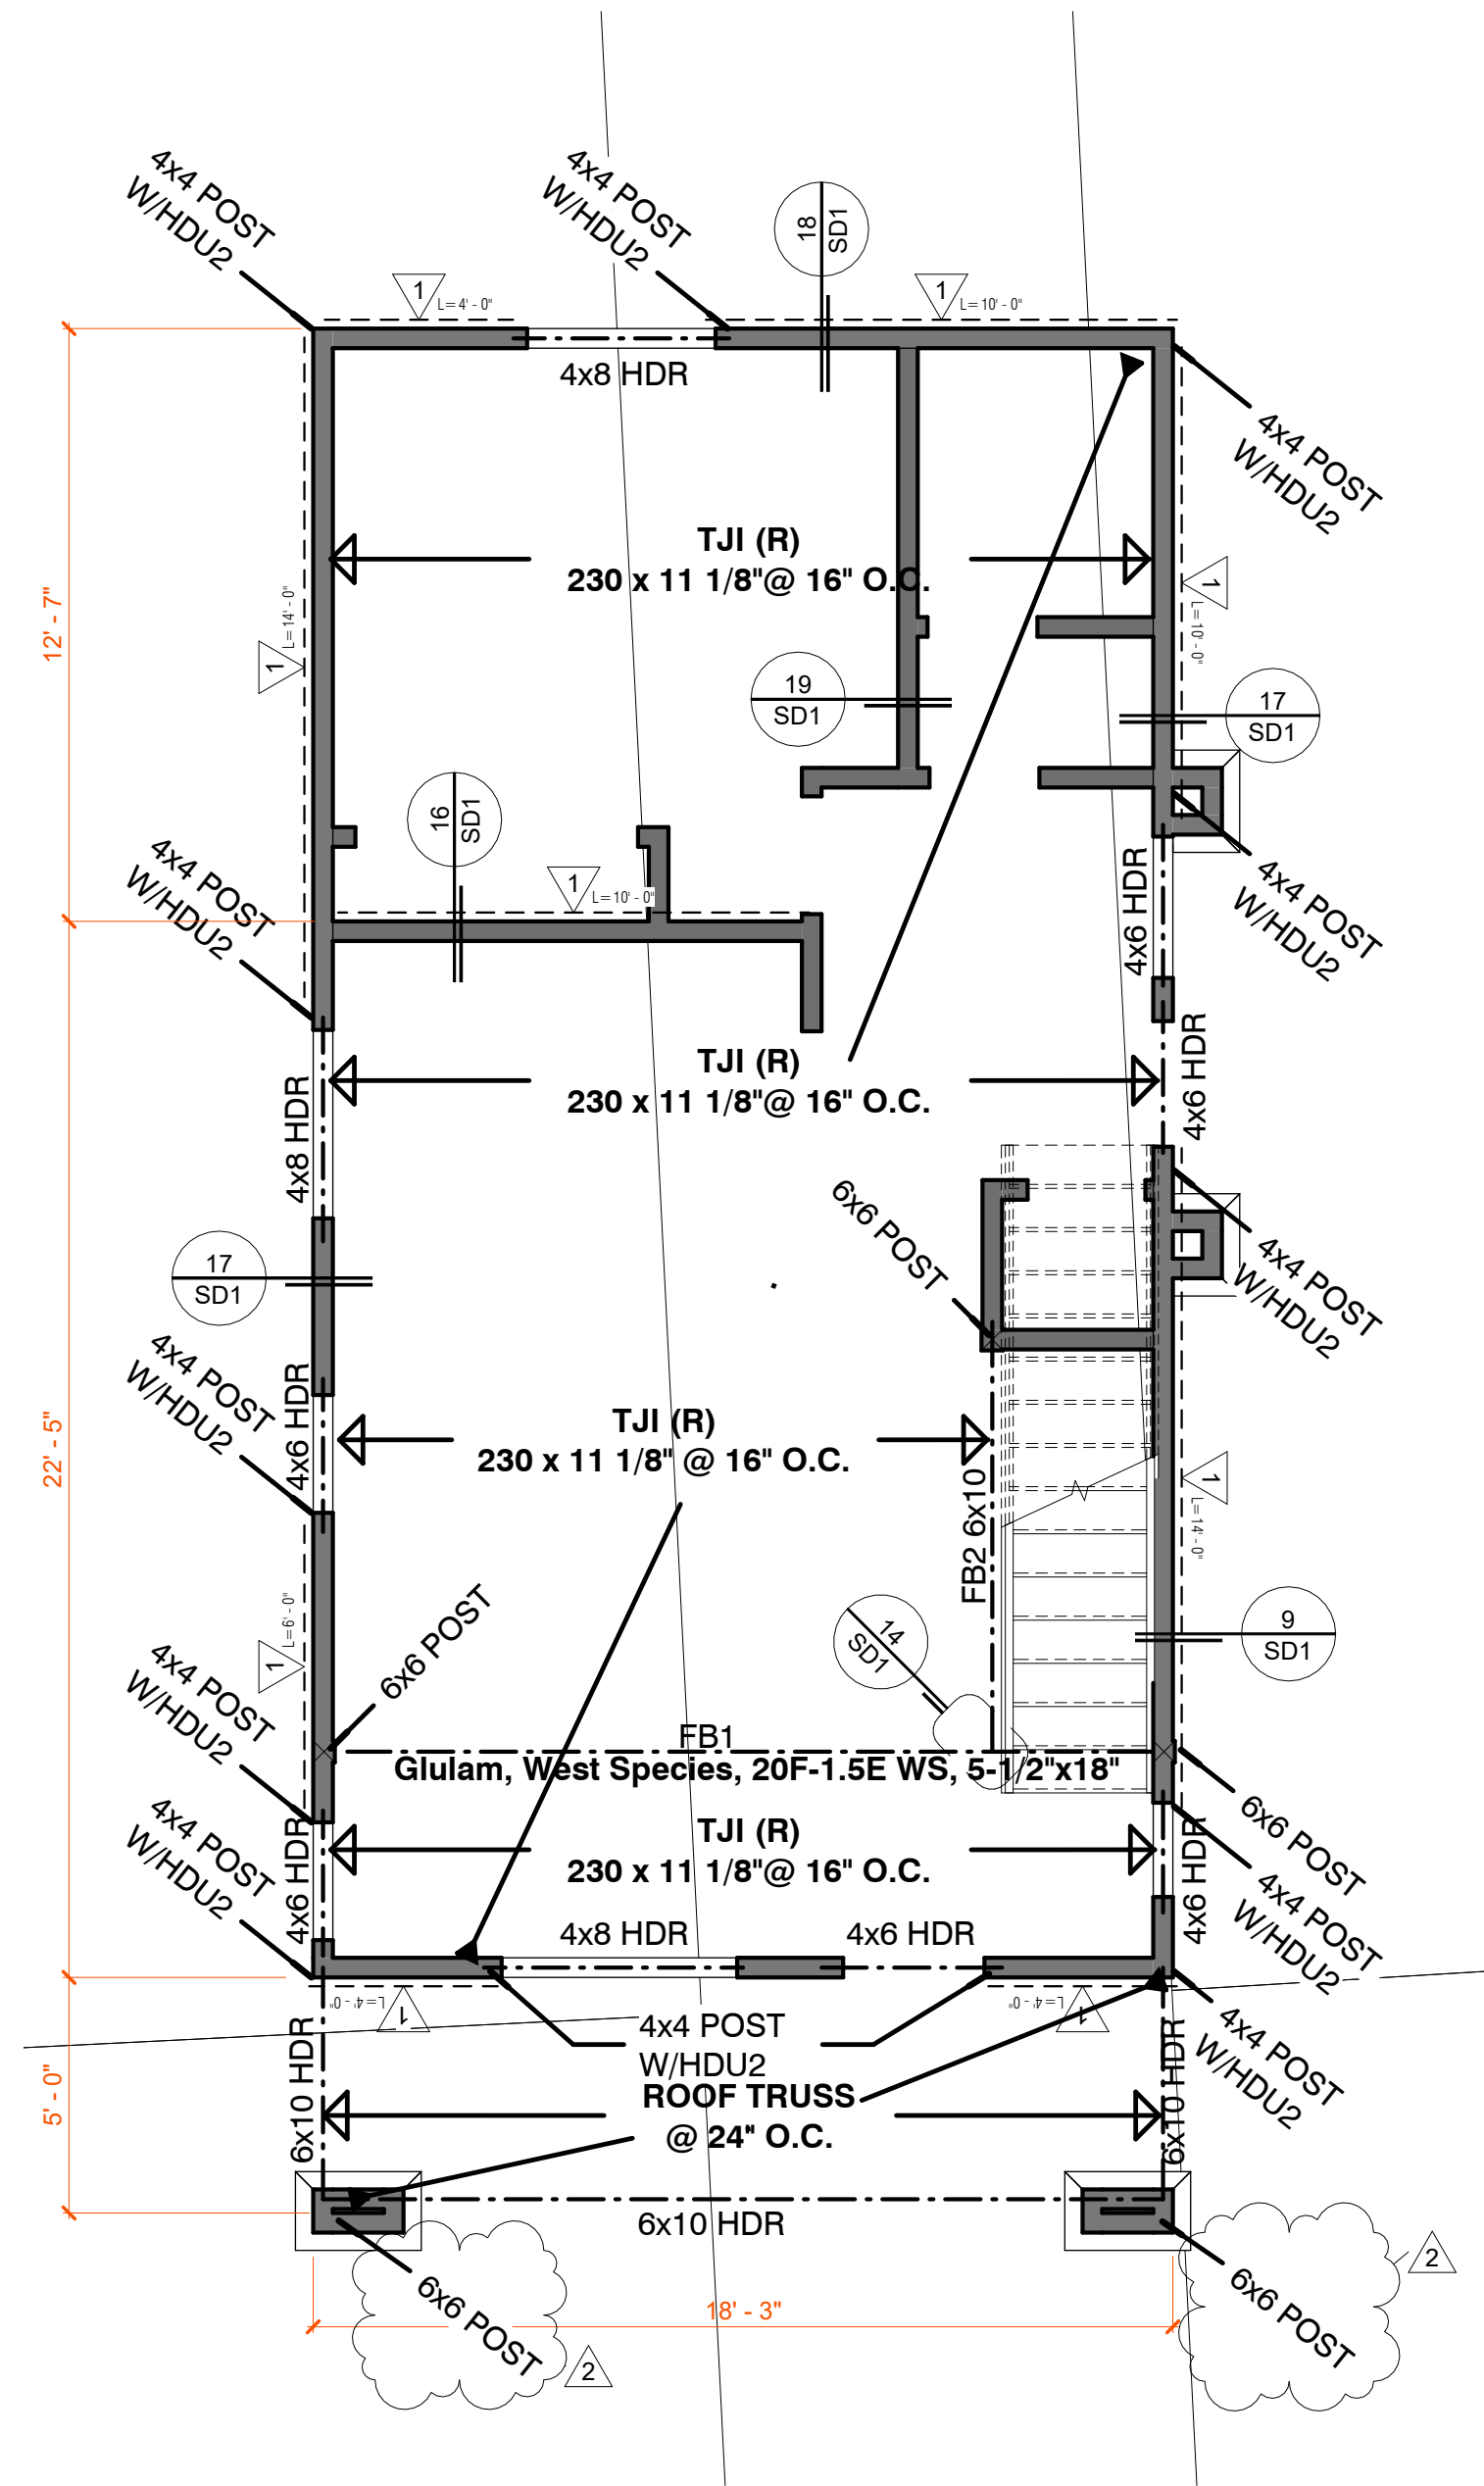

1 *1st Floor Framing Plan*

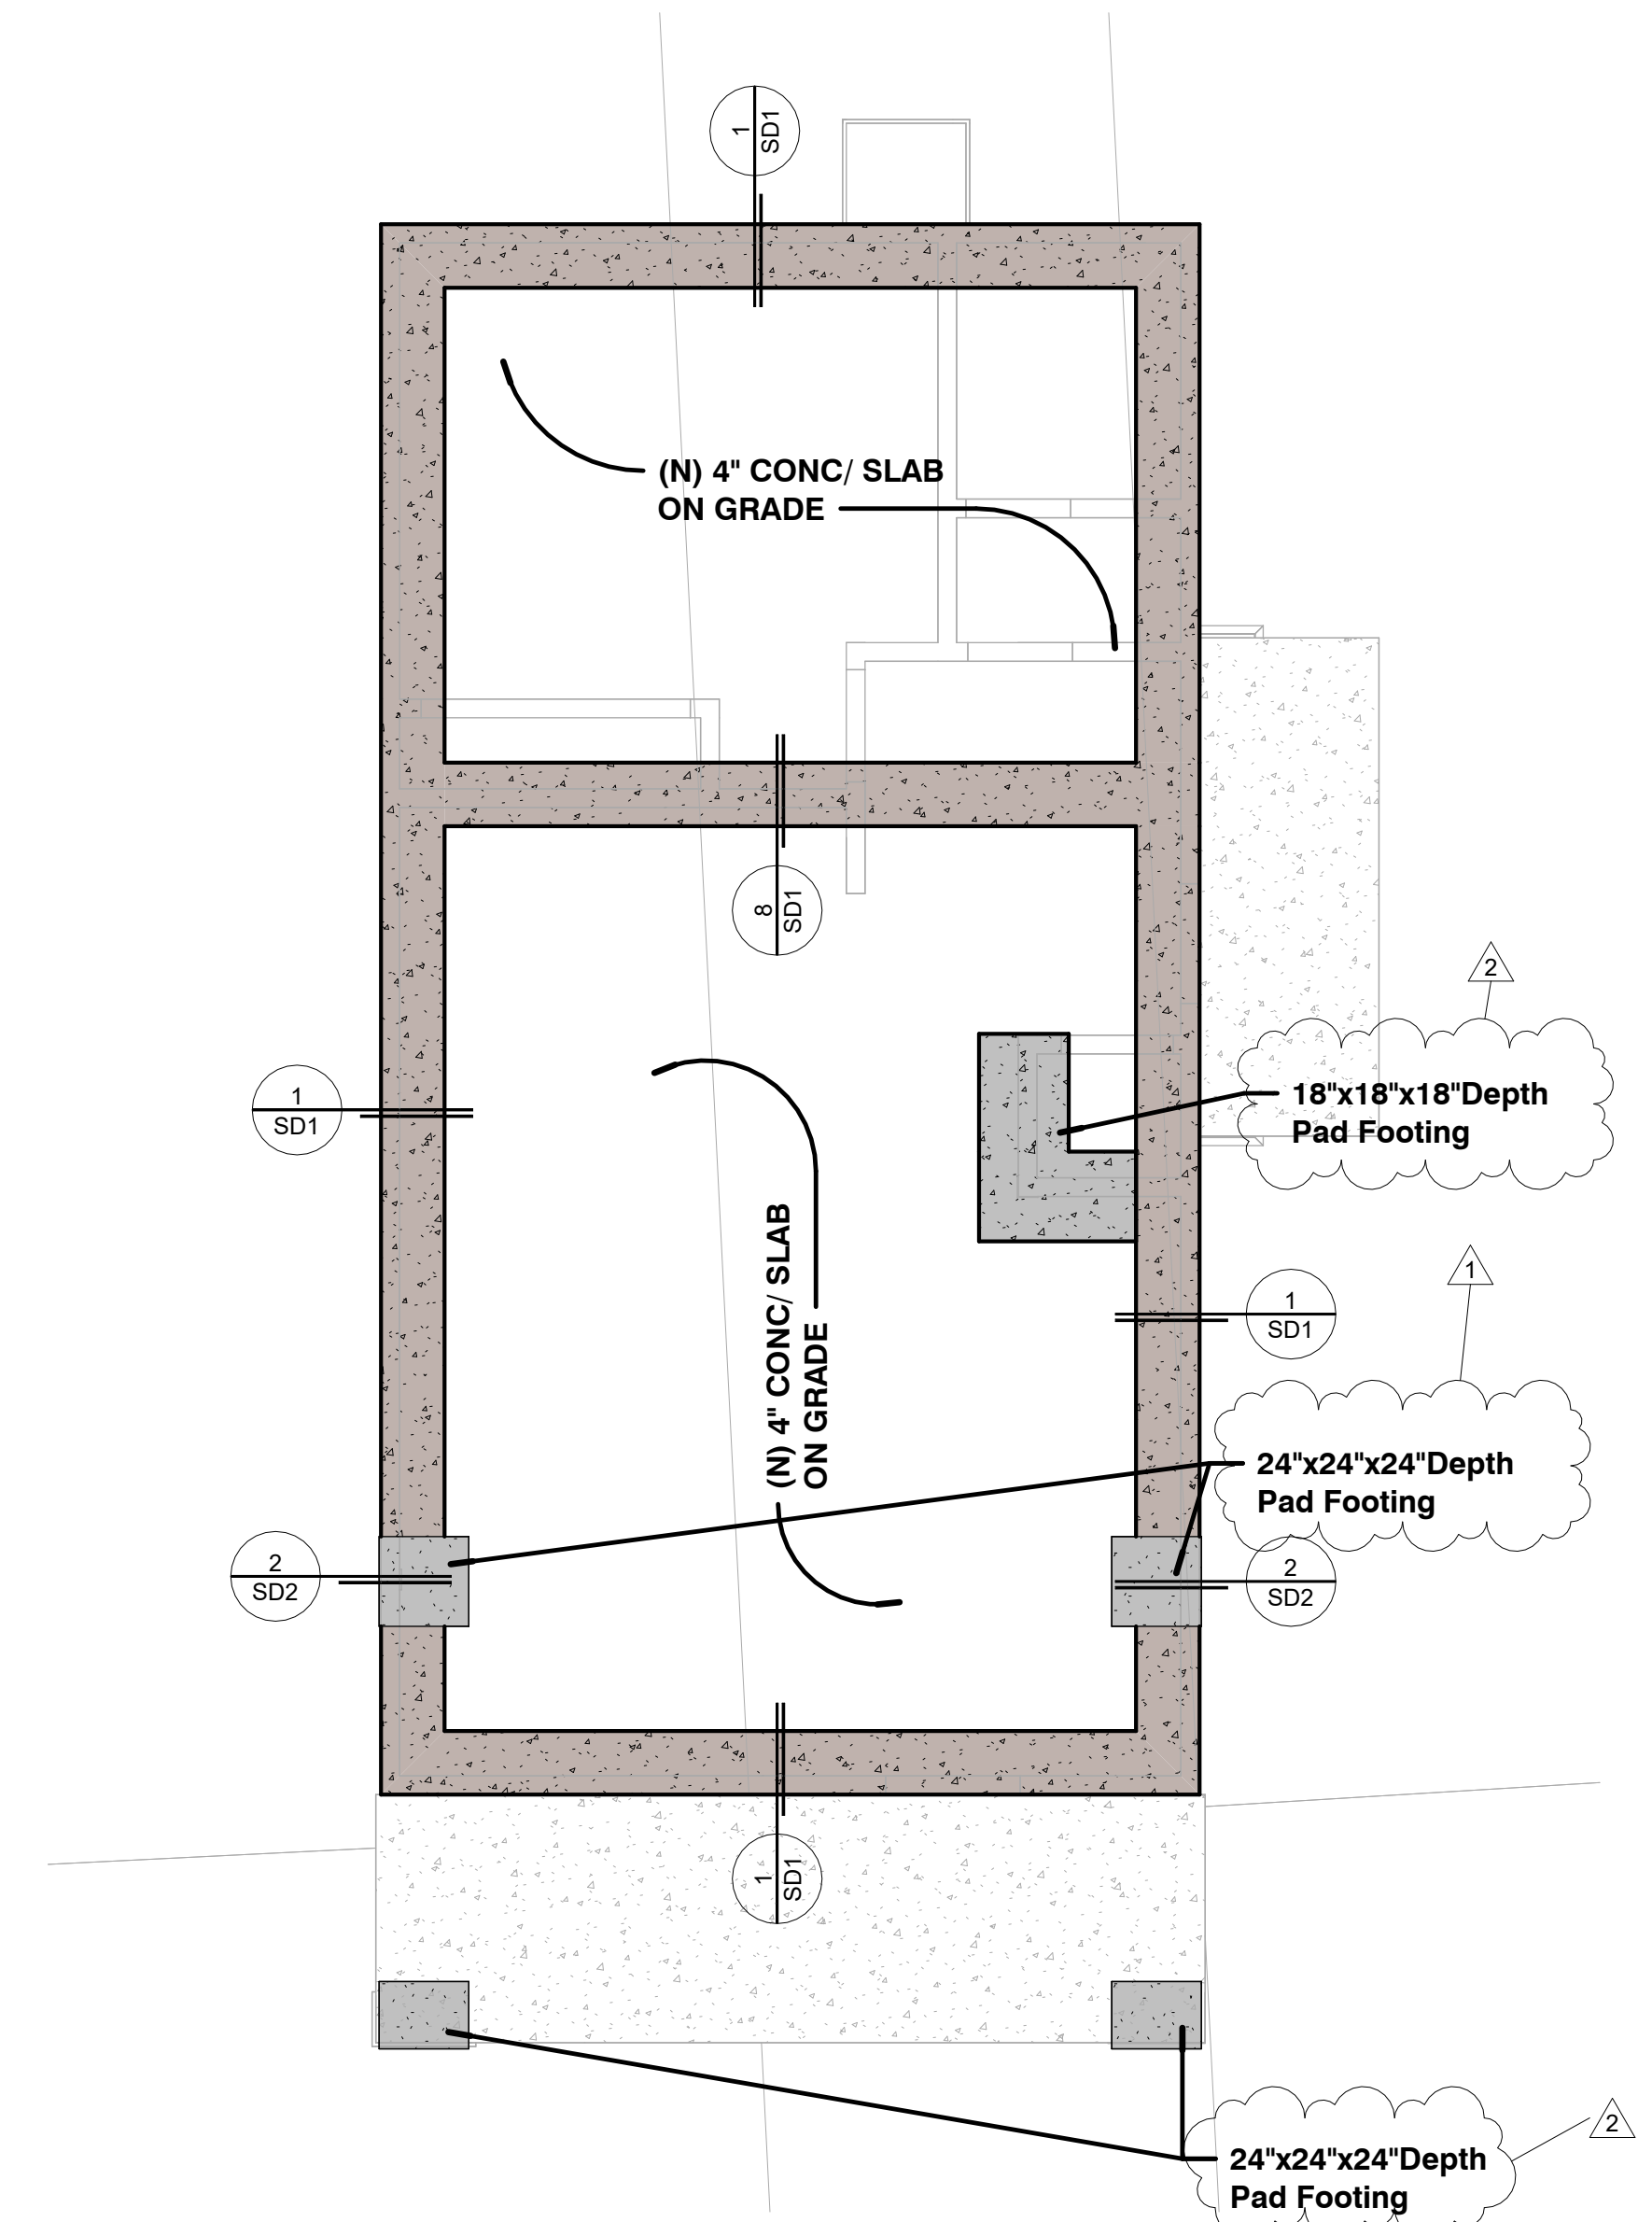

3 *Foundation Floor Plan*

A CERTIFICATE OF SATISFACTORY COMPLETION OF WORK REQUIRING SPECIAL INSPECTION MUST BE COMPLETED AND SUBMITTED TO THE INSPECTION SERVICES DIVISION".

1. ALL OTHER SPECIFICATION FOR STANDARD
HOLD DOWN TO COMPLY WITH SIMPSON REQUIREMENTS
2. ALL HOLD DOWN MUST BE TIED INTO PLACE PRIOR TO FOUNDATION INSPECTION
3. DEPTH SPECIFIED ON SCHEDULE
4. ALL ANCHOR BOLTS SHALL HAVE A 3" 3" .229" MIN. WASHER ON TOP OF SILL PLATES

SHEAR WALL SCHEDULE										
NO.	SHEATING	EDGE NAILING	FEILD NAILING	FRAMING MEMBER	CONNECTION AT TOP PLATE	FOUNDATION ANCHORAGE	SILL PLATE NAILING TO WOOD FLOOR	CAPACITY (plf)	POST-HOL DOWN	SIMPSON HOLDOWN
1	23/32 OSB	8d @ 6"	8d @ 12"	2x	A-35 @ 16"	E18" L @ 48"	16d @ 5"	260	4x4 OR (2) 2X4	HDLI5