


KEYNOTES

- | | | | |
|---|-------------------------------|----|---------------------------|
| 1 | ROOF SHINGLE CLASS A | 8 | 2x4 STUDS @ 16" O.C. |
| 2 | STUCCO @ EXTERIOR | 9 | ROOF TRUSS |
| 3 | 4" MIN. CONC. SLAB ON GRADE | 10 | R-15 BATT INSULATION |
| 4 | 1/2" GYP. BD. | 11 | R-30 BATT INSULATION |
| 5 | WEEP SCREED | 12 | FOOTING PER DETAIL ON SD1 |
| 6 | PRESSURE TREATED BOTTOM PLATE | 13 | |
| 7 | DOUBLE TOP PLATE | 14 | |


KEYNOTES SECTION

1 1/2" = 1'-0"


2nd Floor Plan
11' - 8"

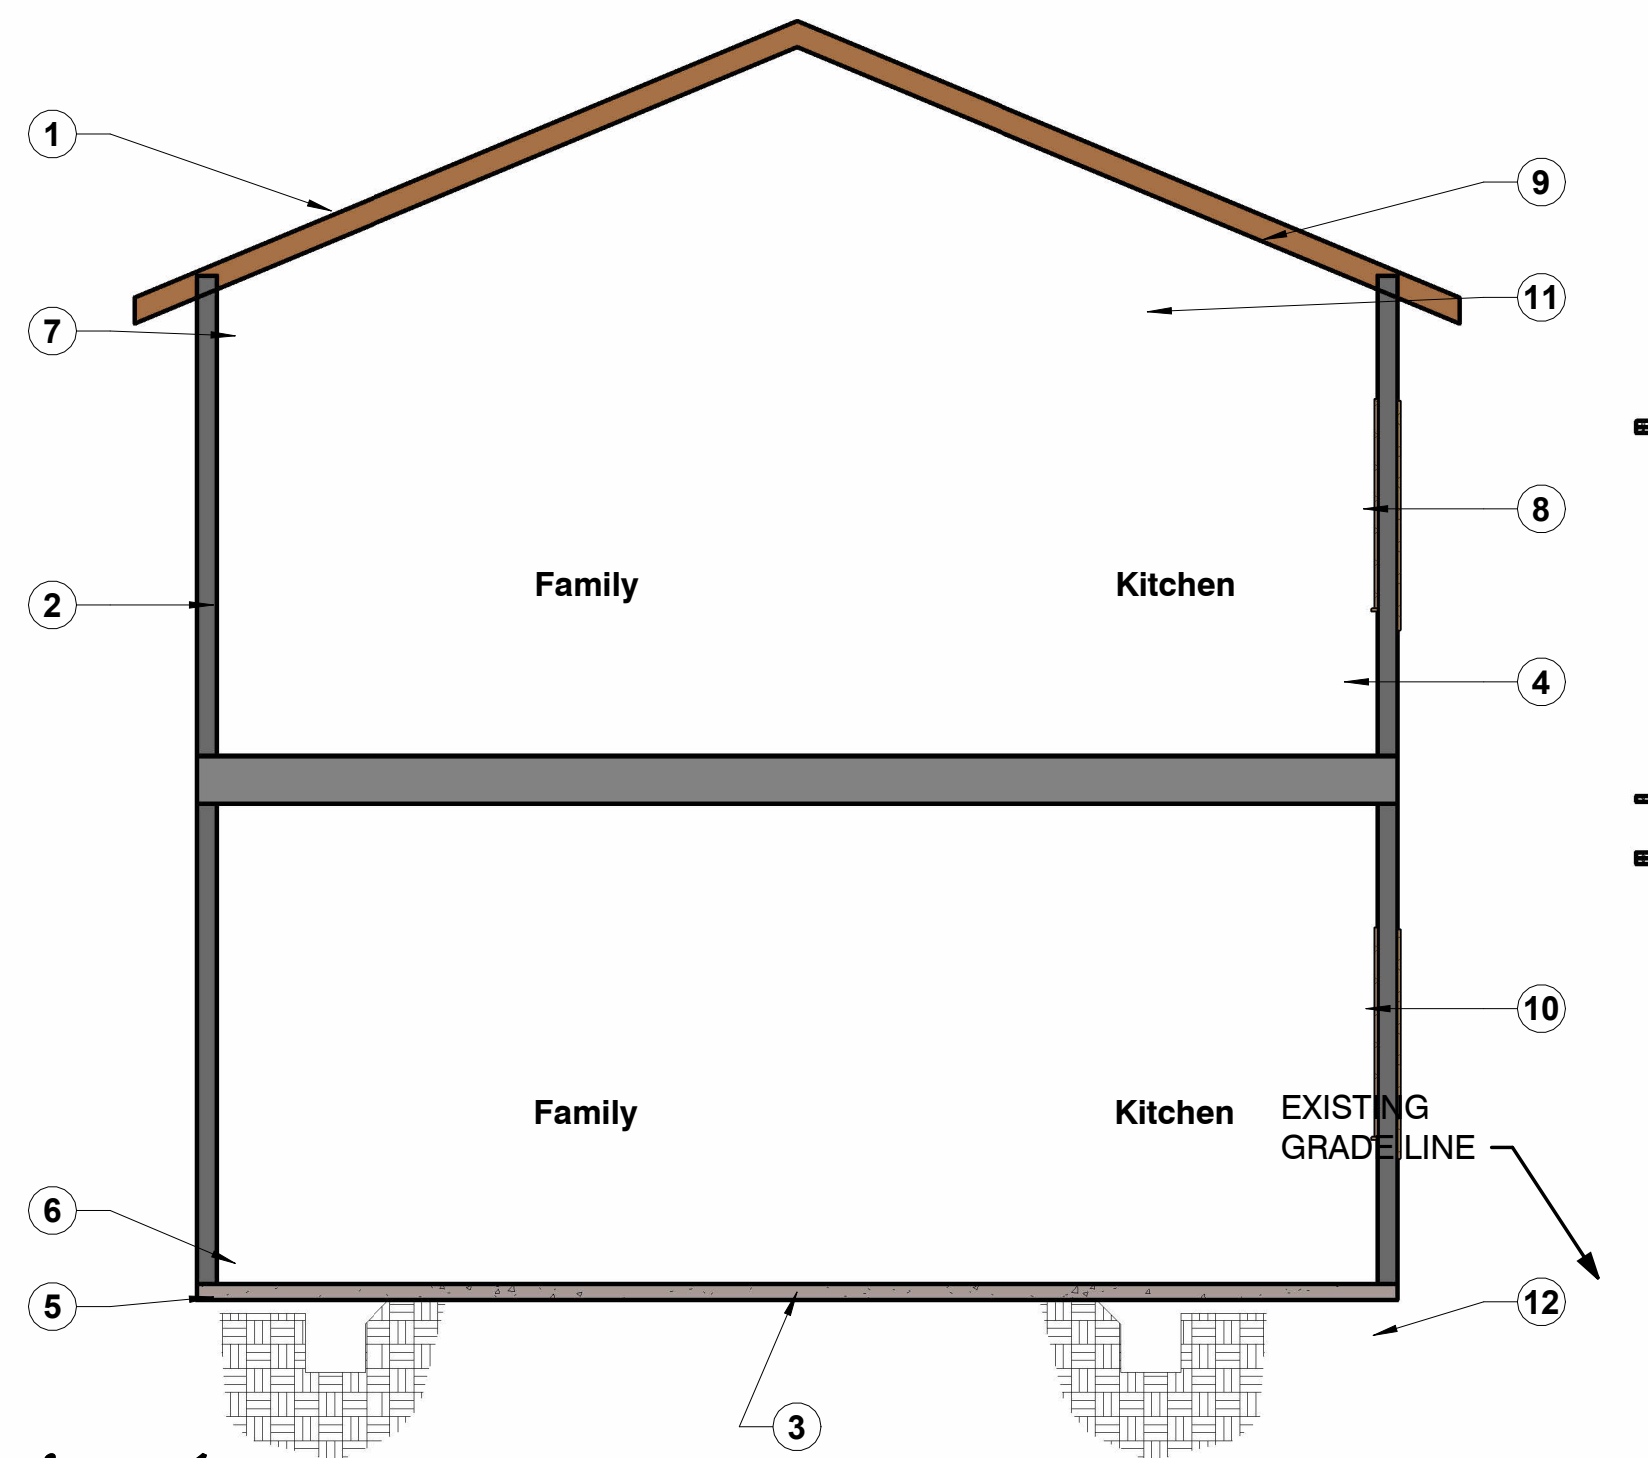


1 *ADU-Section 1*
1/4" = 1'-0"

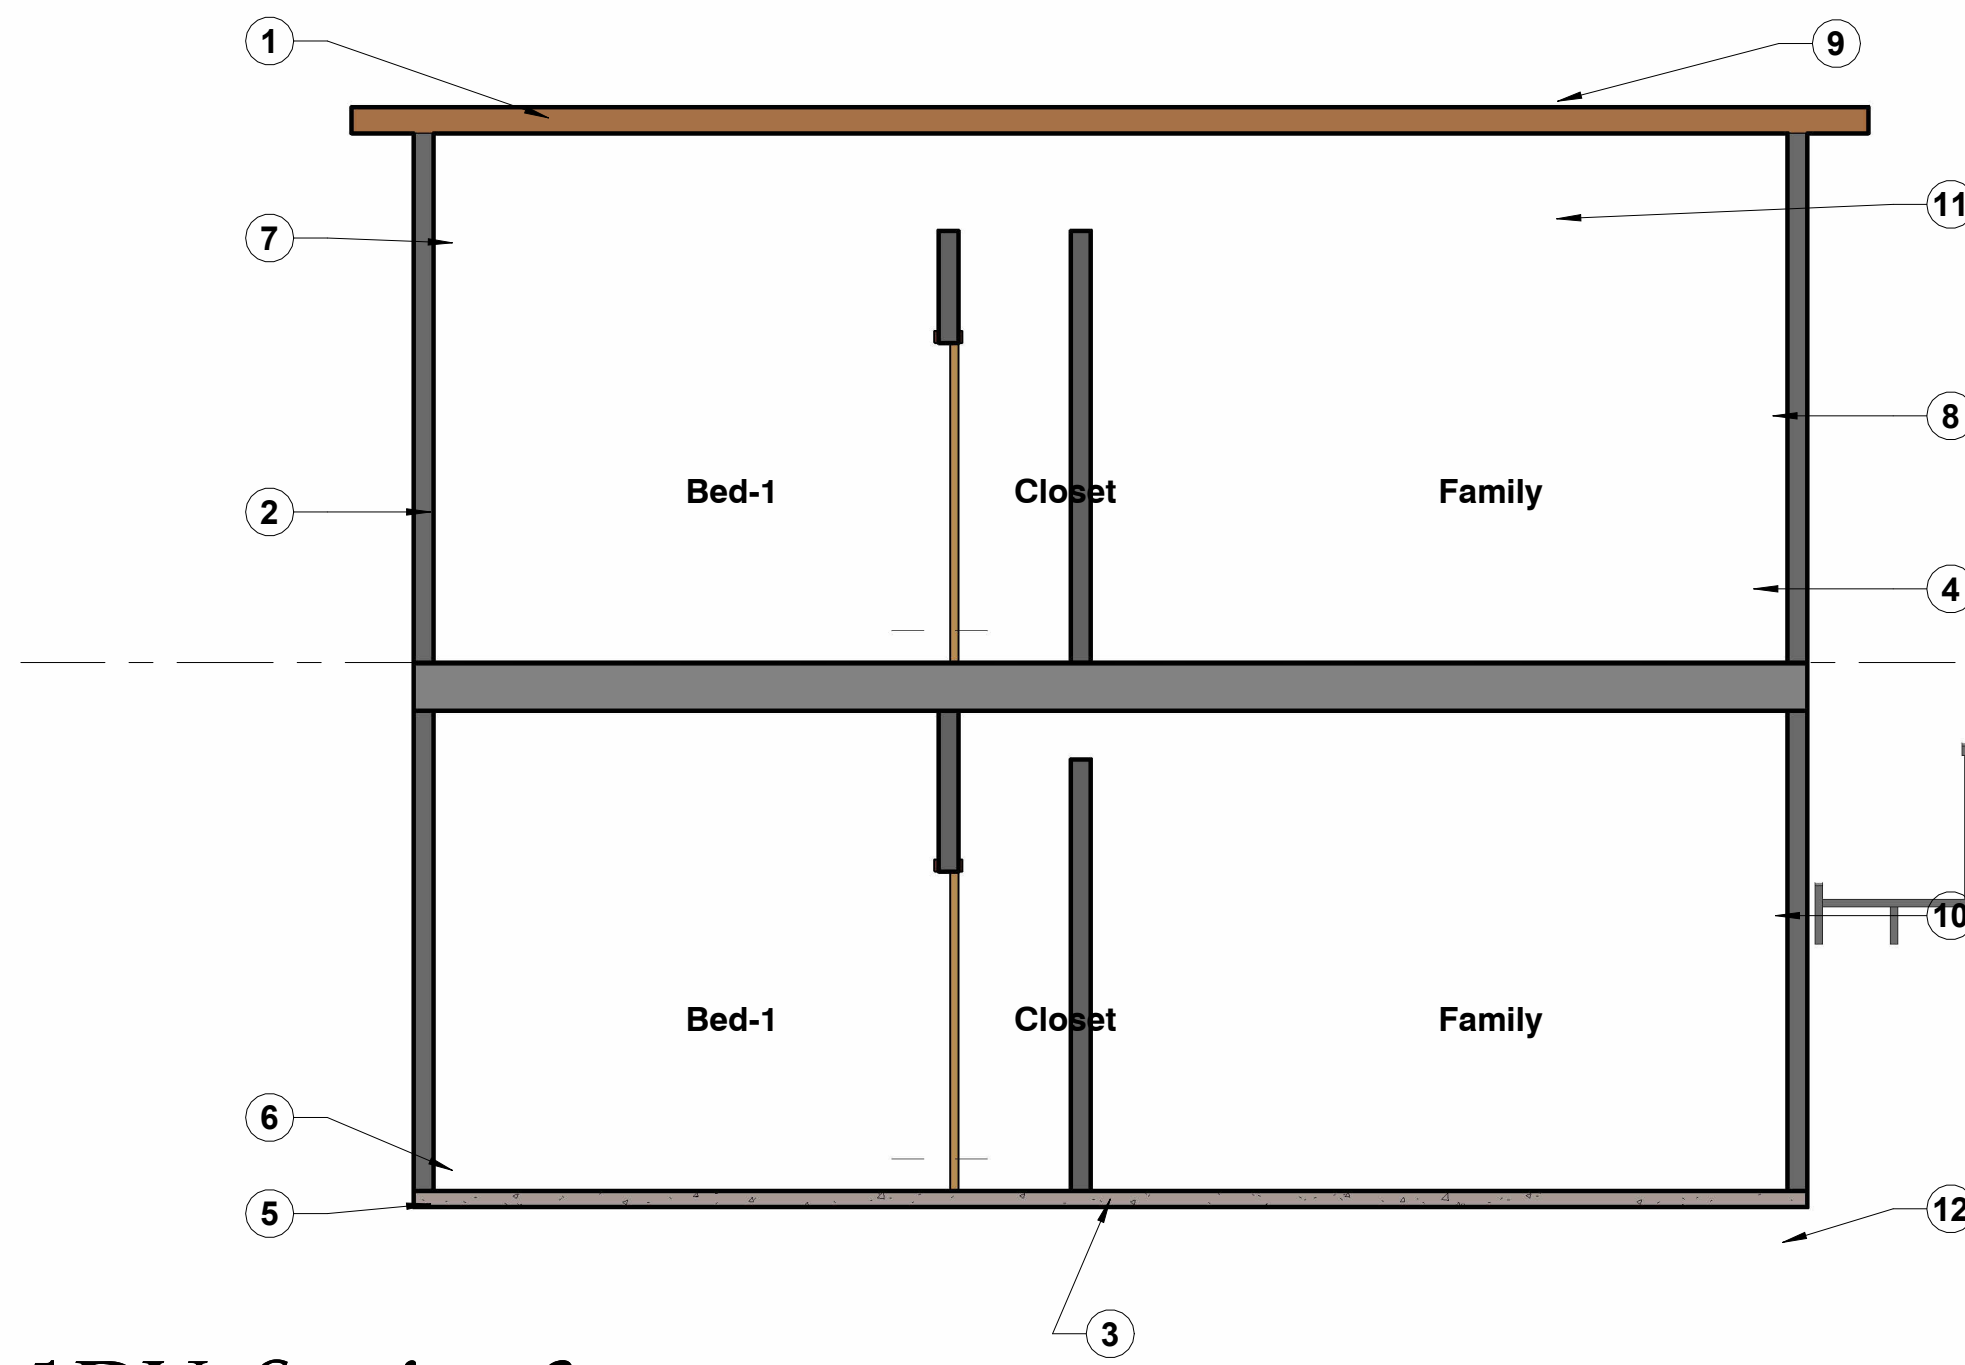

3 *ADU-Section 3*
1/4" = 1'-0"

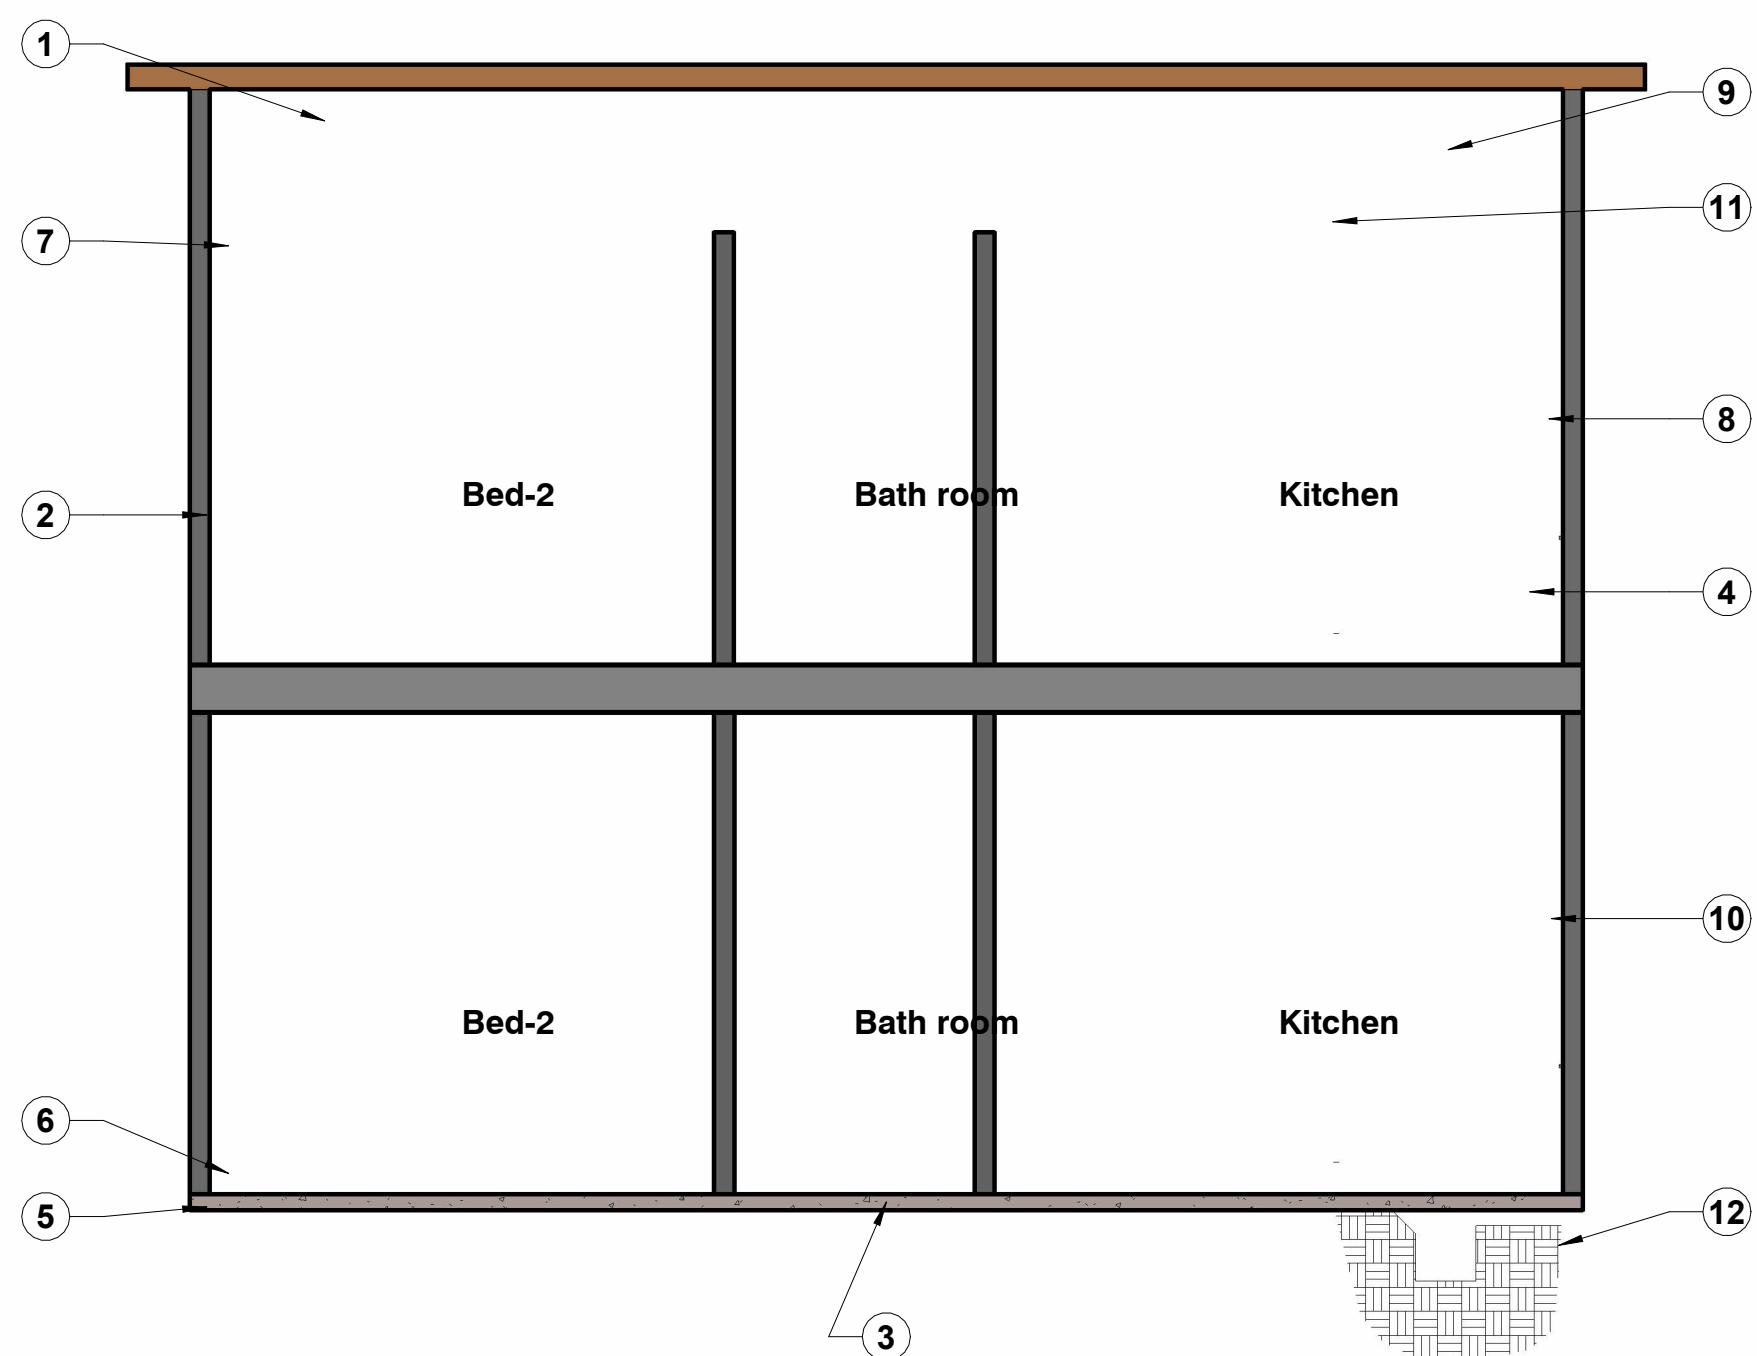

2 *ADU-Section 2*
1/4" = 1'-0"

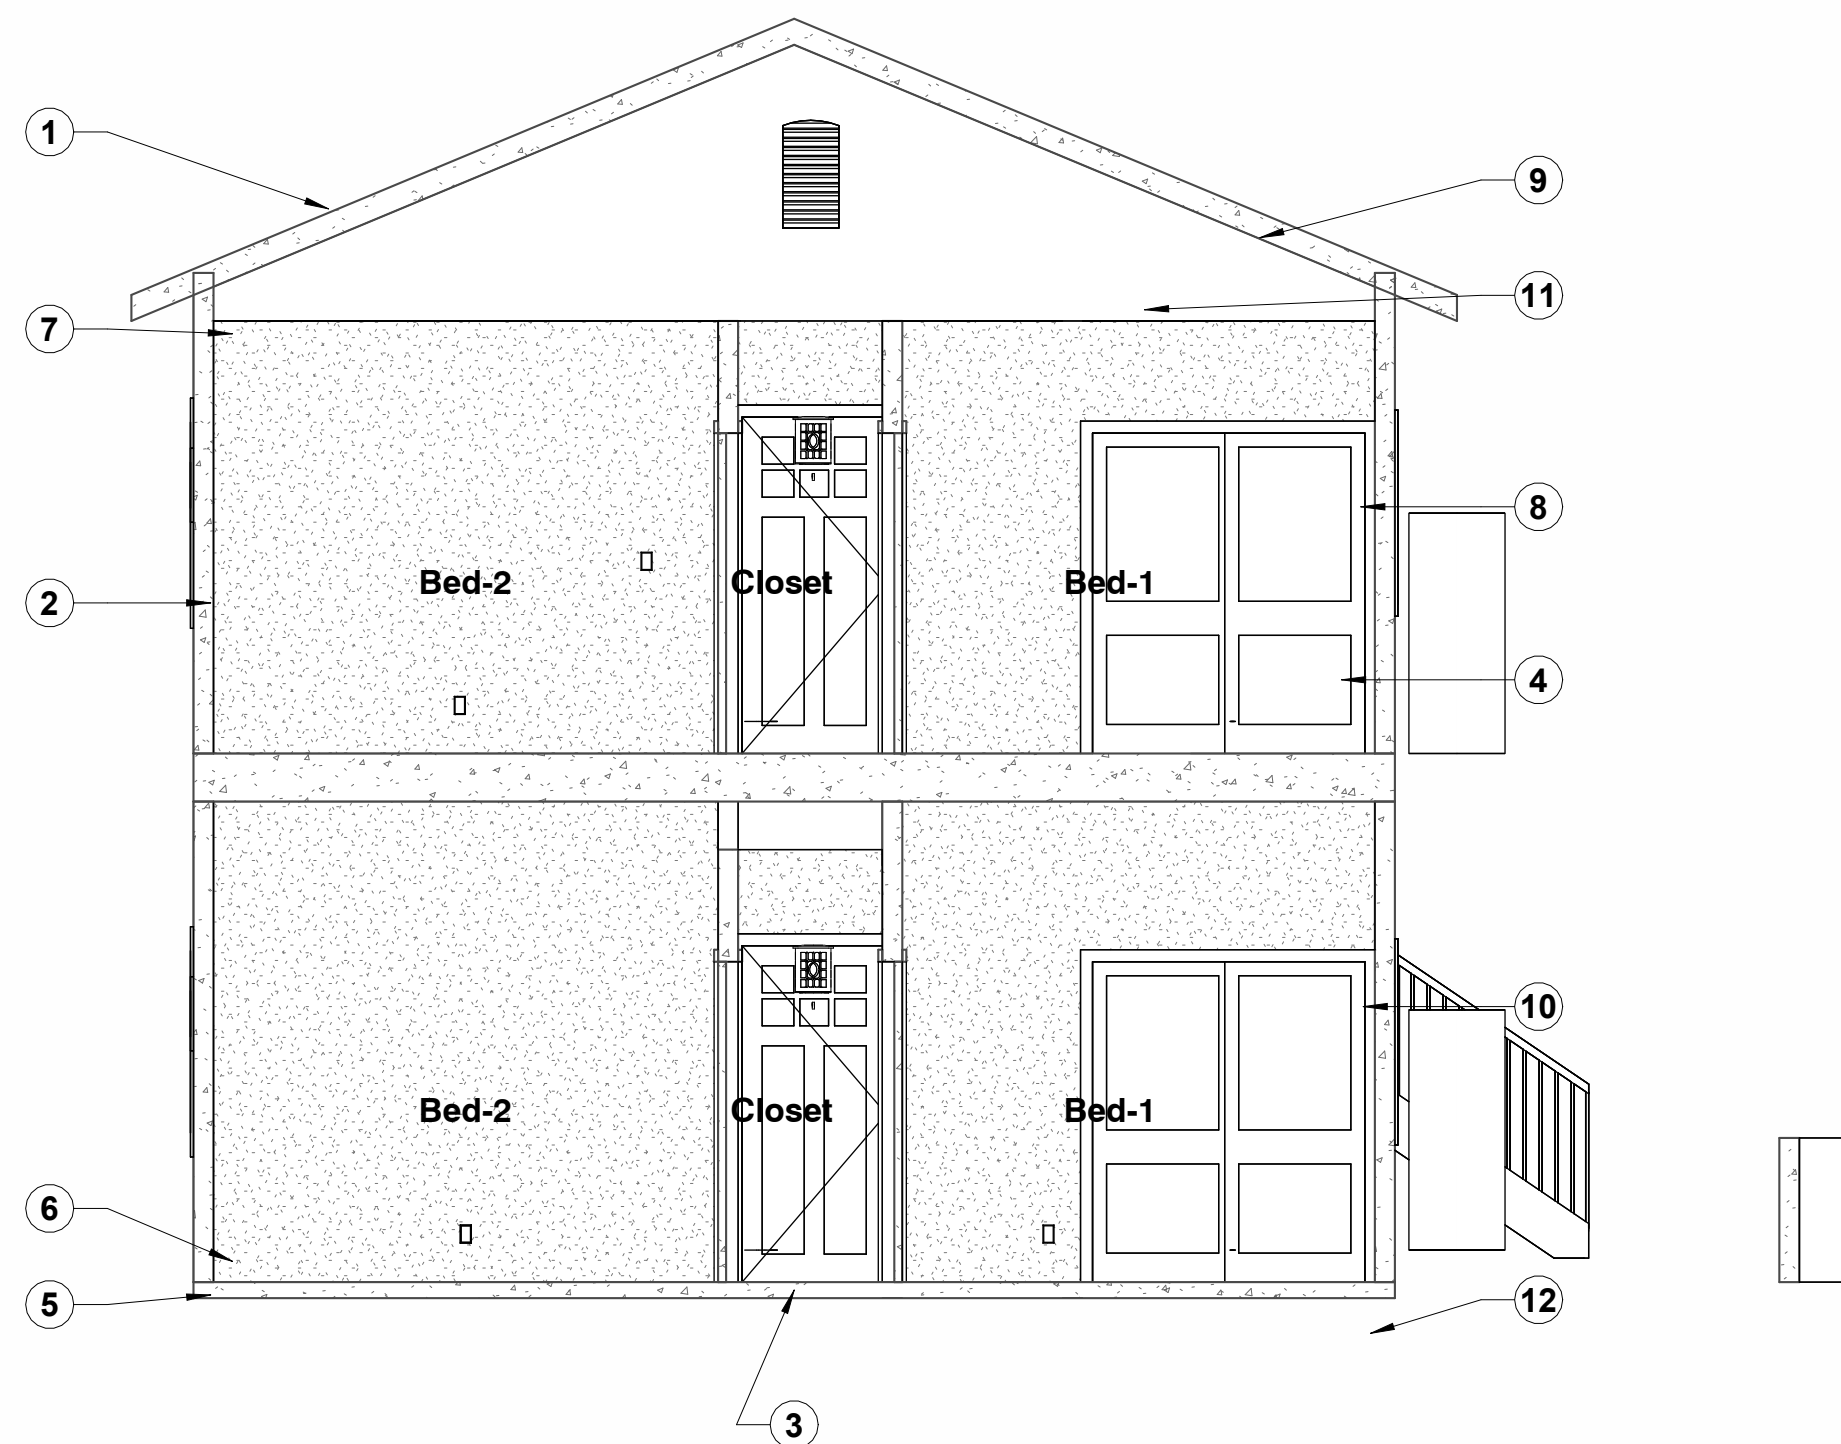

4 *ADU-Section 4*
1/4" = 1'-0"

4439 Keeler Ave ADU

4439 Keeler Ave.
San Diego, CA 92113



Revision Dates	
1	08.15.24
2	01.01.25

SHEET TITLE

Sections

Drawing Date

08.24.26

Check By

Francis N.

Scale

As indicated

Job Number

081623

Sheet Number

A102