



OVER 1/2" CDX PLYWOOD SHEATHING
2x8 FASCIA W/ GUTTER - TYP. AT ALL EAVES
1'-6" ROOF OVERHANG - TYP. ALL SIDES
PROVIDE ATTIC VENTILATION PER ROOF LEGEND

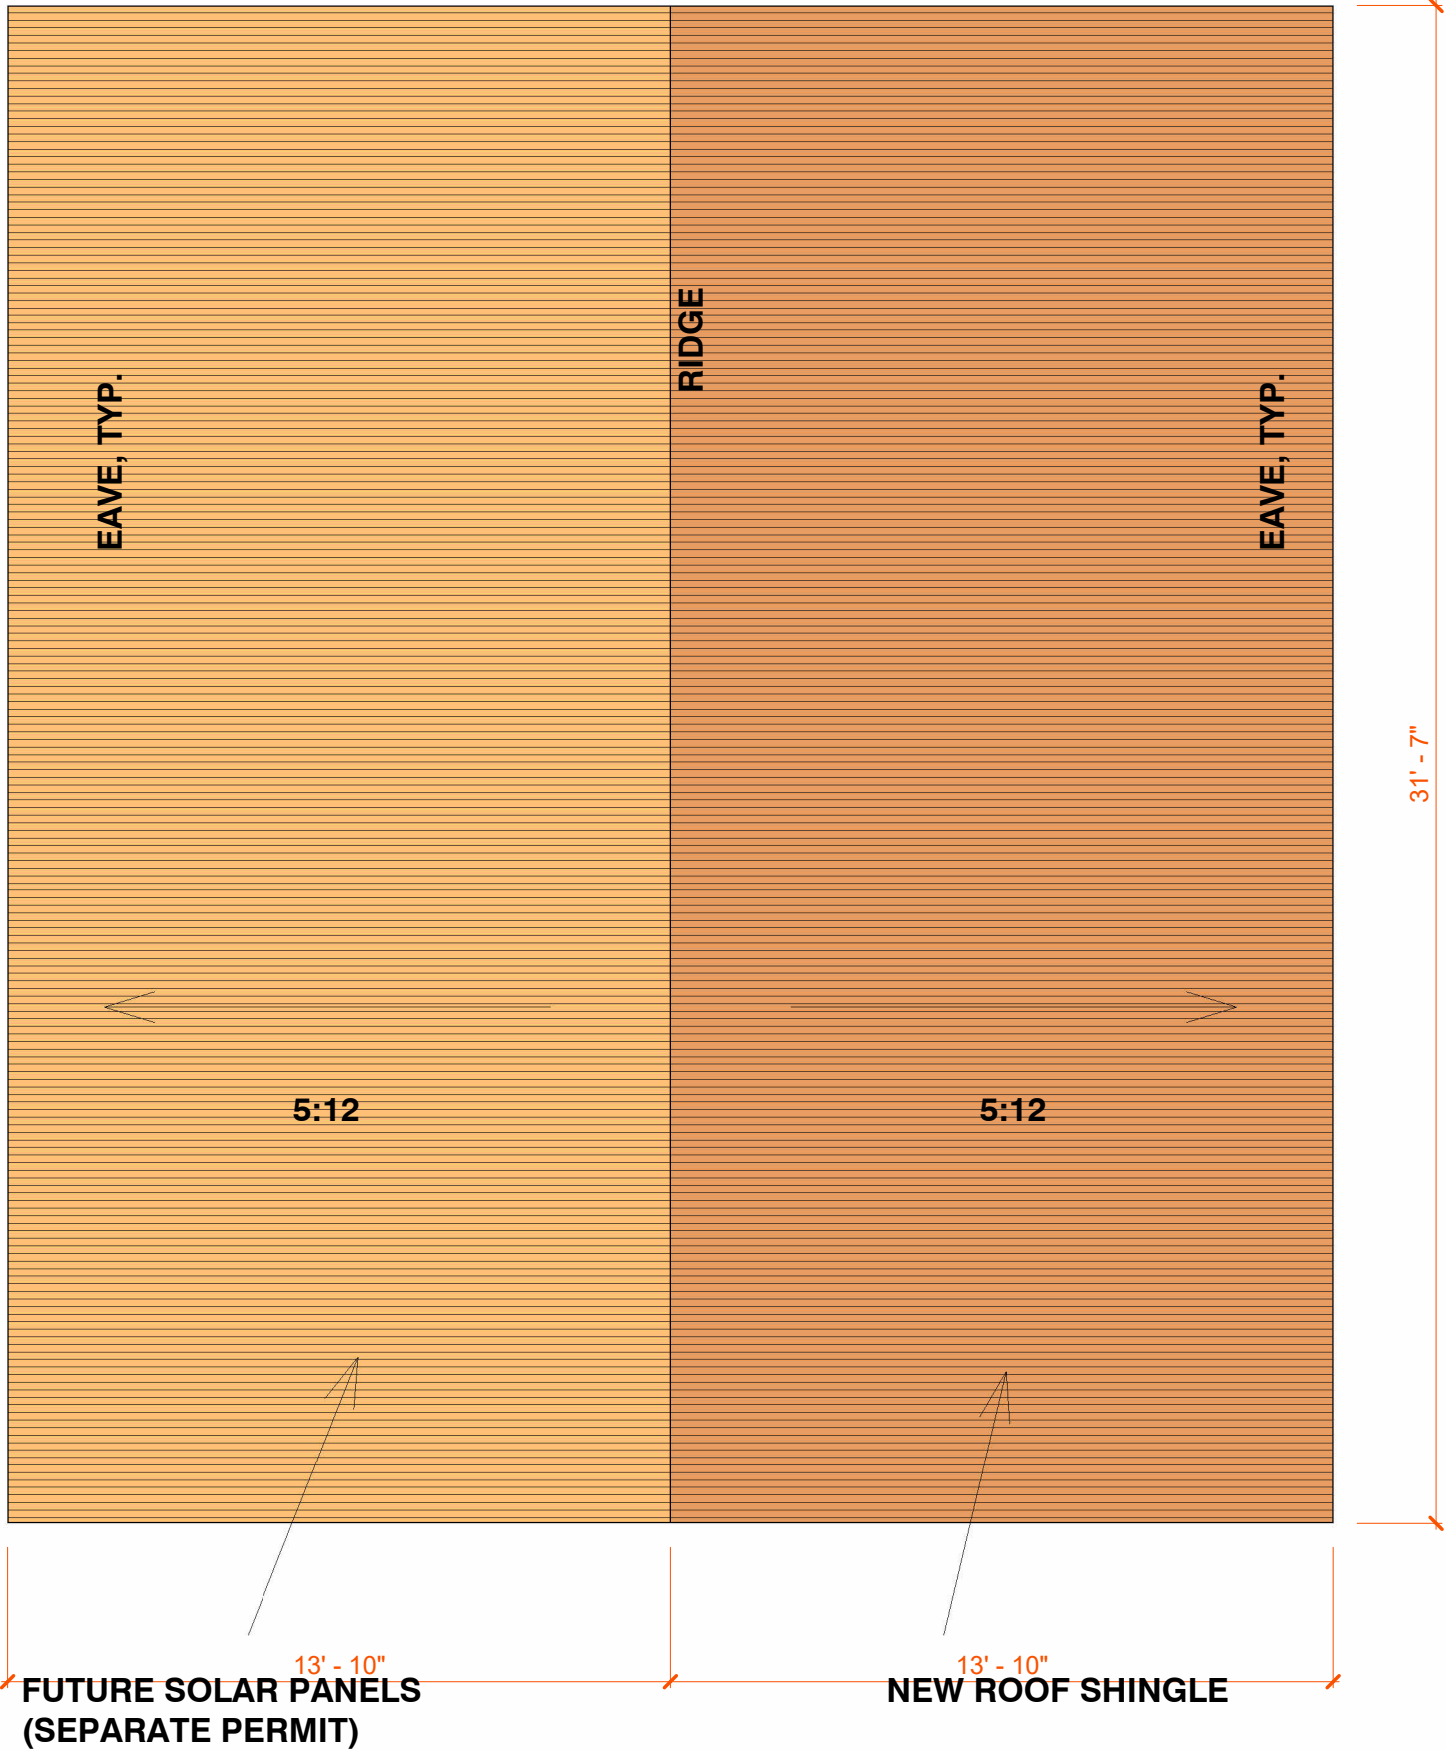

1 **ADU - Roof Plan**
1/4" = 1'-0"

TRUSS SPACING: 24" O.C. / HEEL HEIGHT: 3 15/16" U.N.O.
TAIL LENGTH: 24" U.N.O. / TAIL SIZE: 2x4 U.N.O.

PRE-ENGINEERED ROOF TRUSSES @ 24" O.C.
PER TRUSS MFR. CALCS - 5:12 PITCH
TRUSS TIE-DOWN PER DETAIL ON SD1

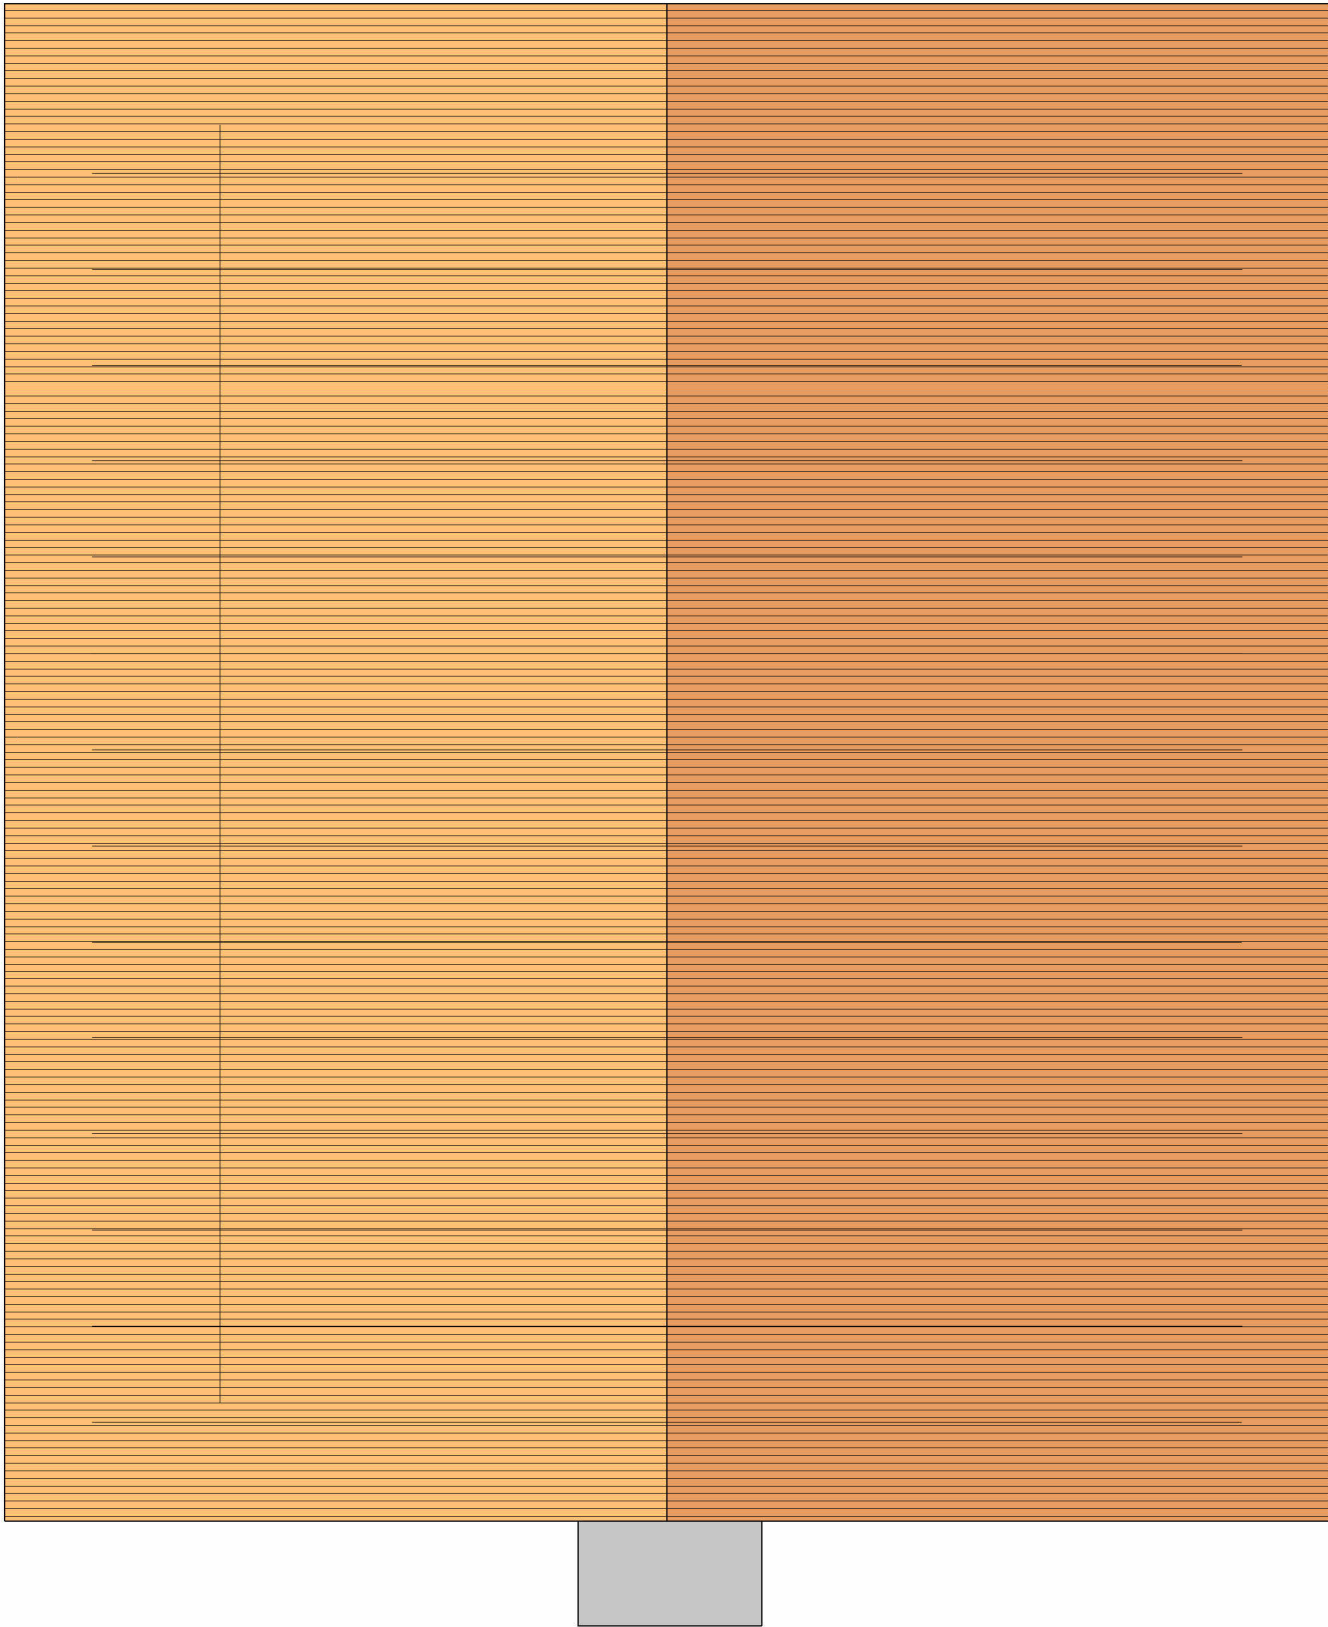

2 **ADU - Roof Framing Plan**
1/4" = 1'-0"

NOTES: ATTIC VENTILATION OPENINGS
SHALL BE COVERED W/ CORROSION-
RESISTENT METAL W/ MESH OPENINGS
OF 1/4" IN DIMENSIONS

ROOF LEGEND
ROOF SHINGLES SPEC
OWENS CORNING (OR EQ.), CLASS 'A'
ICC-ESR LISTED / CRRC RATED
OVER (1) LAYER 30# FELT