




| Revision Dates |          |
|----------------|----------|
| 1              | 08.15.24 |
| 2              | 01.01.25 |
|                |          |
|                |          |
| SHEET TITLE    |          |
| Elevations     |          |
|                |          |
| Drawing Date   |          |
| 08.24.26       |          |
| Check By       |          |
|                |          |
| Drawn By       |          |
| FRANCIS N.     |          |
| Scale          |          |
| As indicated   |          |
| Job Number     |          |
| 081623         |          |
| Sheet Number   |          |

- KEYNOTES:**
- 1 ROOF SHINGLES
  - 2 WINDOW PER SCHEDULE
  - 3 14"x24" LOUVER
  - 4 STUCCO AT EXTERIOR WALL TO MATCH EXISTING
  - 5 EXTERIOR LIGHT
  - 6 EXTERIOR DOOR SCHEDULE
  - 7




**2** ADU - South Elevation

1/4" = 1'-0"

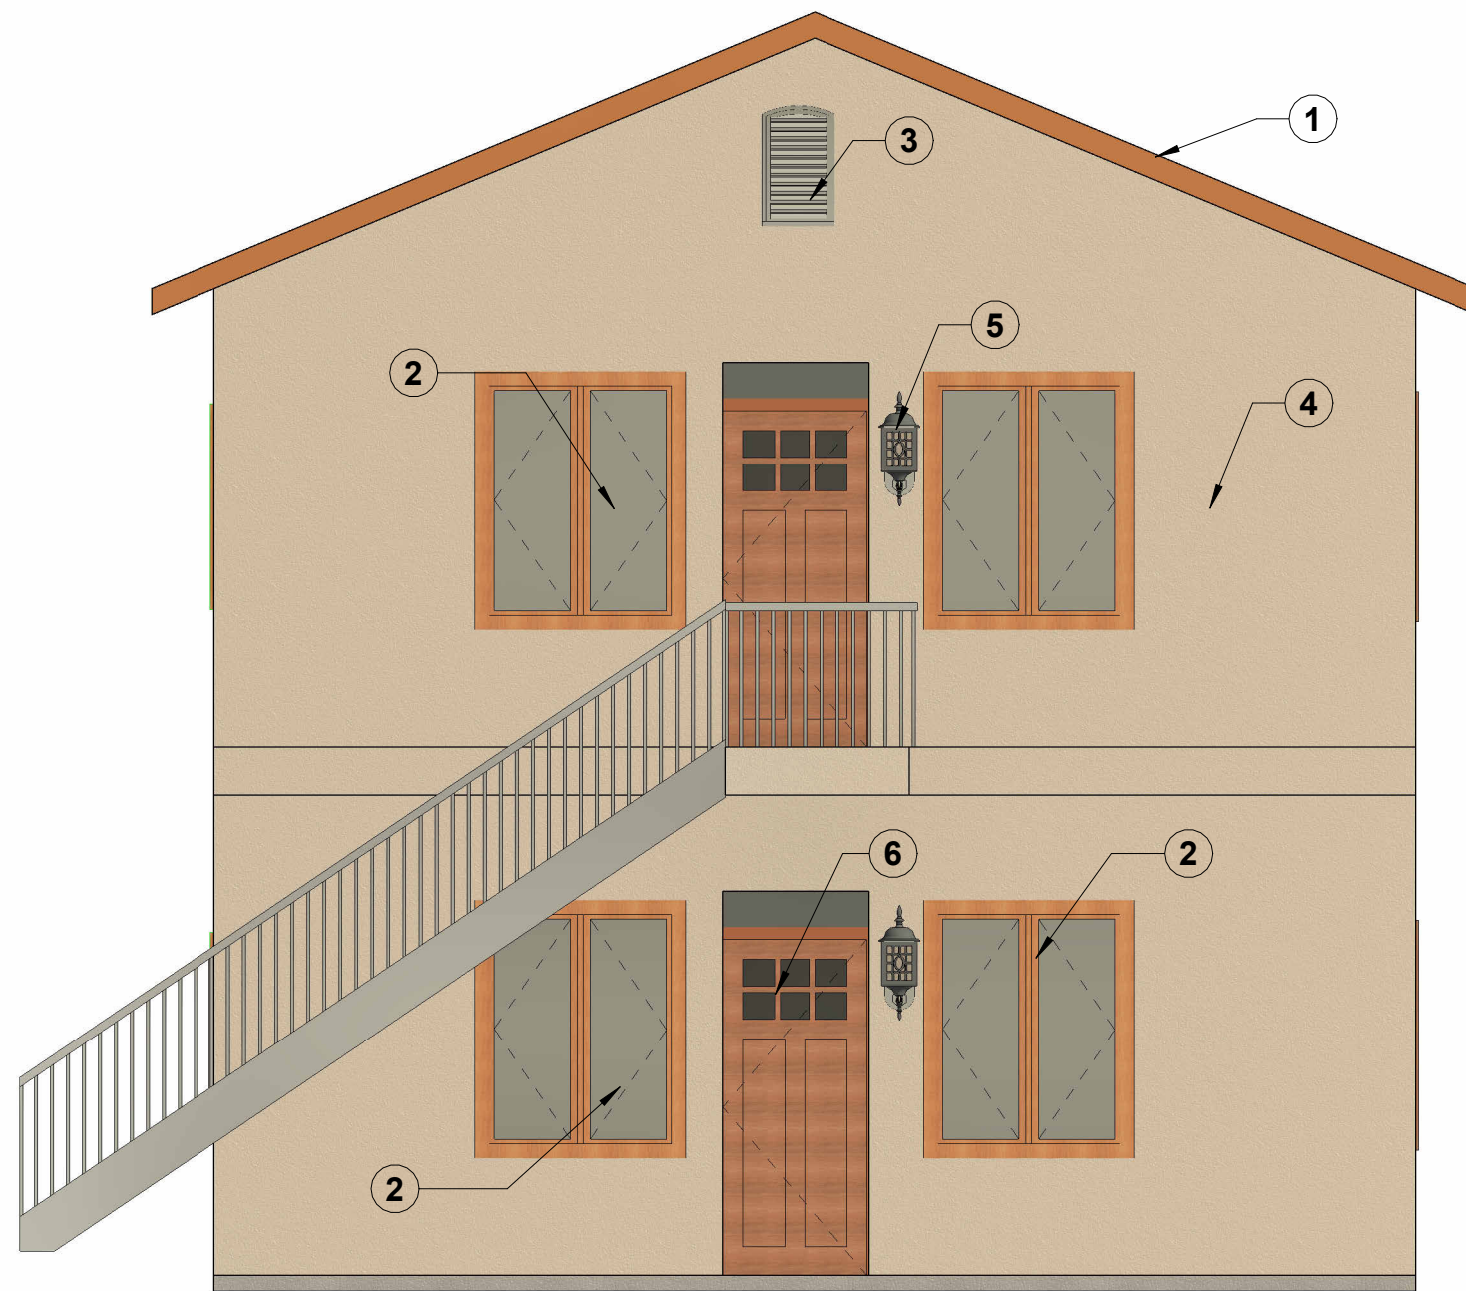


**3** ADU - West Elevation

1/4" = 1'-0"

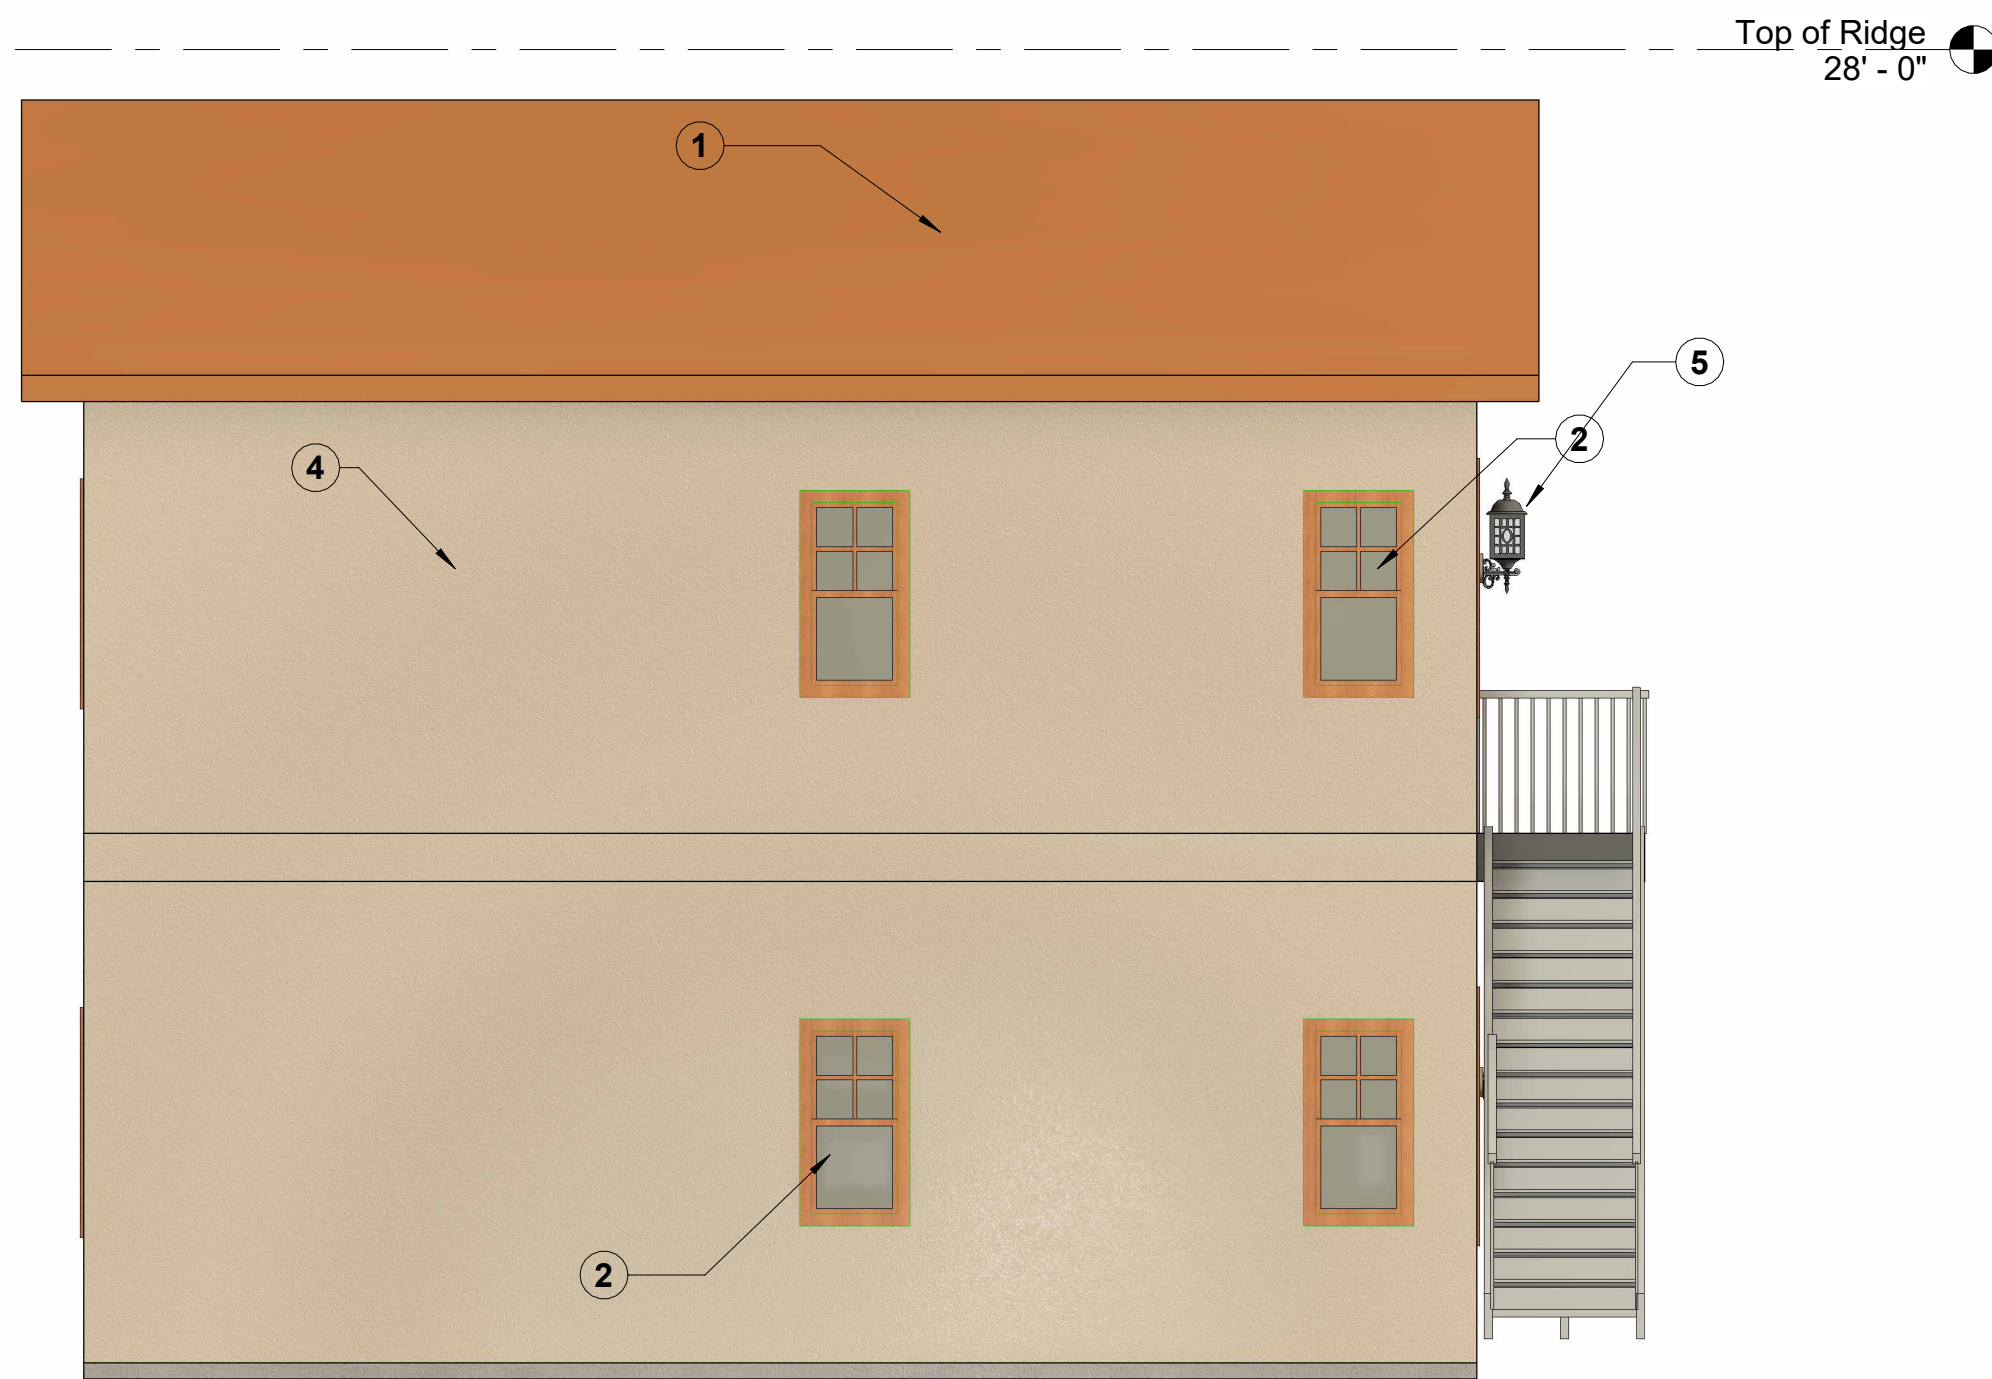

**1** ADU - North Elevation

1/4" = 1'-0"

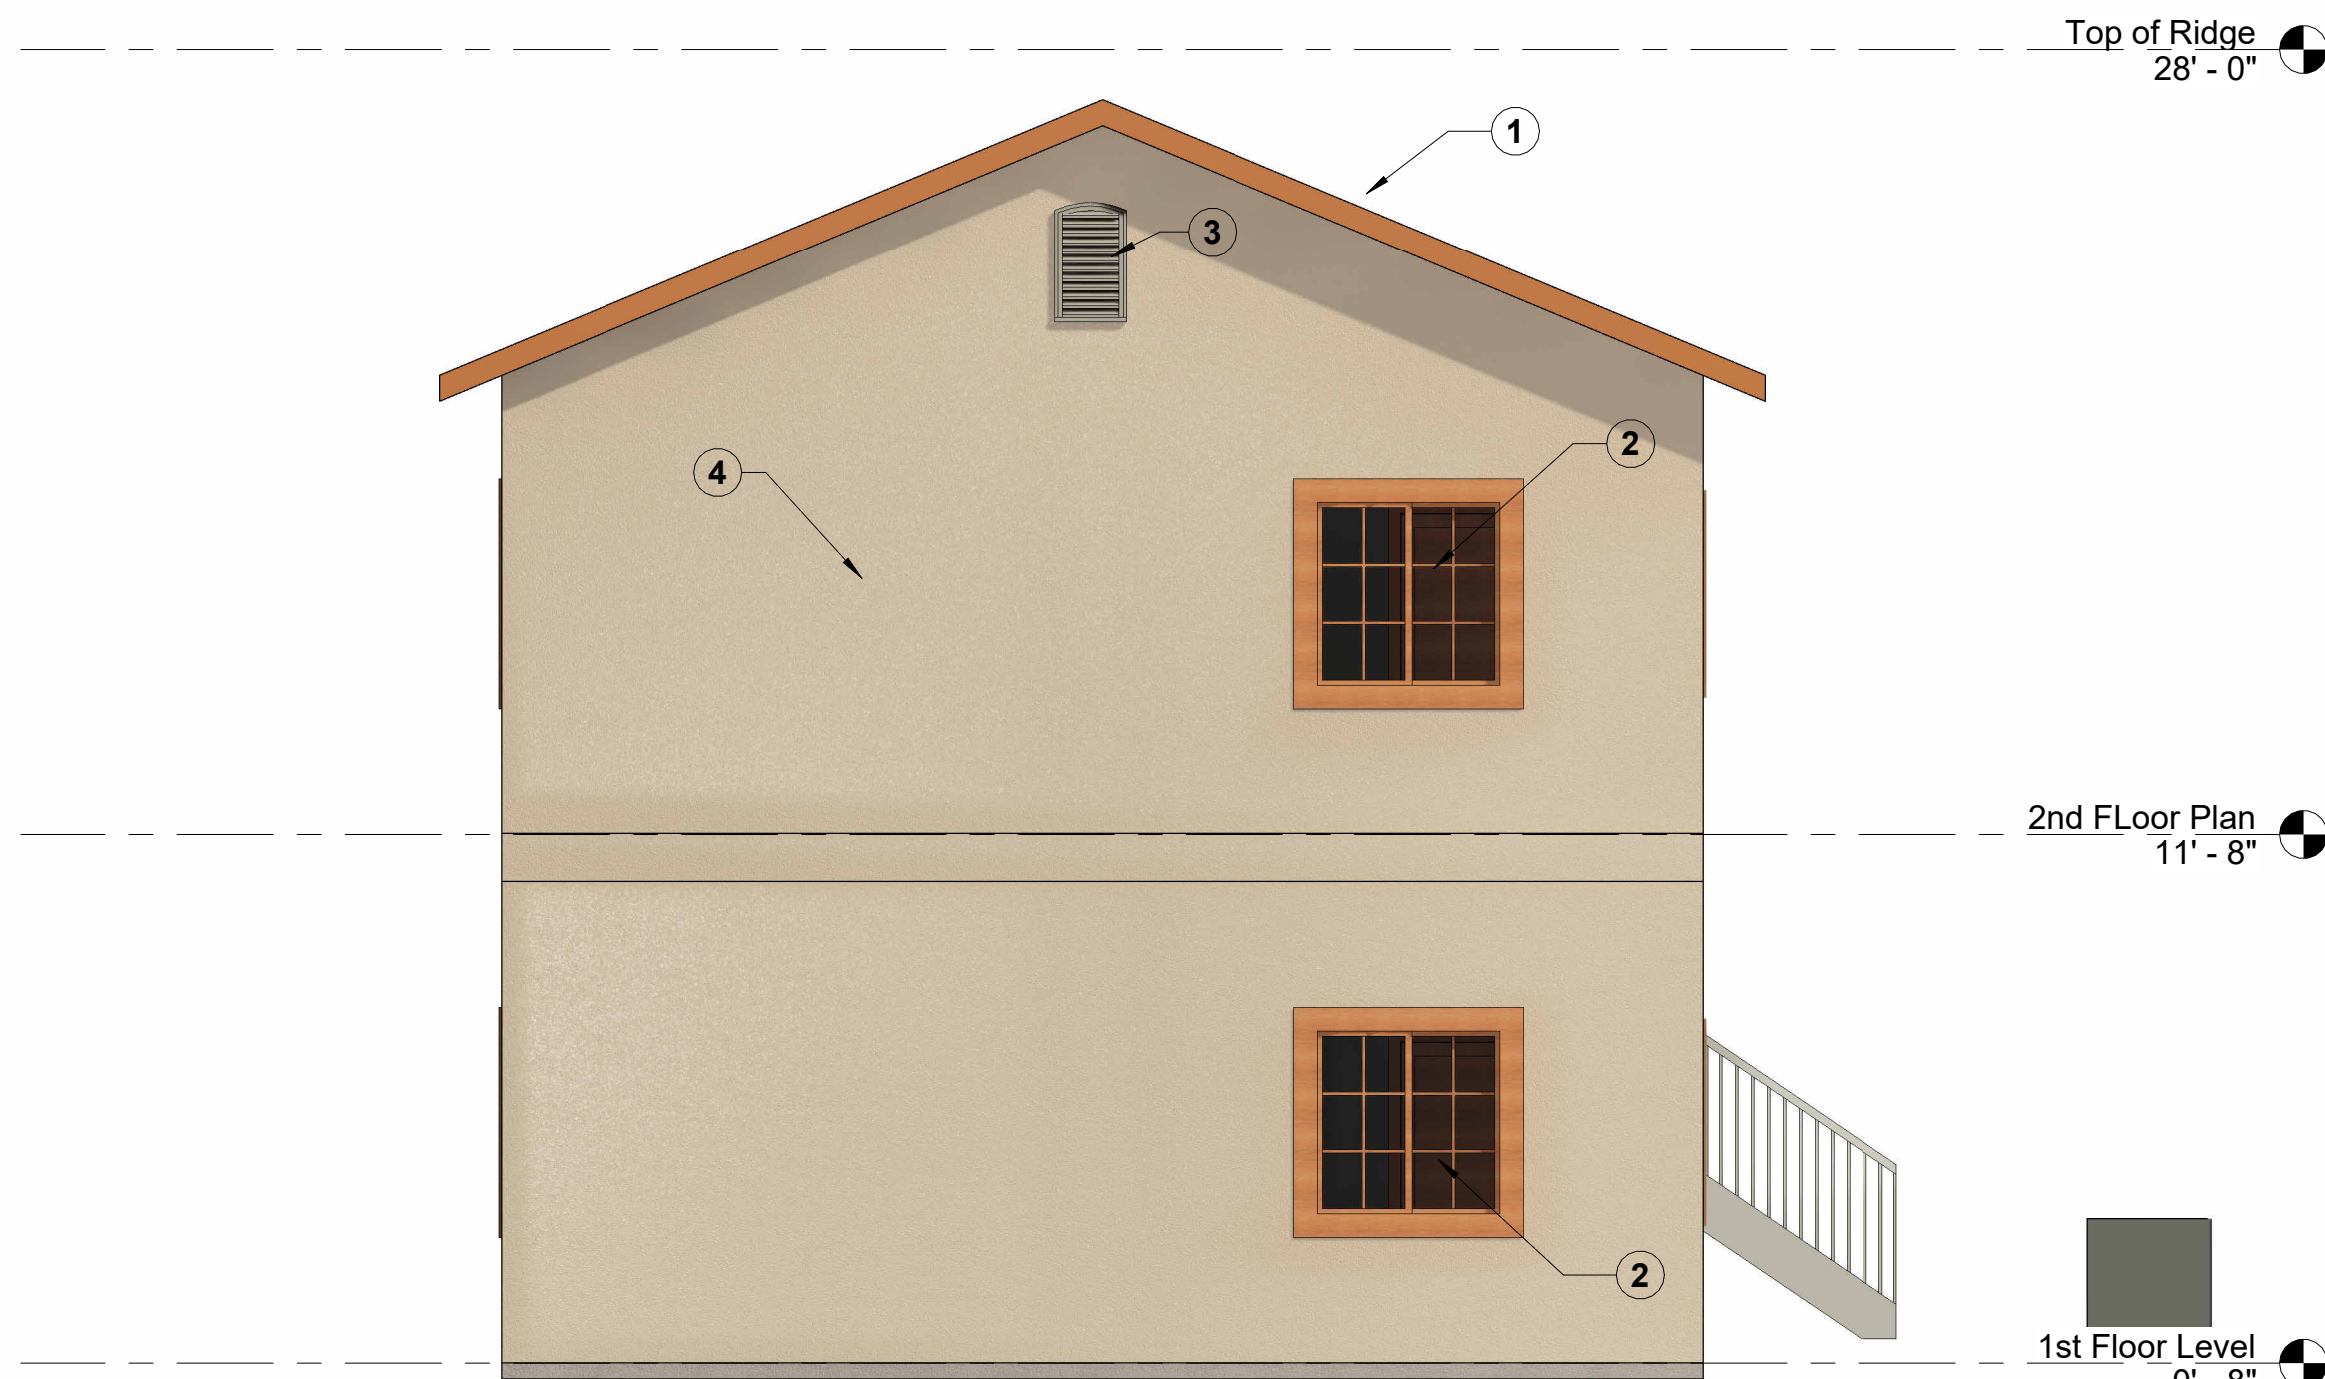

**4** ADU - East Elevation

1/4" = 1'-0"