




Revision Dates	
1	08.15.24
2	01.01.25
SHEET TITLE	
Foundation / Framing Plan	
Drawing Date	
08.24.26	
Check By	
-	
Drawn By	
FRANCIS N.	
Scale	
1/4" = 1'-0"	
Job Number	
081623	
Sheet Number	

15" x 12" CONT. CONC. FOOTING W/ (2) #4 CONT. TOP & BOTTOM,
TYP. AT ALL EXTERIOR WALLS - FOUNDATION PER DETAIL ON SD1
4" MIN. CONC. SLAB ON GRADE OVER 6 MIL VAPOR BARRIER
OVER 4" SAND - #4 @ 18" O.C. EACH WAY

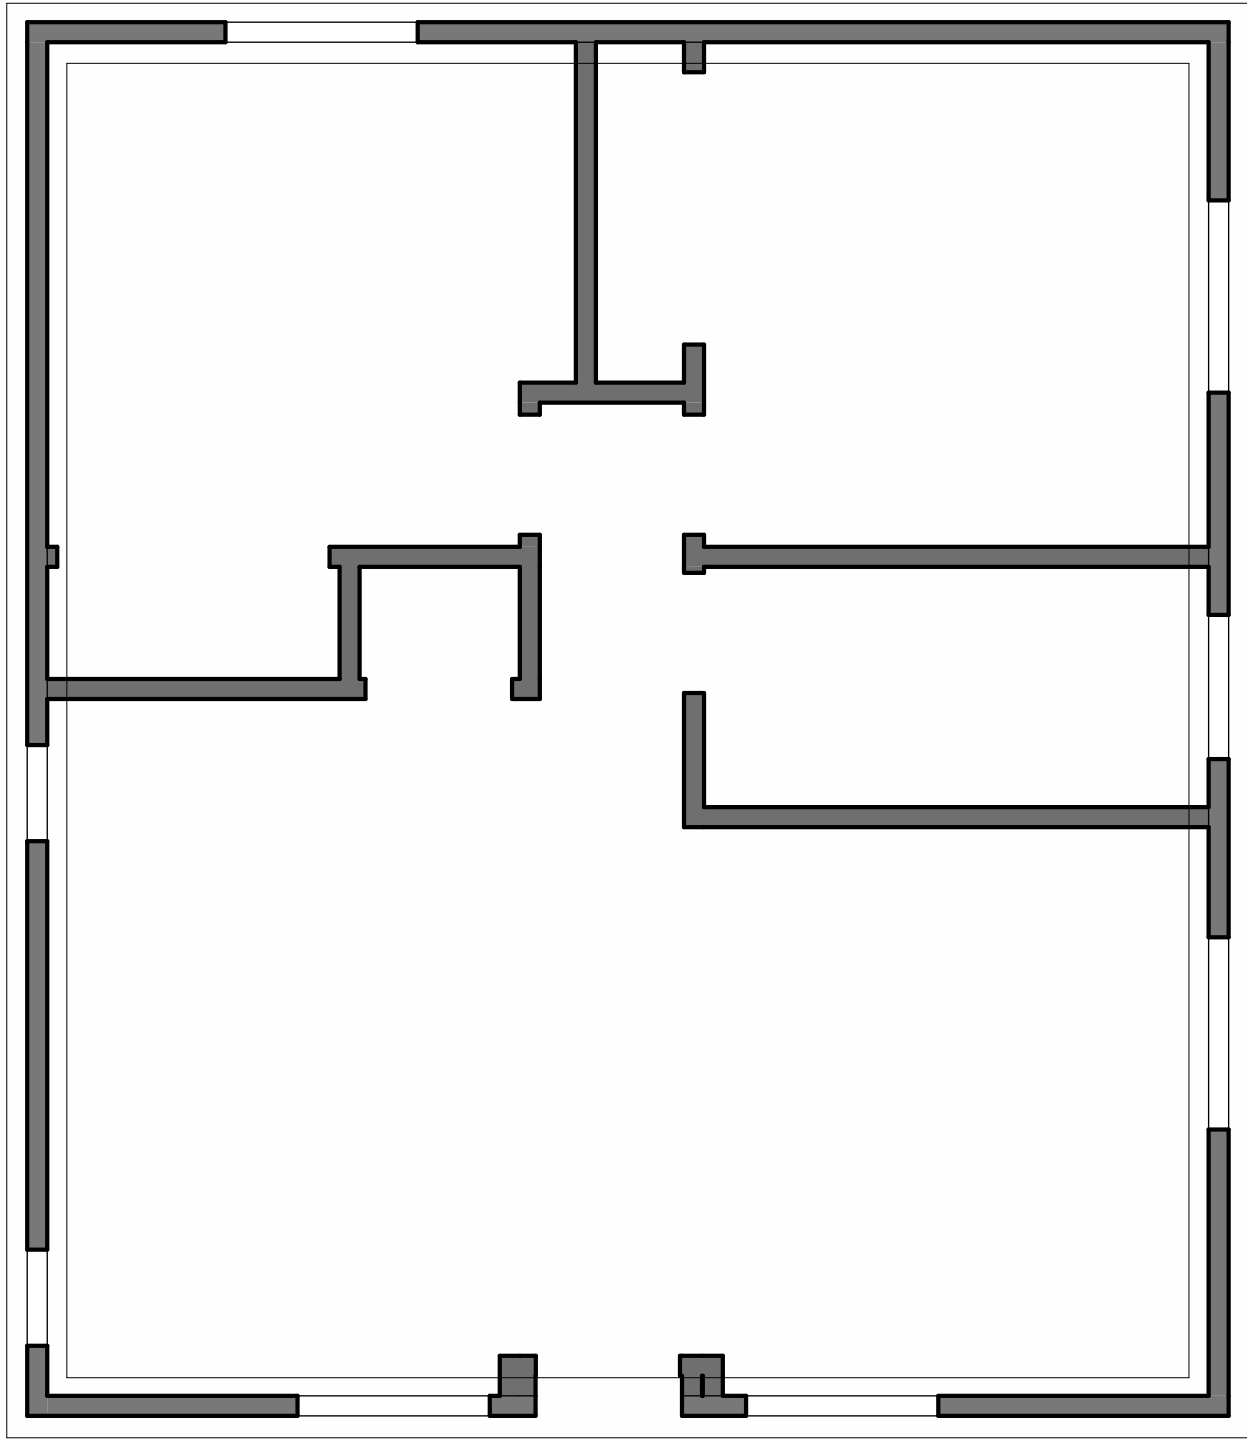


1

ADU - Foundation Plan

1/4" = 1'-0"

2x10 D.F. #2 FLOOR JOISTS @ 16" O.C.
SPAN AS SHOWN - SEE DETAIL ON SD1
BEARING WALL BELOW AT MID-SPAN

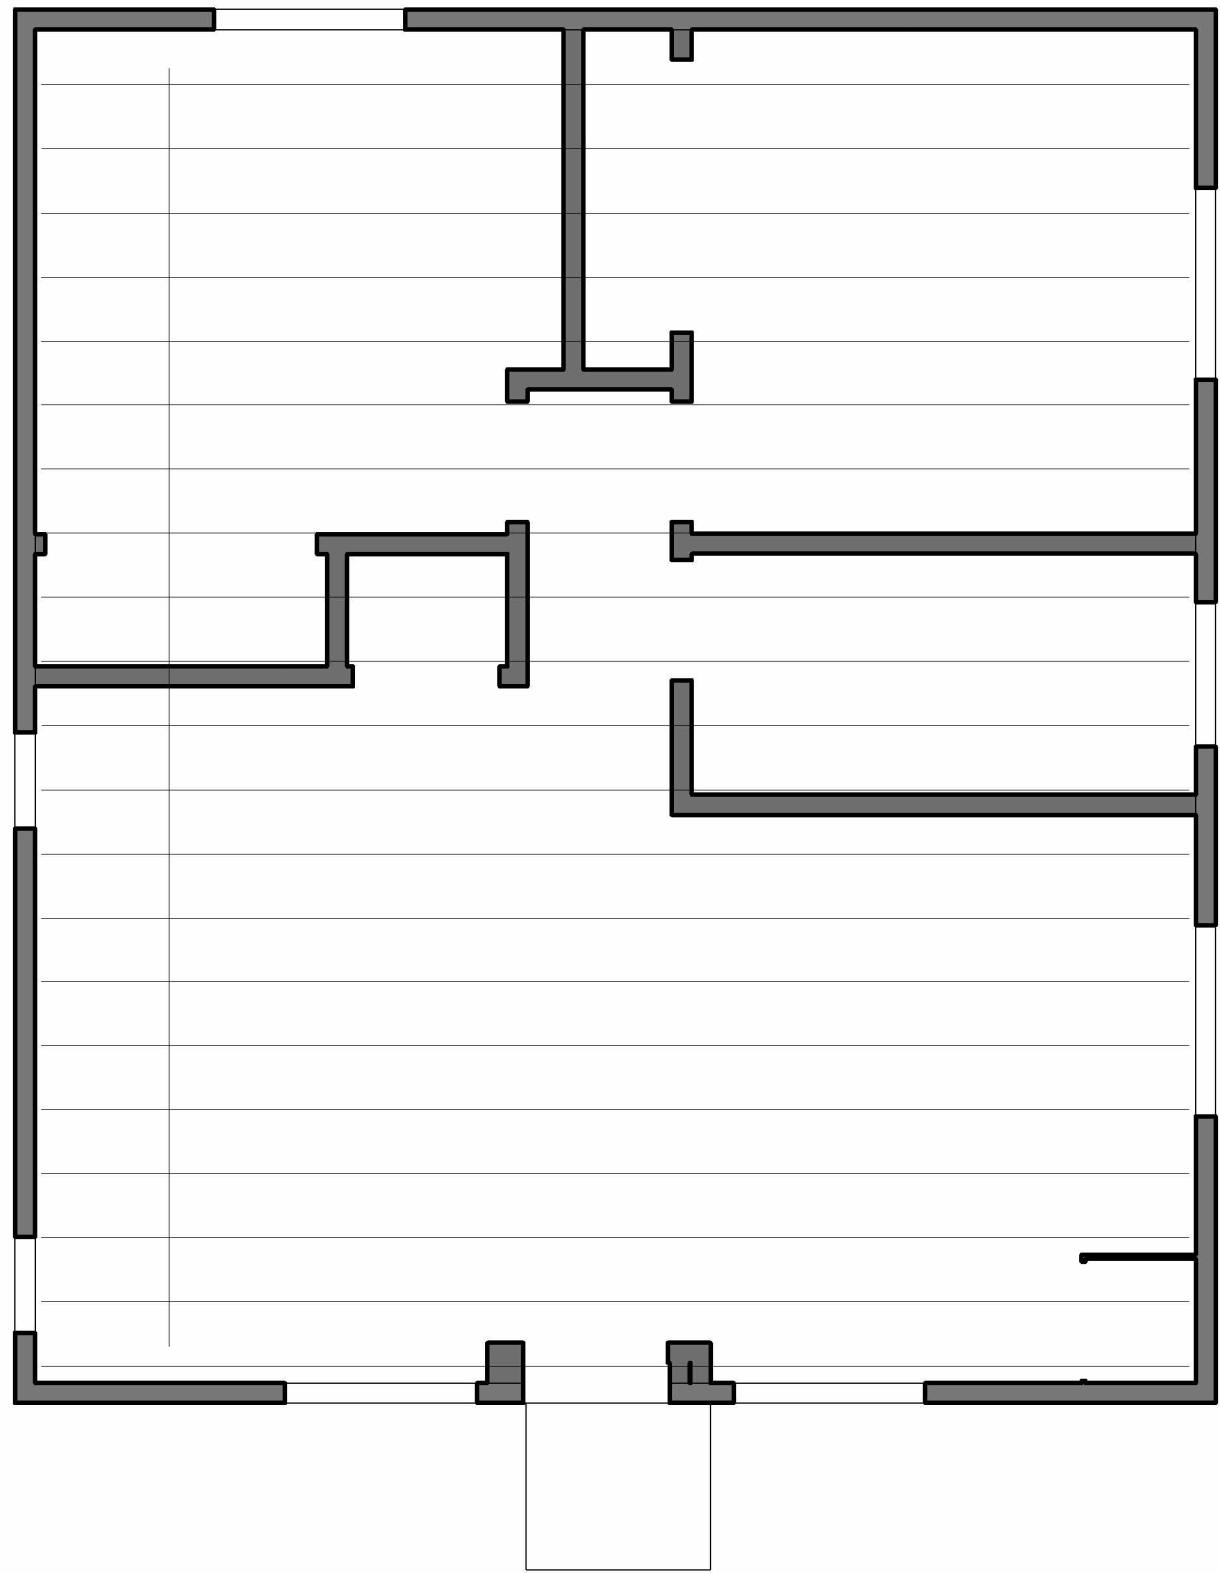

2

ADU - 2nd Floor Framing Plan

1/4" = 1'-0"

SHEAR WALL SCHEDULE										
NO.	SHEATING	EDGE NAILING	FEILD NAILING	FRAMING MEMBER	CONNECTION AT TOP PLATE	FOUNDATION ANCHORAGE	SILL PLATE NAILING TO WOOD FLOOR	CAPACITY (plf)	POST-HOL DOWN	SIMPSON HOLDOWN
1	23/32 OSB	8d @ 6"	8d @ 12"	2x	A-35 @ 16"	5/8" ∅ @ 48"	16d @ 5"	260	4x4 OR (2) 2X4	HDU5