



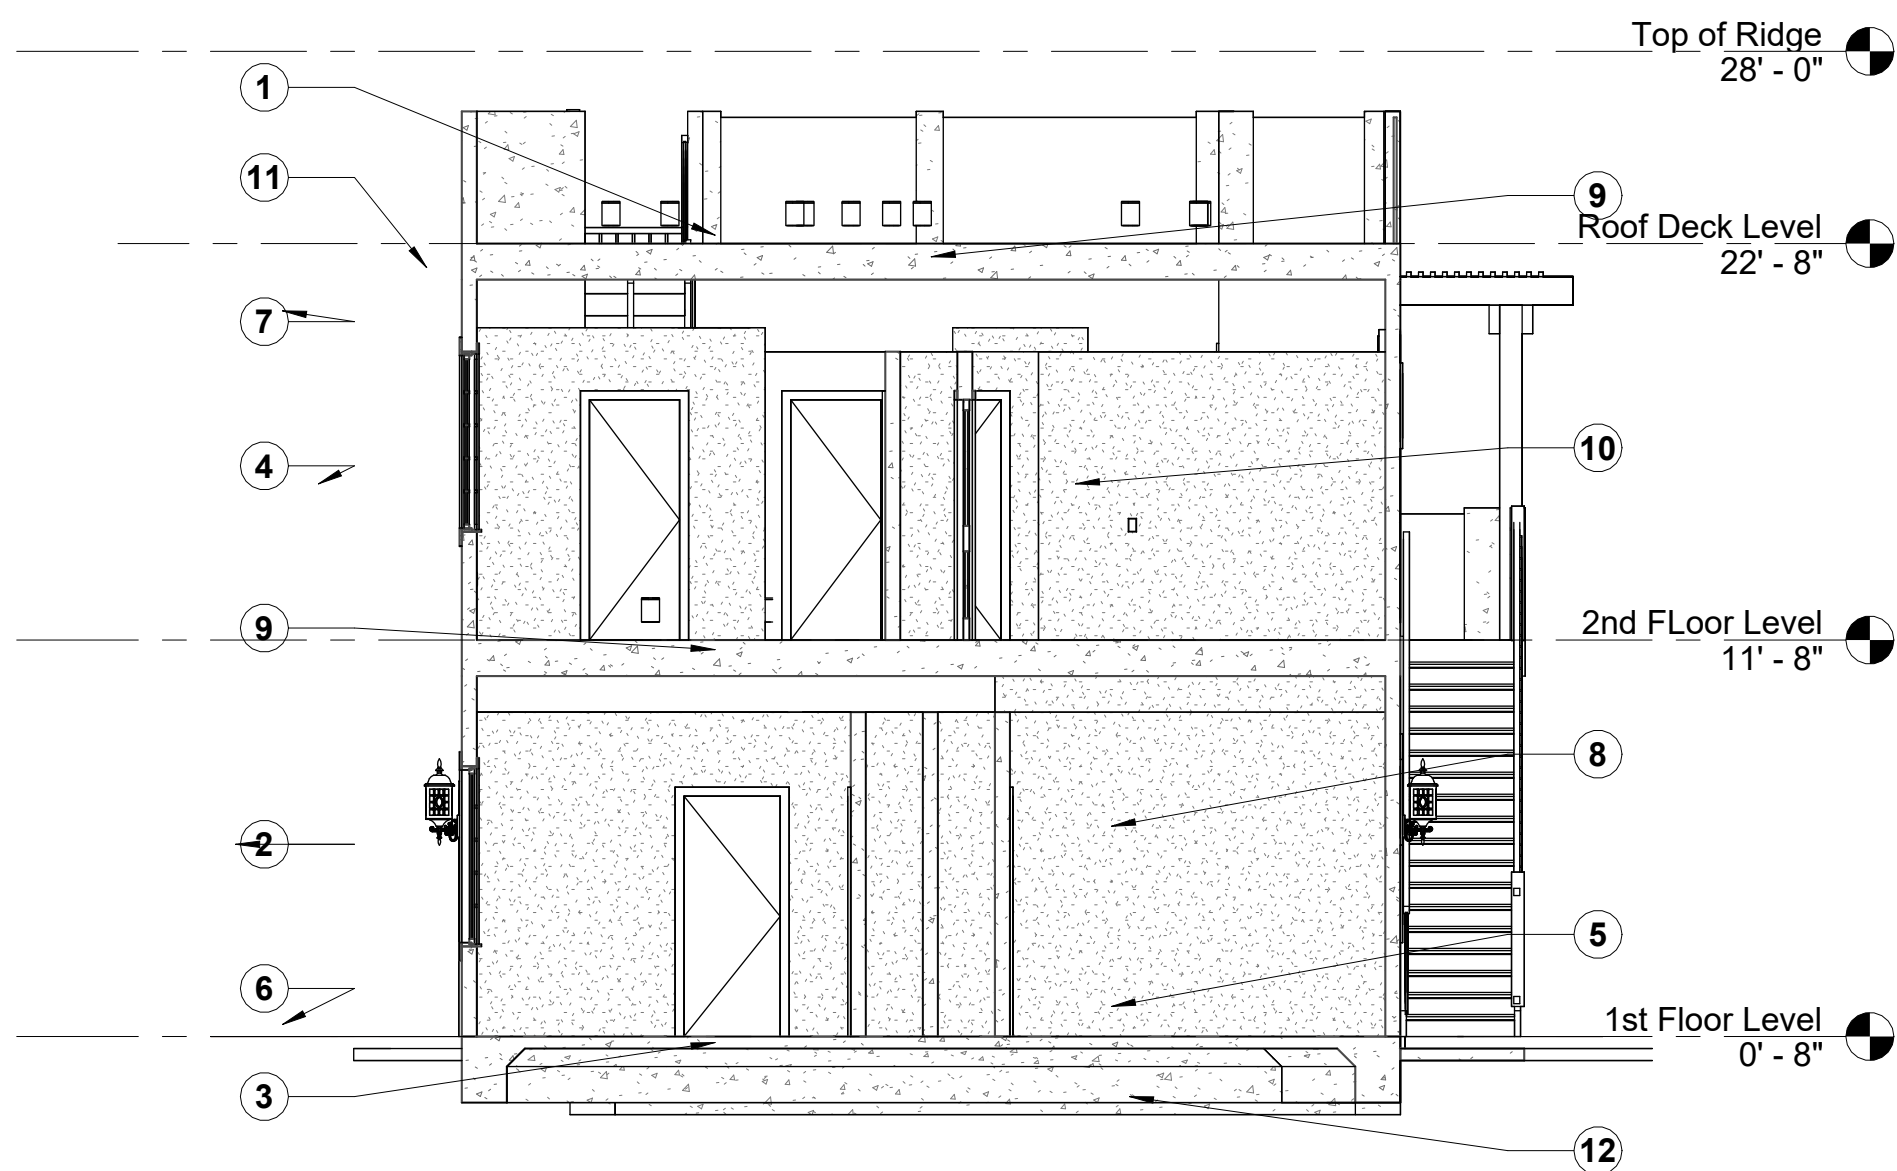

**1 Section 1**  
3/16" = 1'-0"

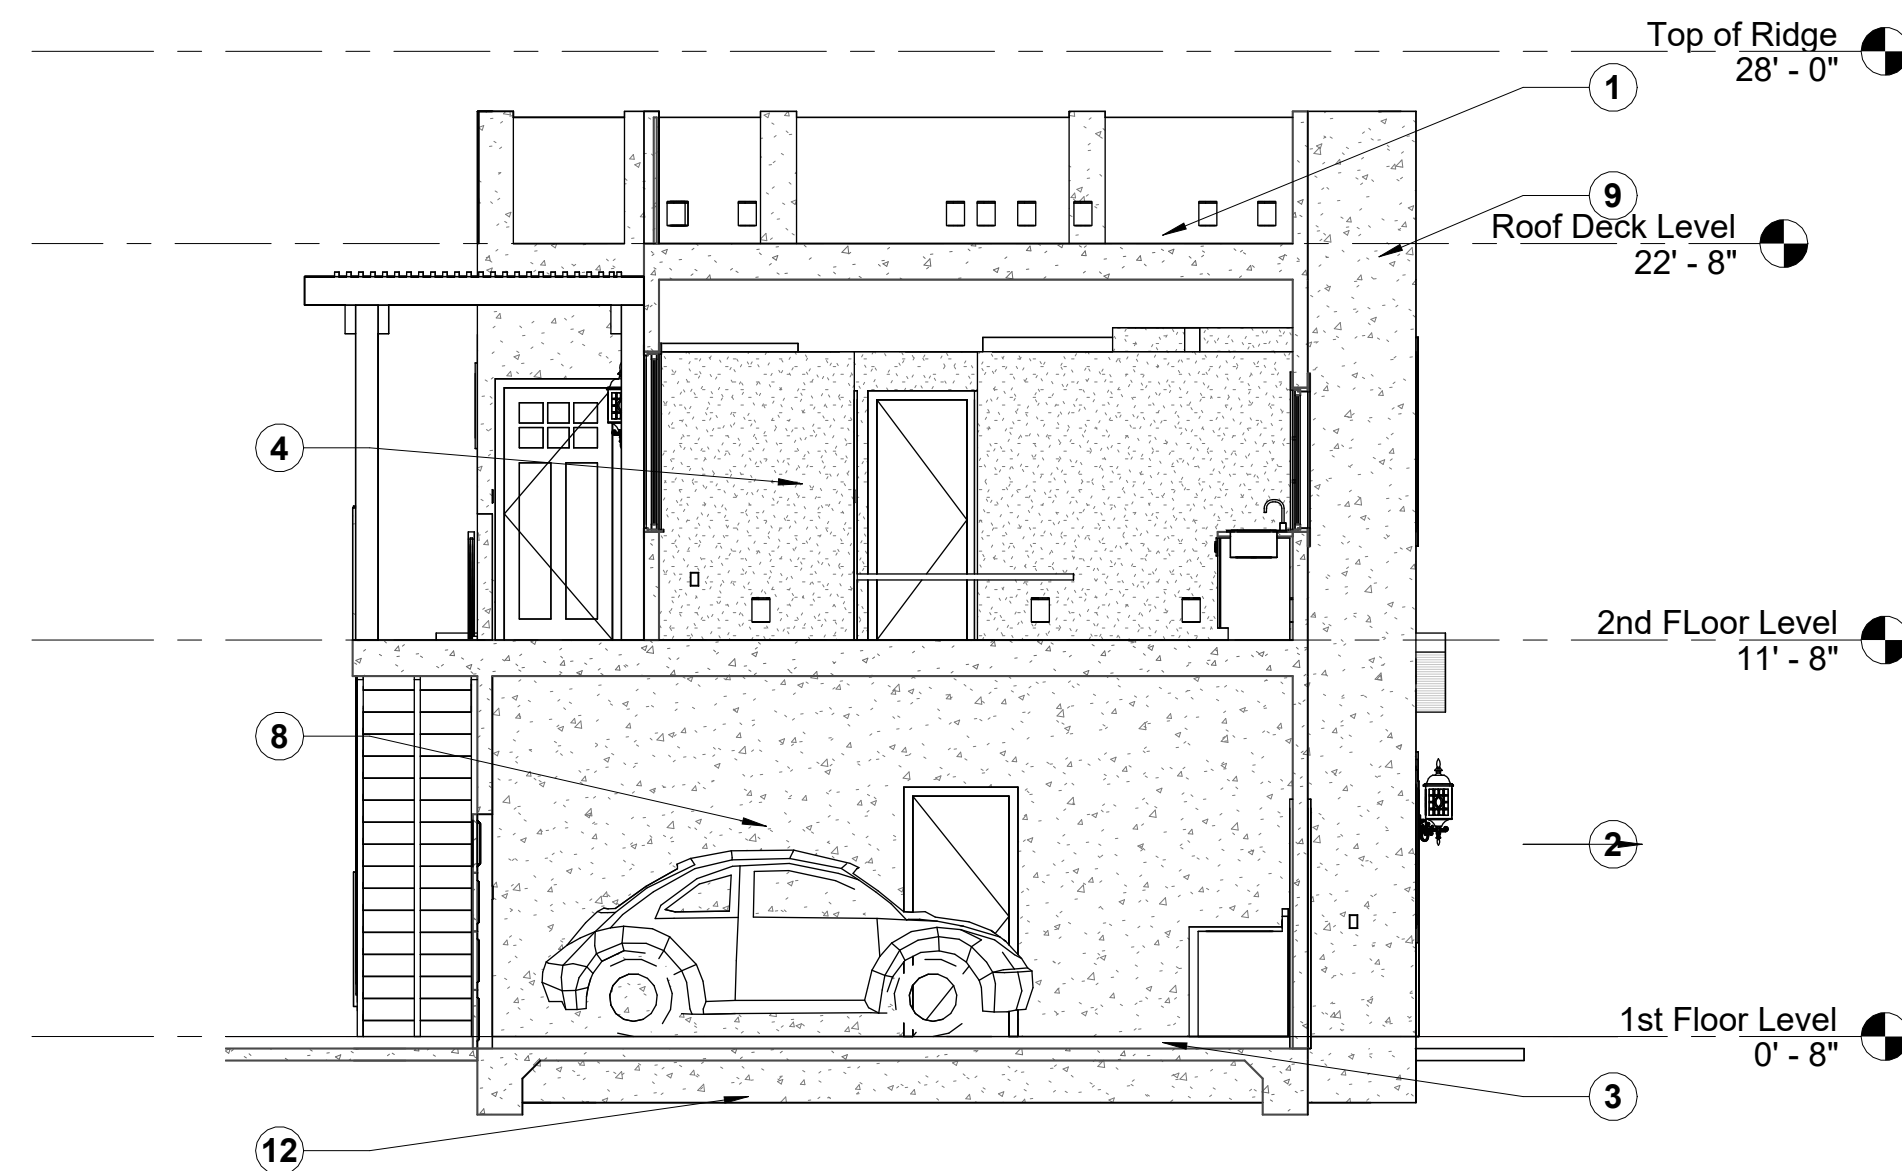

**2 Section 2**  
3/16" = 1'-0"


**KEYNOTES**

- 1 CLASS A ROOF DECK SYSTEM
- 2 STUCCO @ EXTERIOR
- 3 4" MIN. CONC. SLAB ON GRADE
- 4 1/2" GYP. BD.
- 5 WEEP SCREED
- 6 PRESSURE TREATED BOTTOM PLATE
- 7 DOUBLE TOP PLATE

- 8 2x4 STUDS @ 16" O.C.
- 9 ROOF/FLR JOISTS PER PLAN
- 10 R-15 BATT INSULATION
- 11 R-30 BATT INSULATION
- 12 FOOTING PER DETAIL ON SD1



**3 Section 3**  
3/16" = 1'-0"

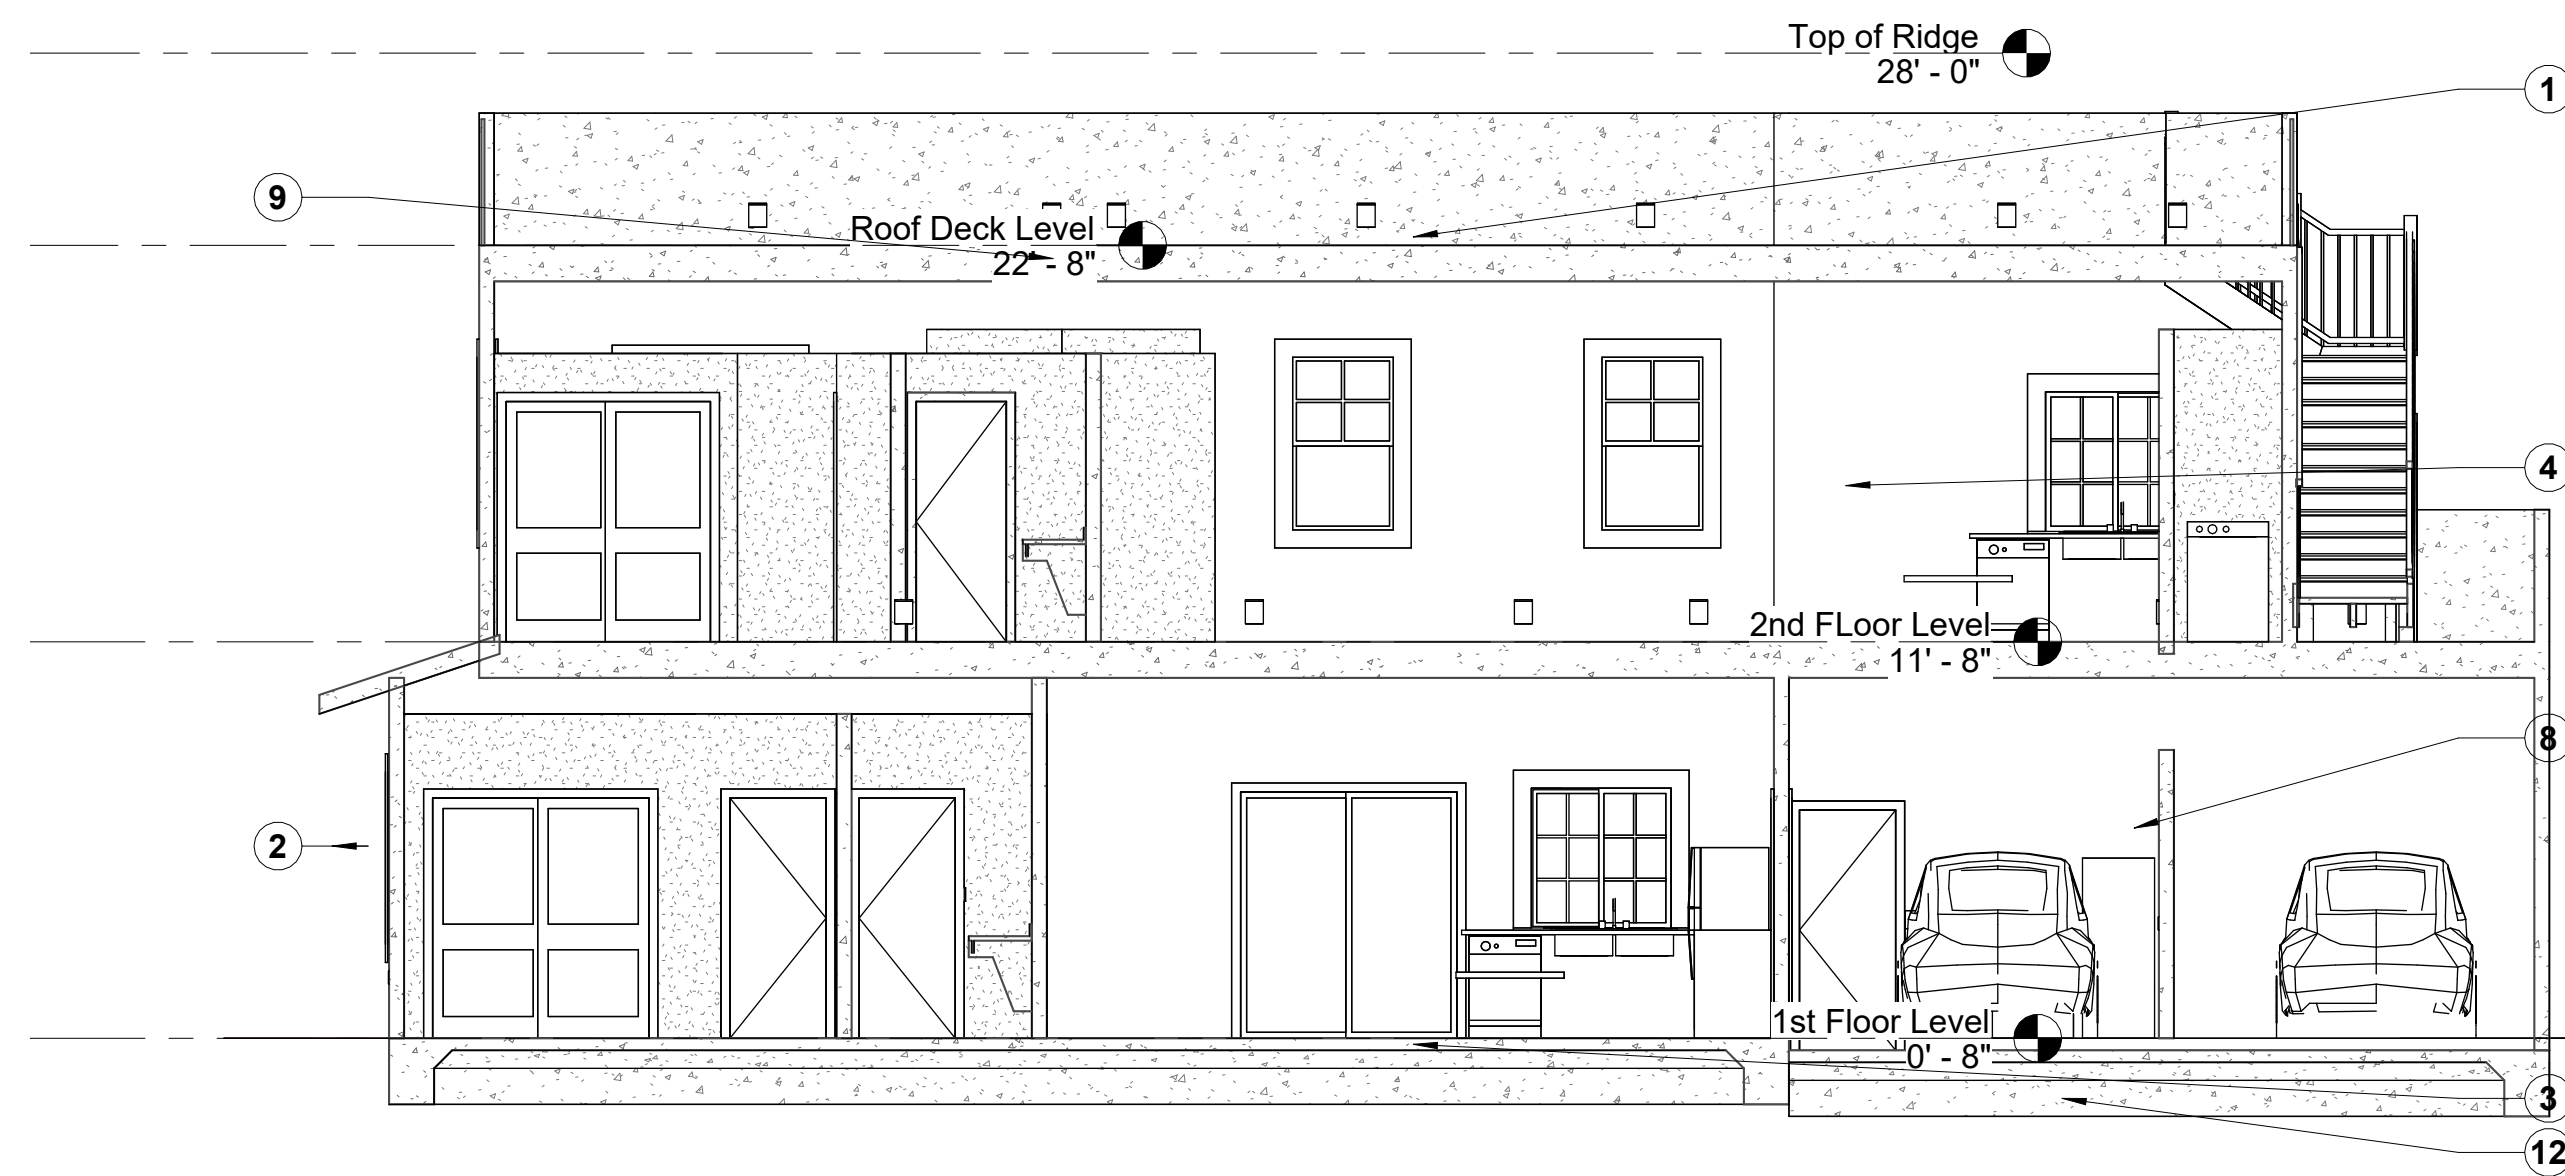

**4 Section 4**  
3/16" = 1'-0"