



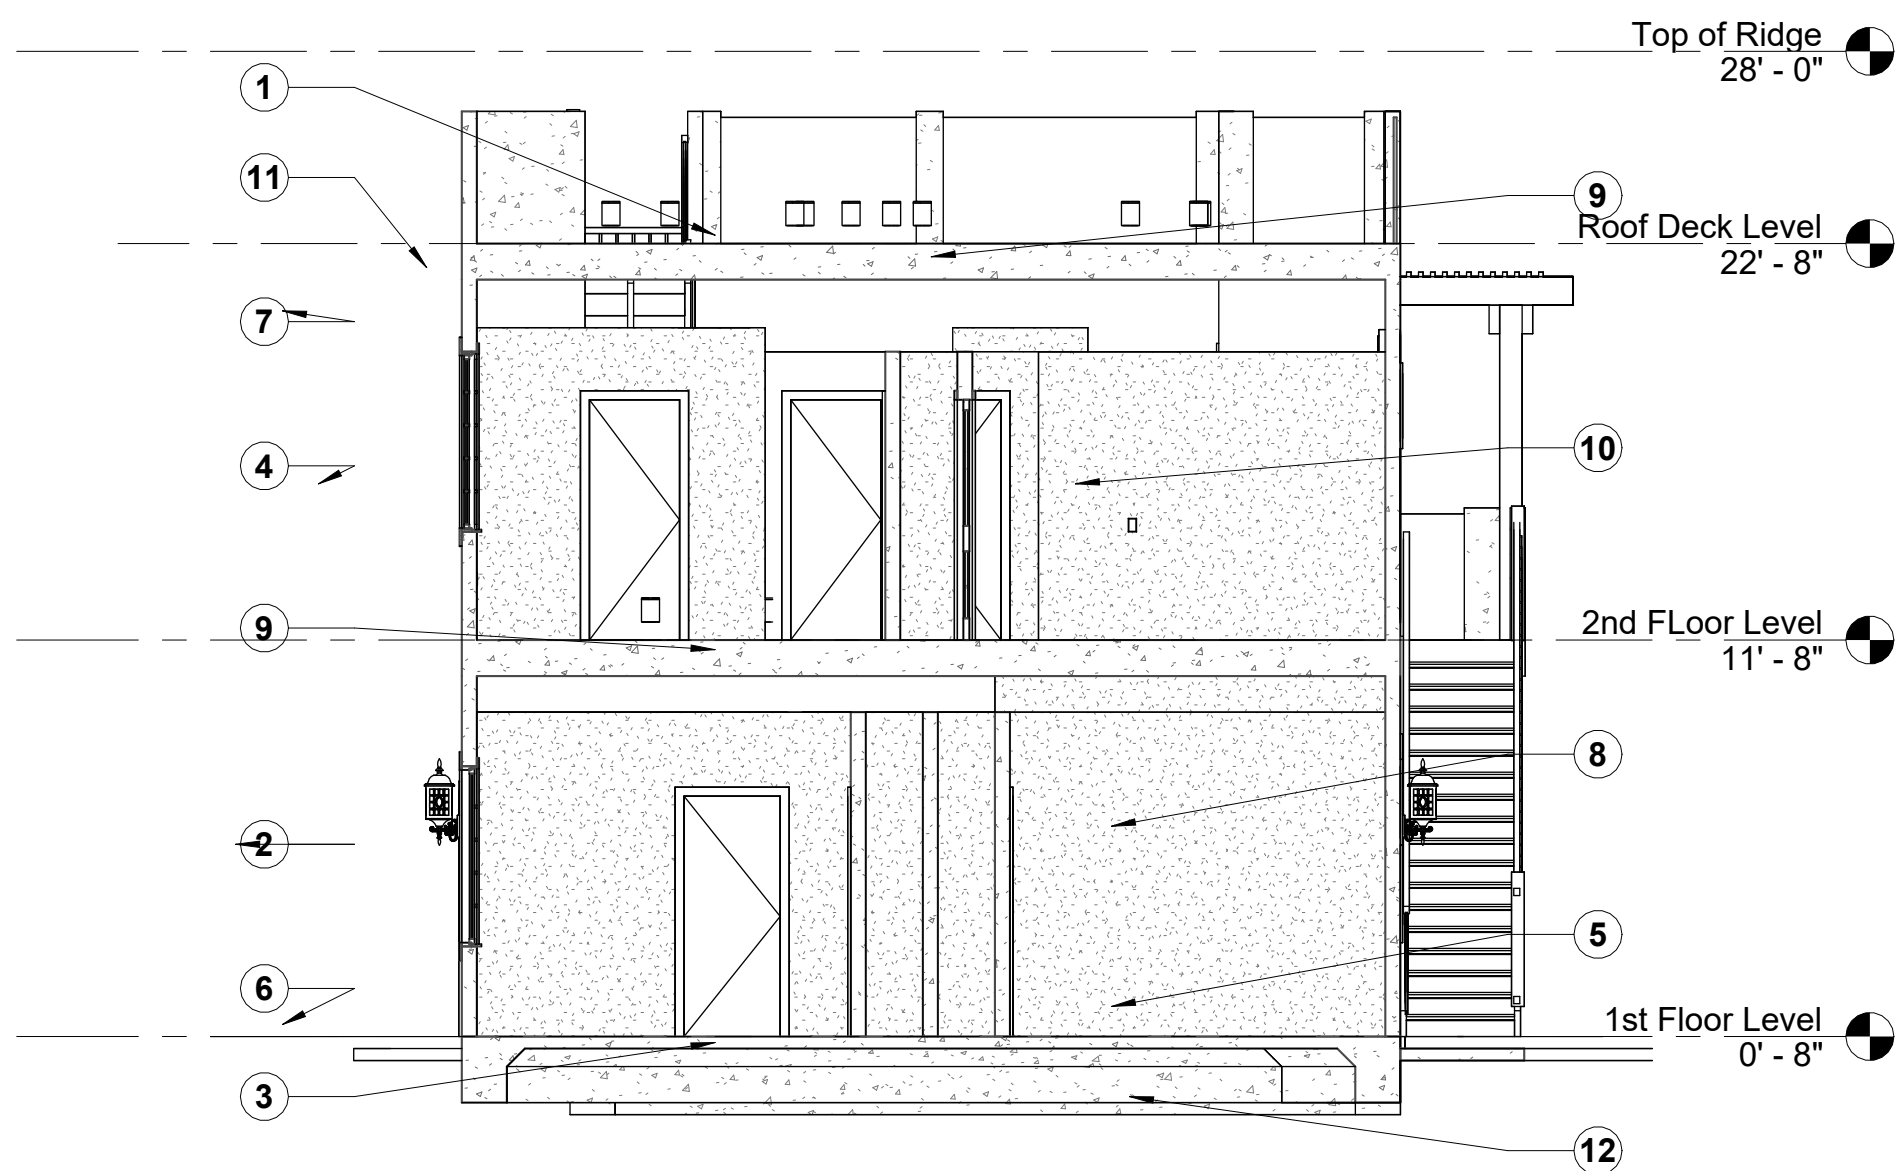

1 *Section 1*
3/16" = 1'-0"

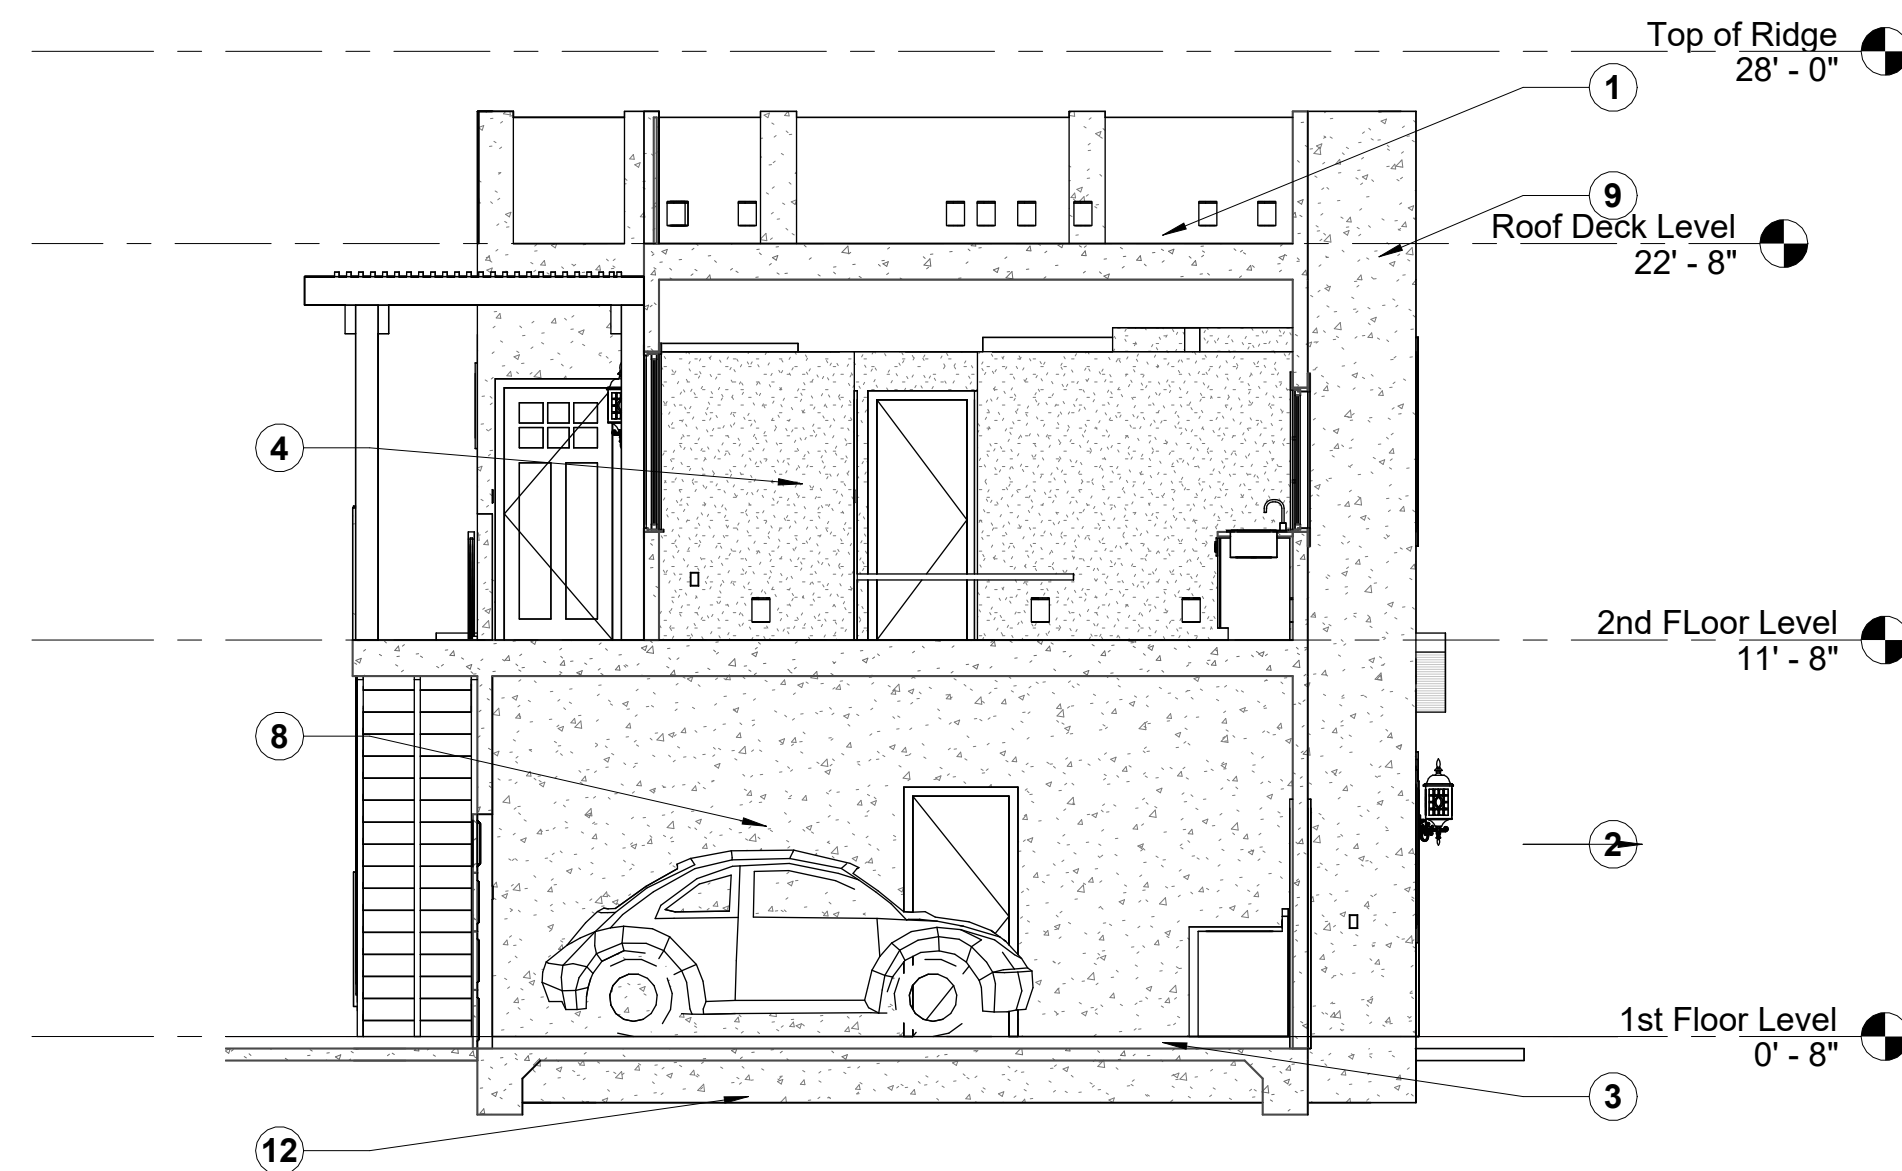

2 *Section 2*
3/16" = 1'-0"


KEYNOTES

- 1 CLASS A ROOF DECK SYSTEM
- 2 STUCCO @ EXTERIOR
- 3 4" MIN. CONC. SLAB ON GRADE
- 4 1/2" GYP. BD.
- 5 WEEP SCREED
- 6 PRESSURE TREATED BOTTOM PLATE
- 7 DOUBLE TOP PLATE

- 8 2x4 STUDS @ 16" O.C.
- 9 ROOF/FLR JOISTS PER PLAN
- 10 R-15 BATT INSULATION
- 11 R-30 BATT INSULATION
- 12 FOOTING PER DETAIL ON SD1
- 13
- 14



3 *Section 3*
3/16" = 1'-0"

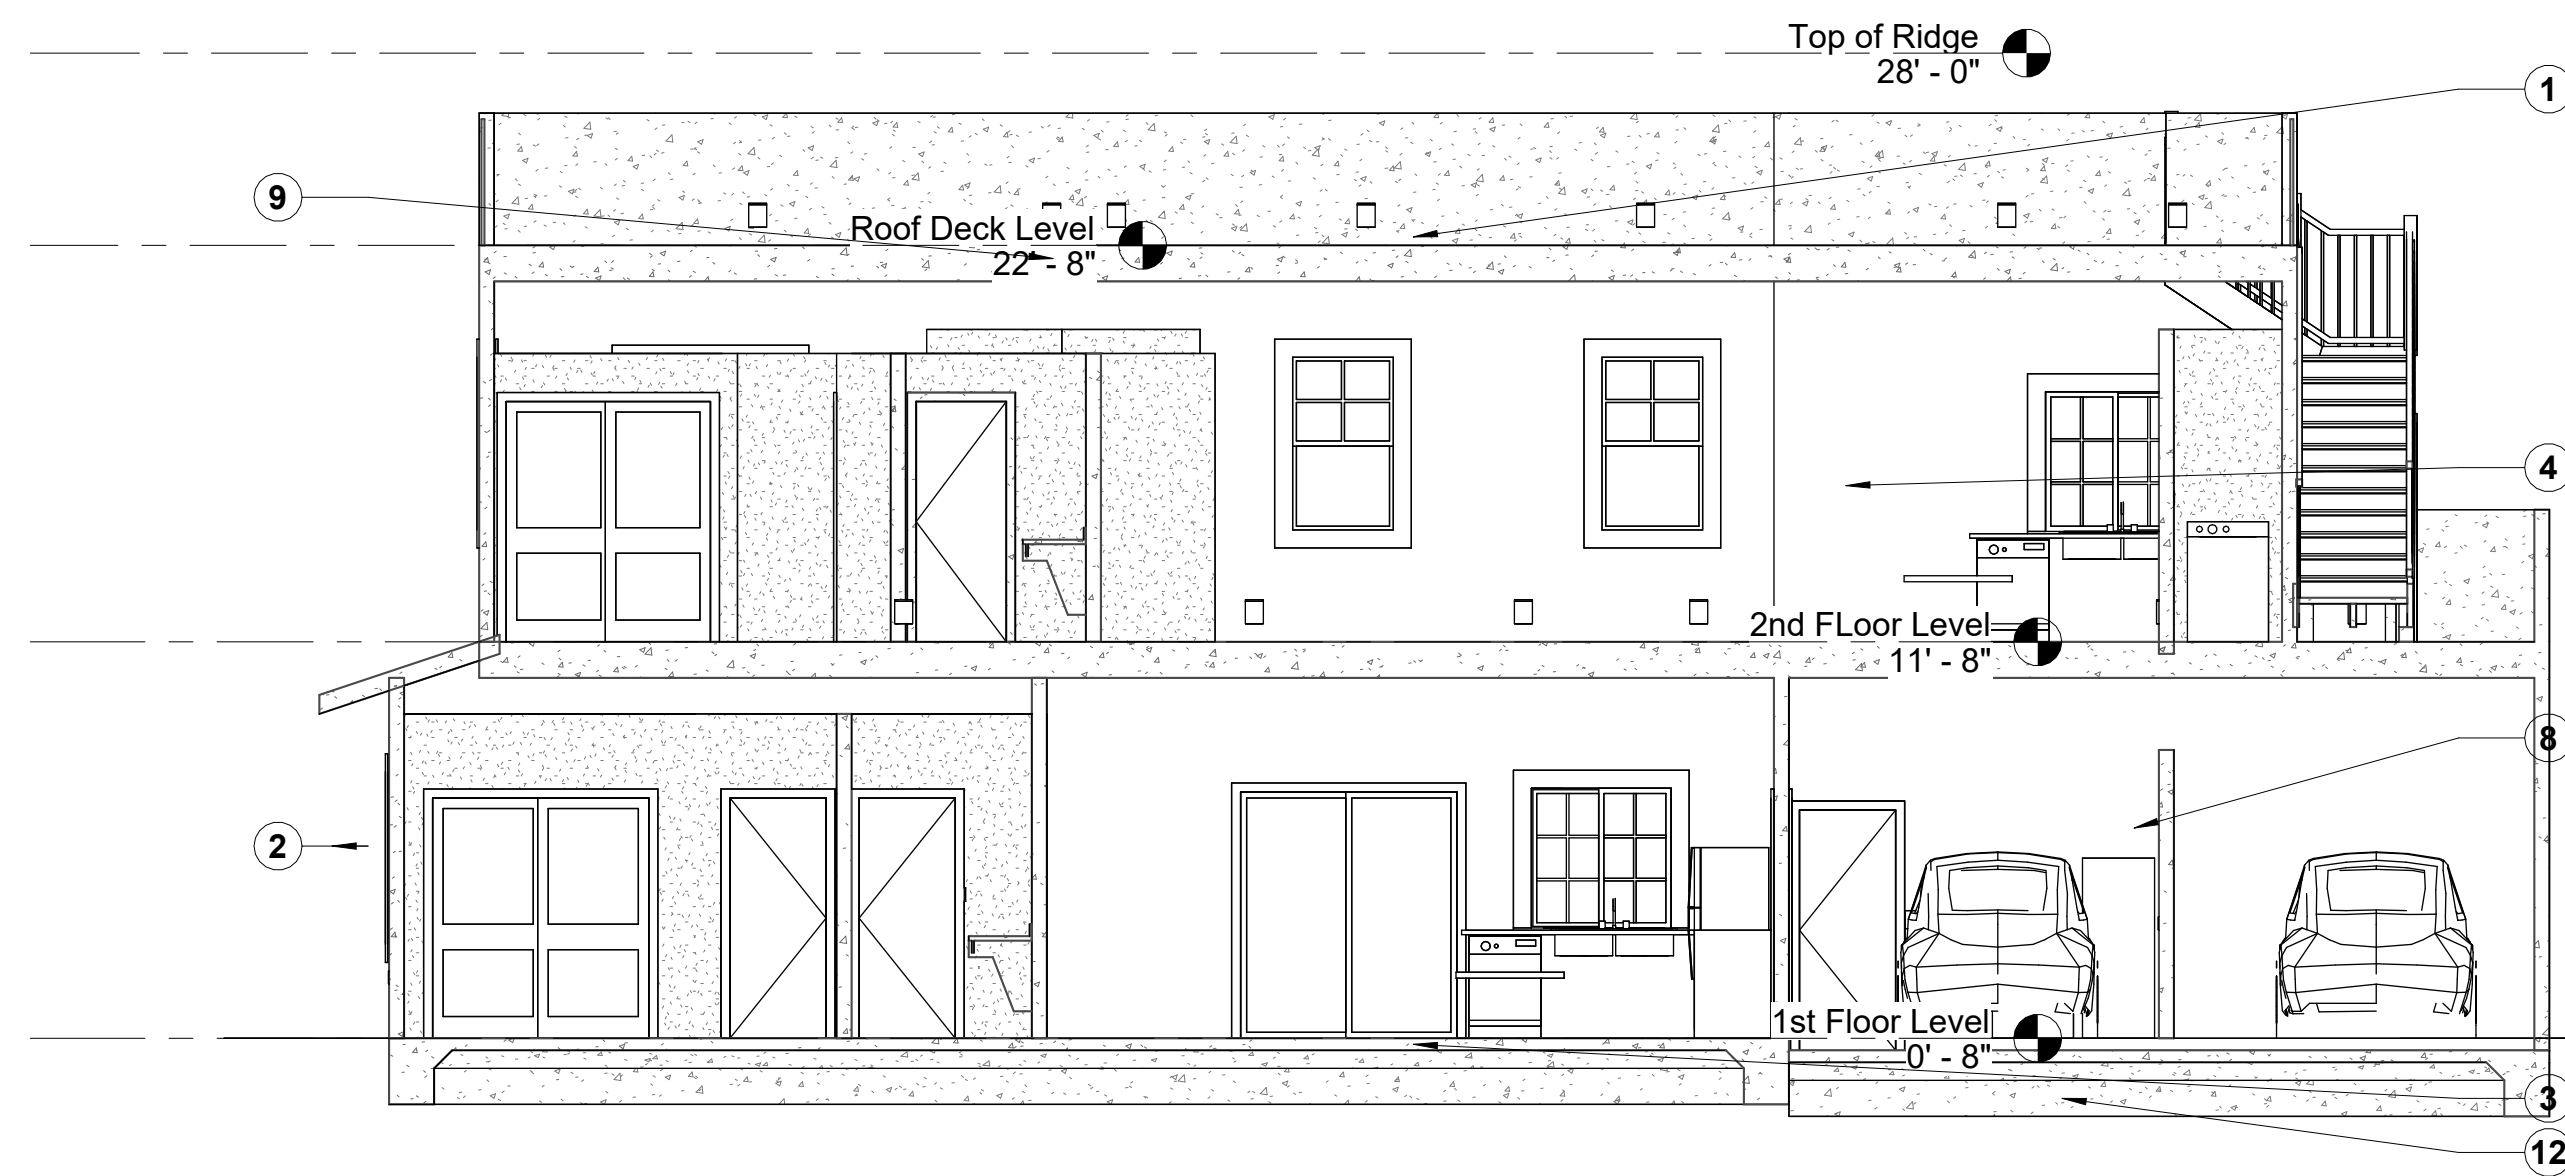

4 *Section 4*
3/16" = 1'-0"