



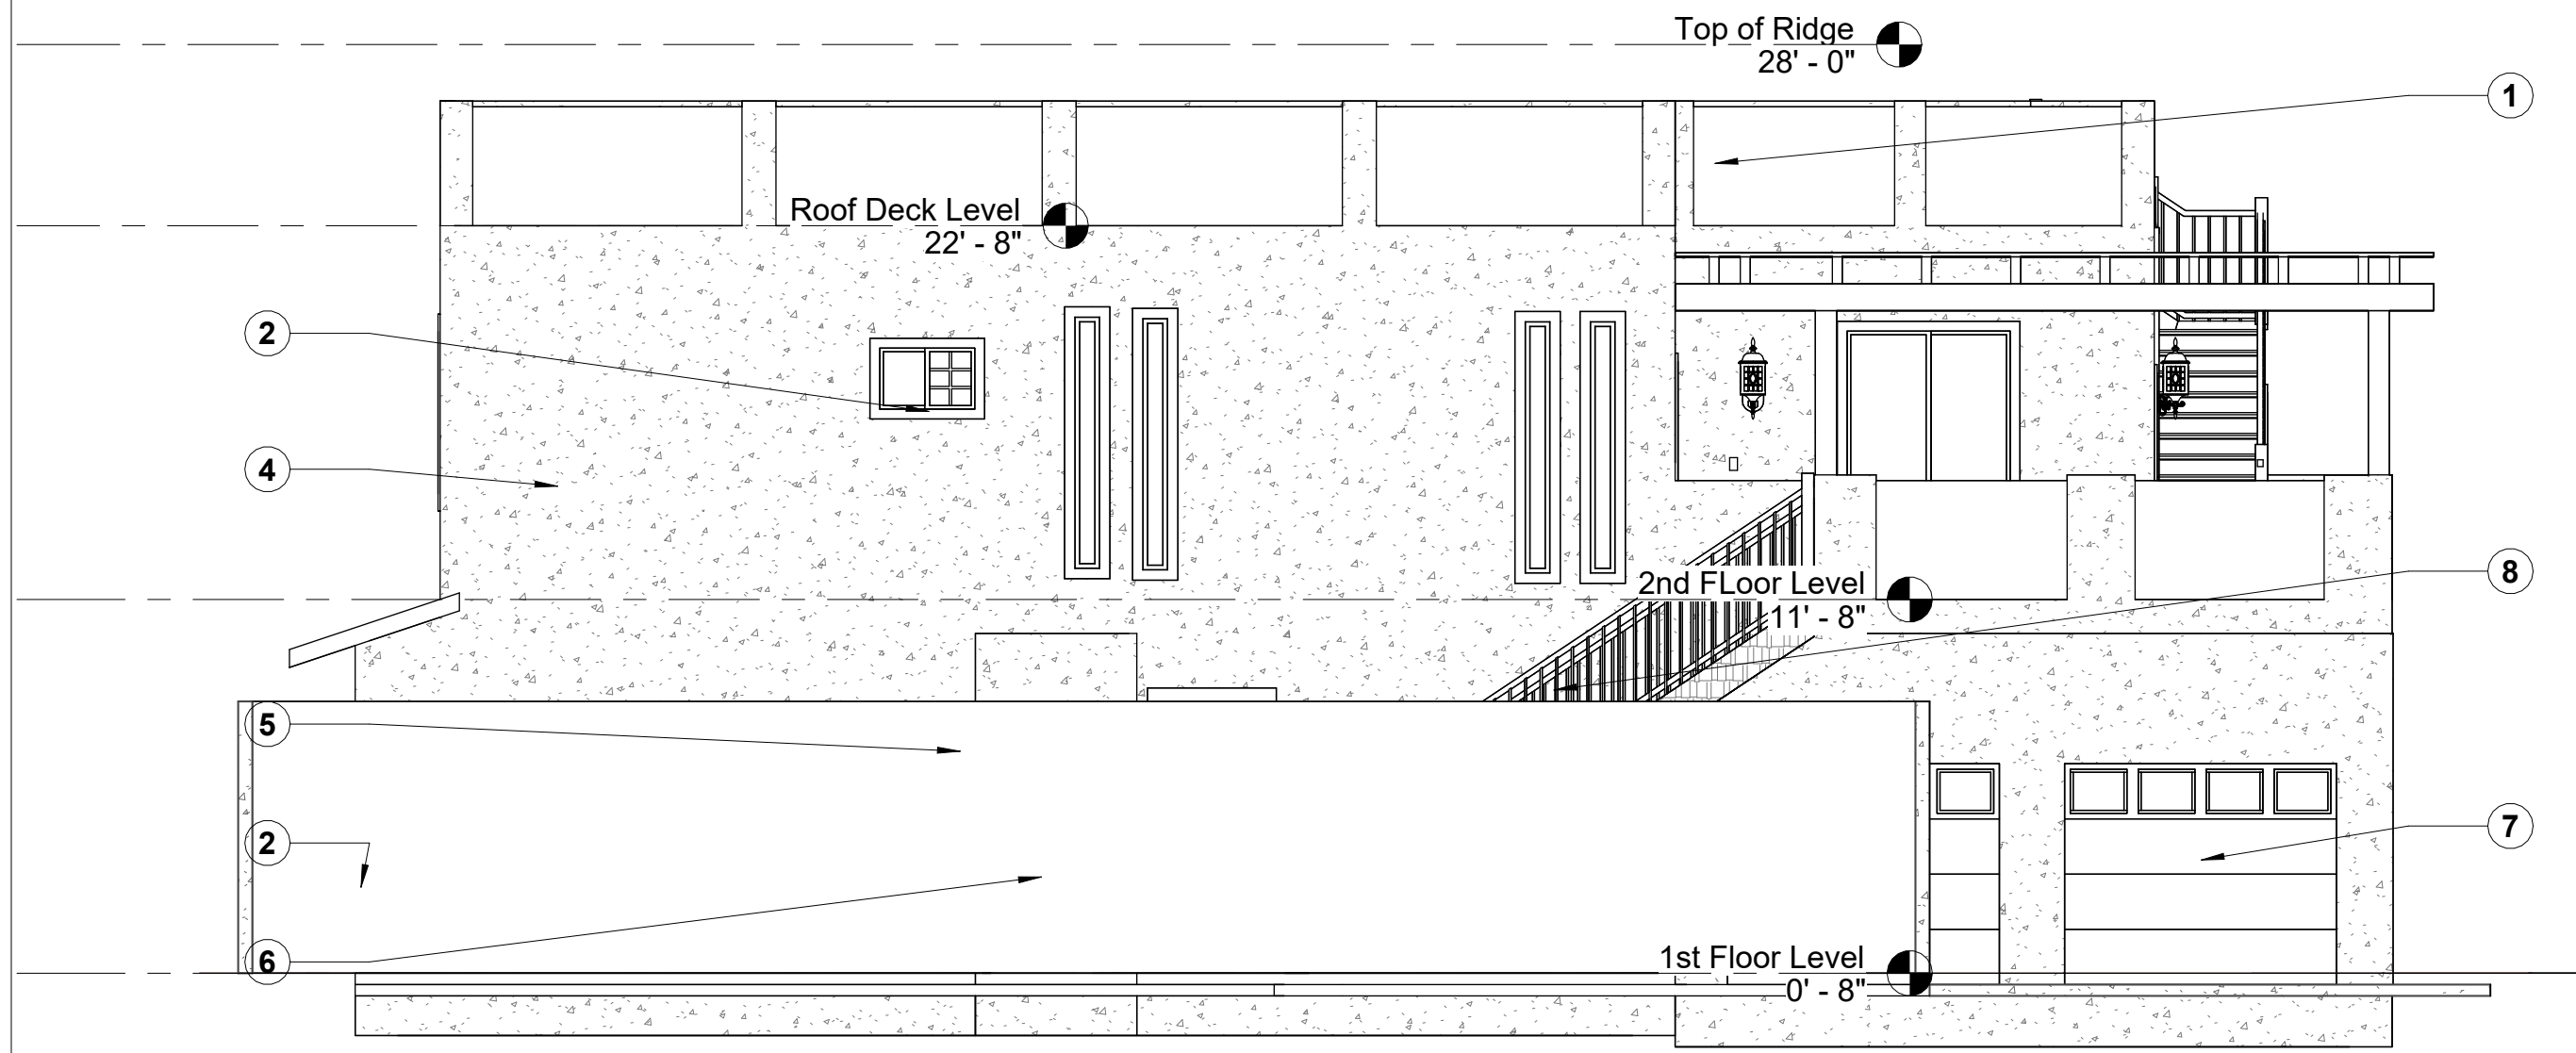


**1** *South Elev.*  
3/16" = 1'-0"

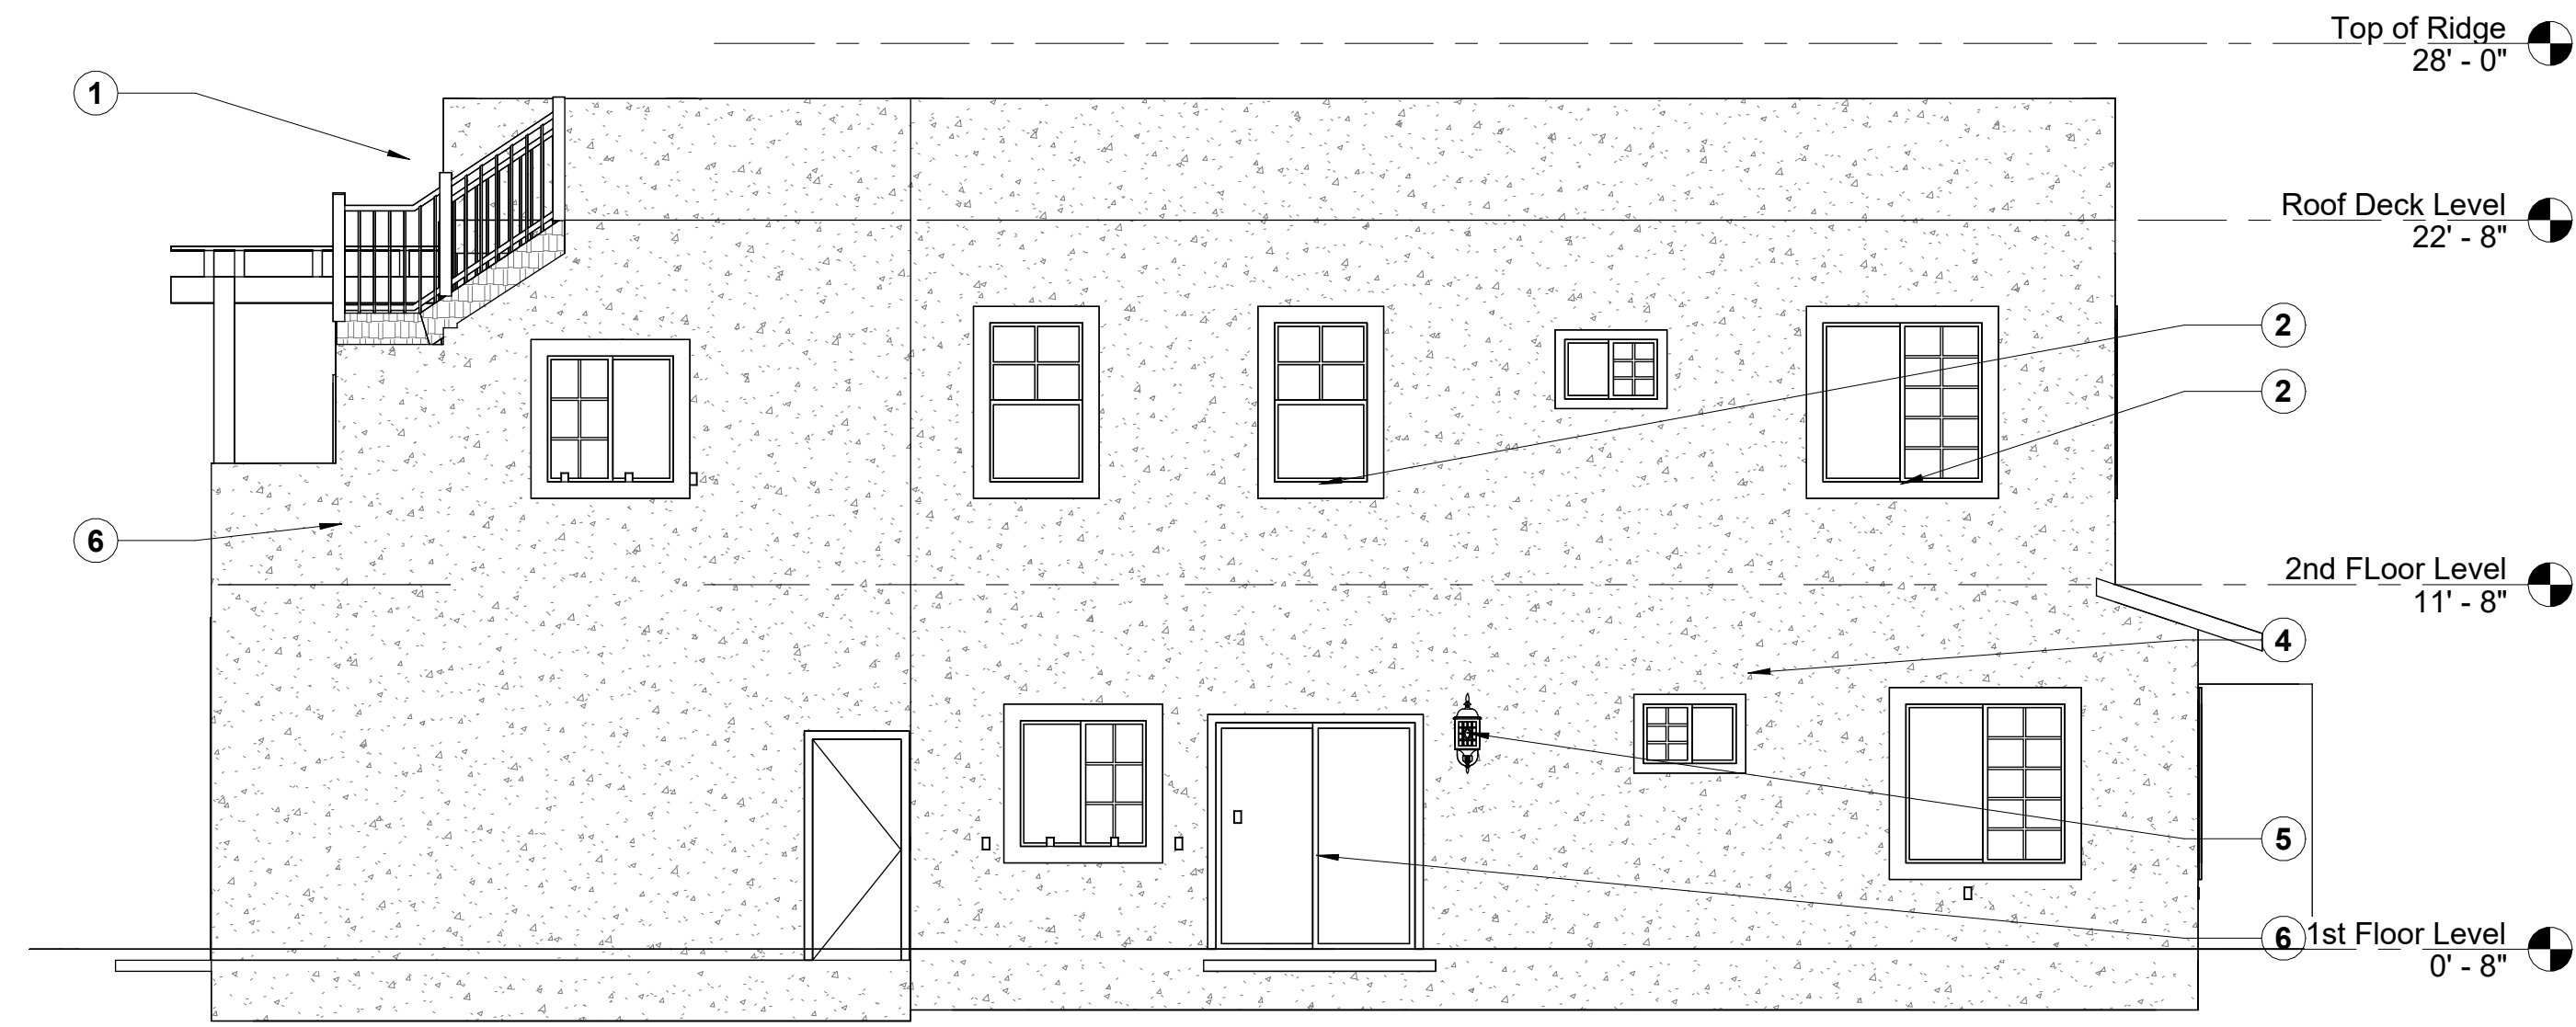

**2** *North Elev.*  
3/16" = 1'-0"



**3** *West Elev.*  
3/16" = 1'-0"

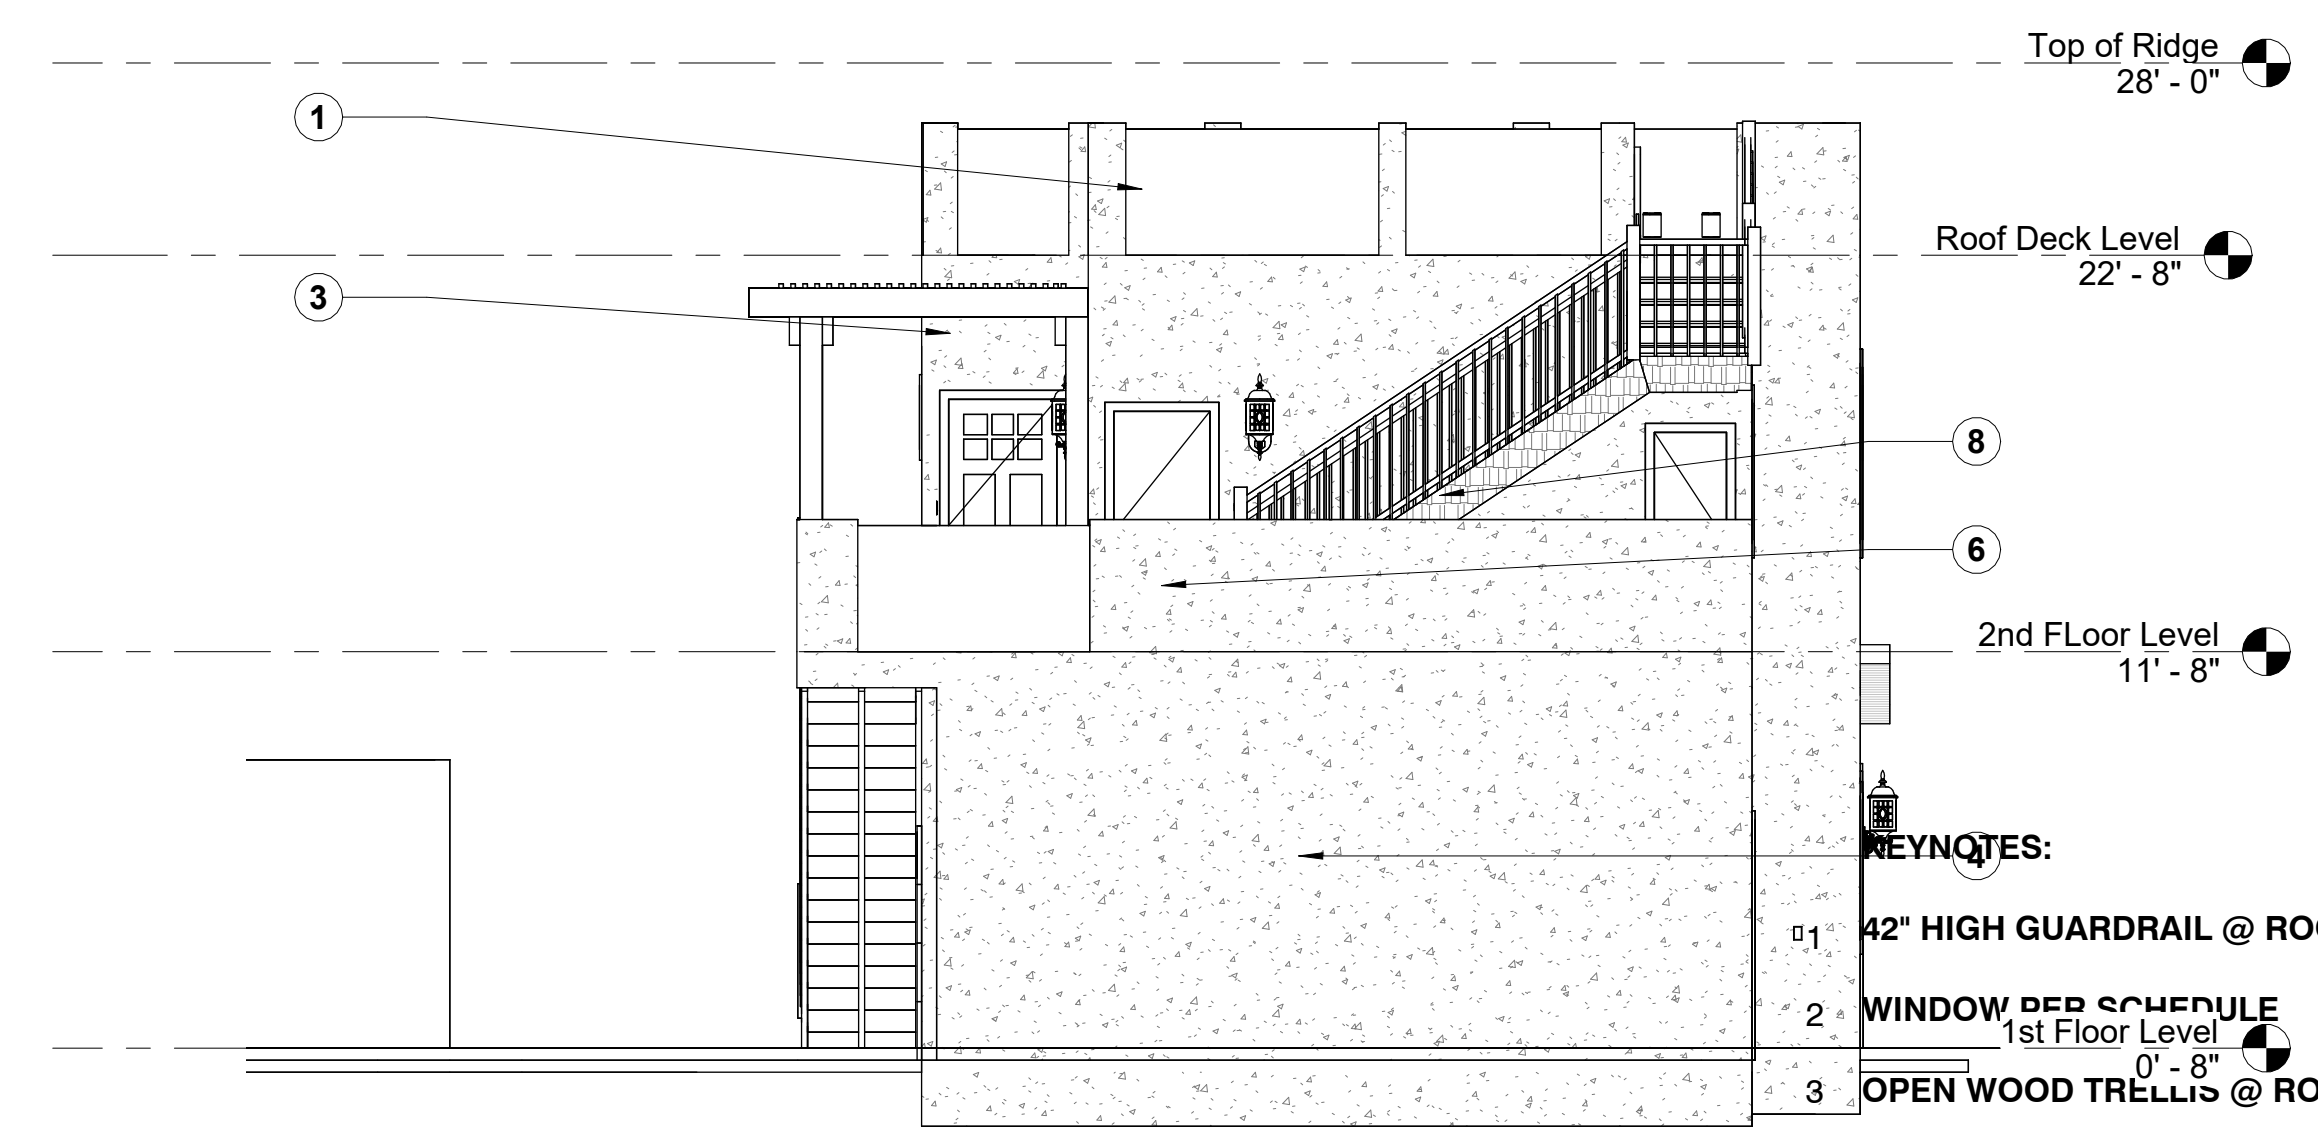

**4** *East Elev.*  
3/16" = 1'-0"

- KEYNOTES:**
- 1 42" HIGH GUARDRAIL @ ROOF DECK
  - 2 WINDOW PER SCHEDULE
  - 3 OPEN WOOD TRELLIS @ ROOF DECK
  - 4 STUCCO AT EXTERIOR WALL TO MATCH EXISTING
  - 5 EXTERIOR LIGHT
  - 6 EXTERIOR DOOR PER SCHEDULE
  - 7 SECTIONAL GARAGE DOOR
  - 8 EXTERIOR MTL STAIR W/ 42" GUARDRAIL