



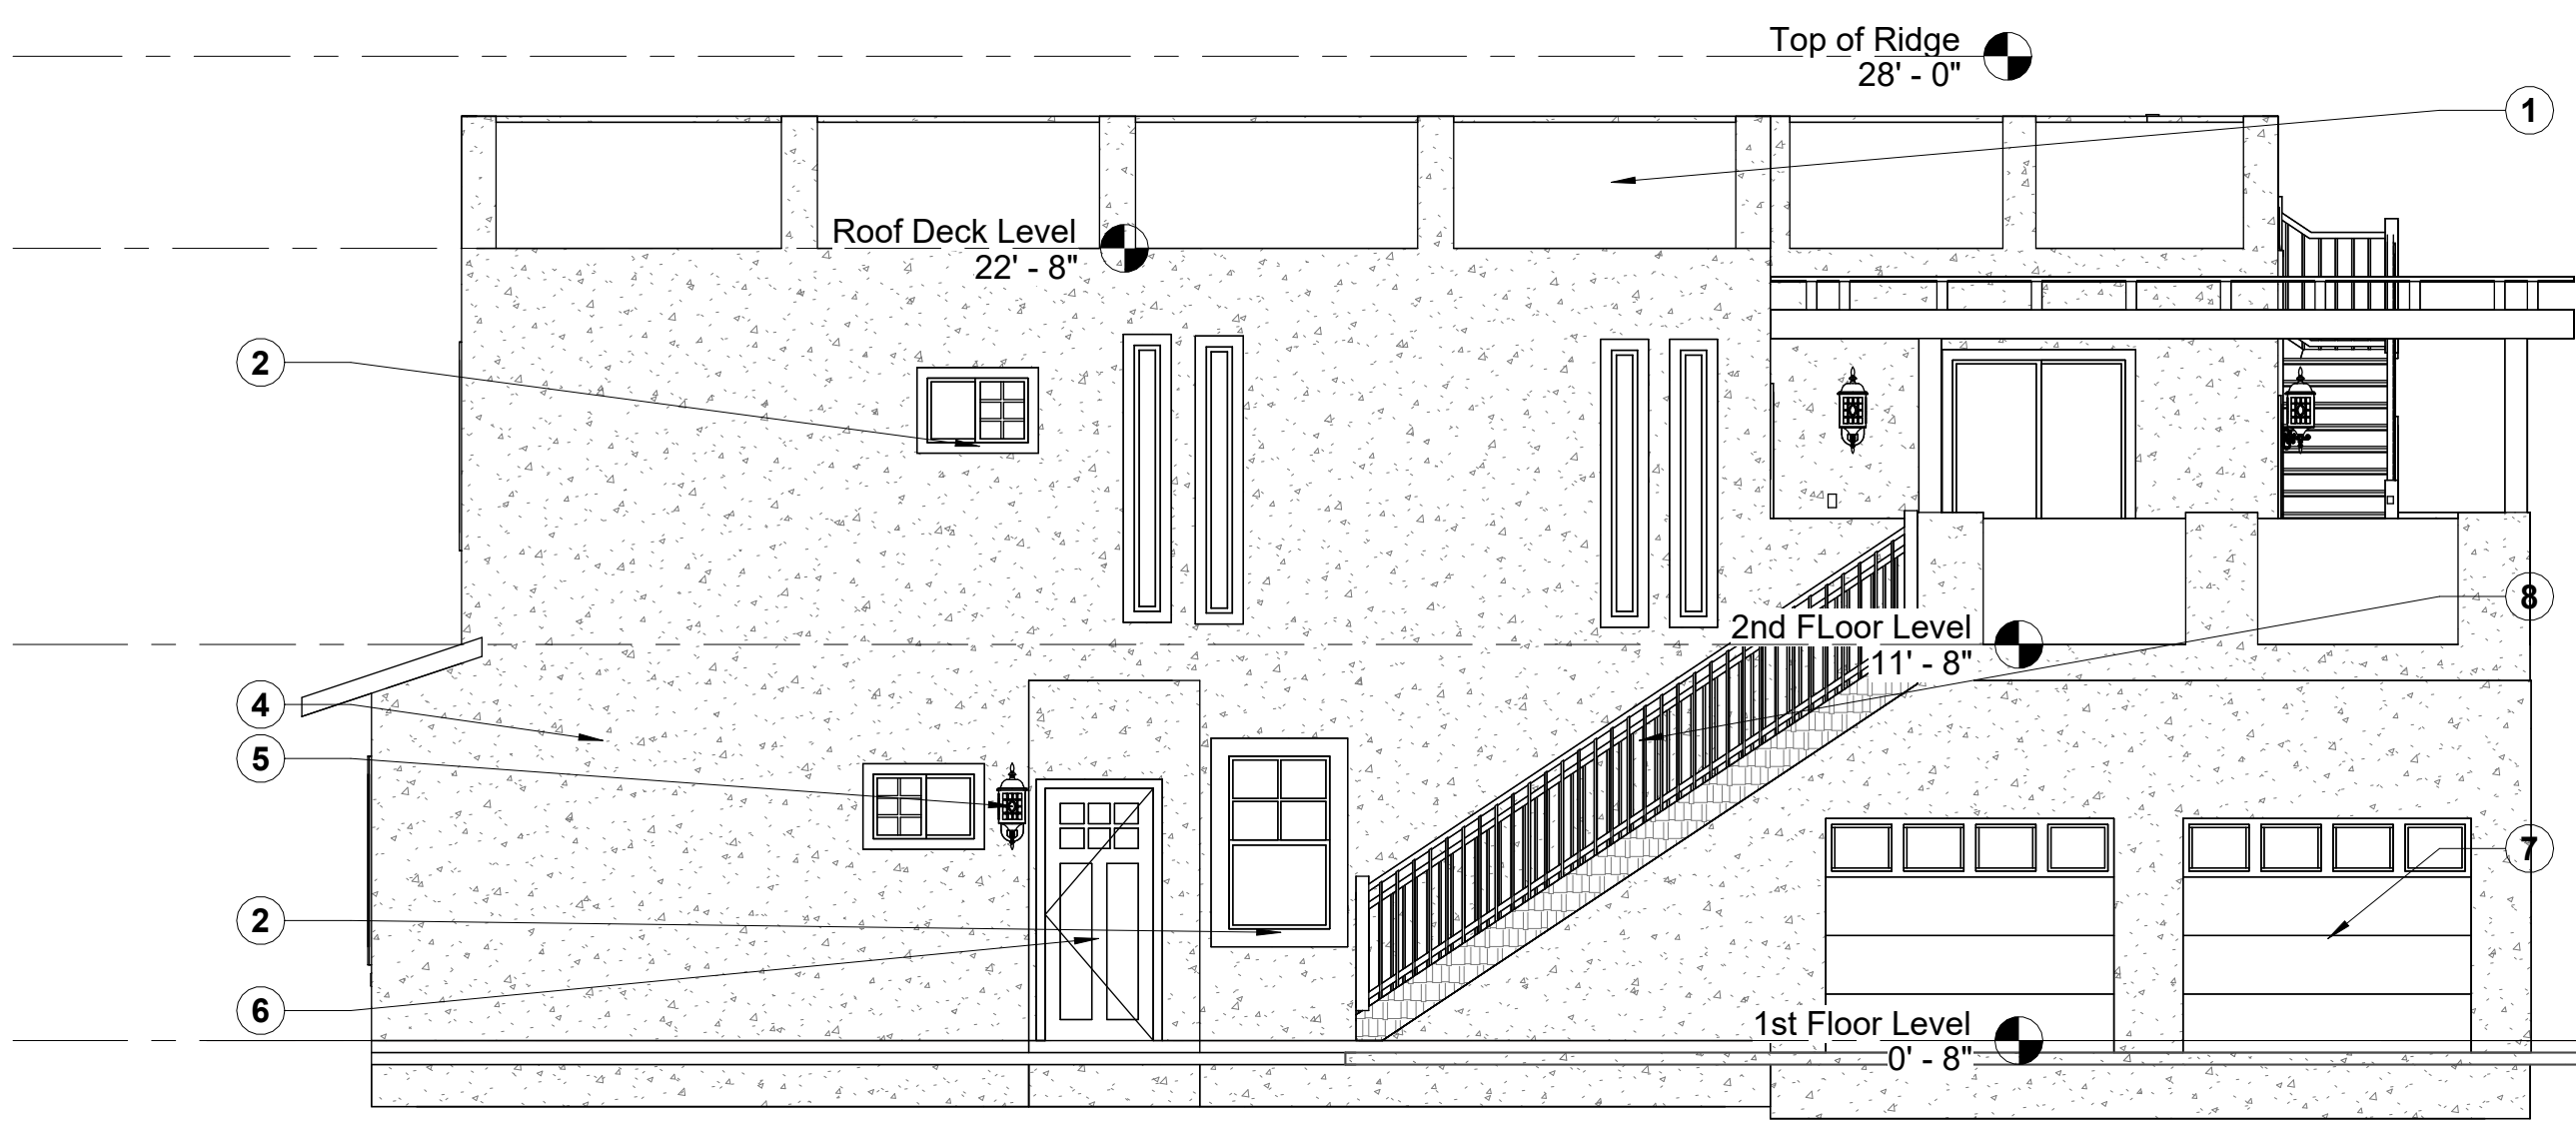


1 *South Elev.*
3/16" = 1'-0"

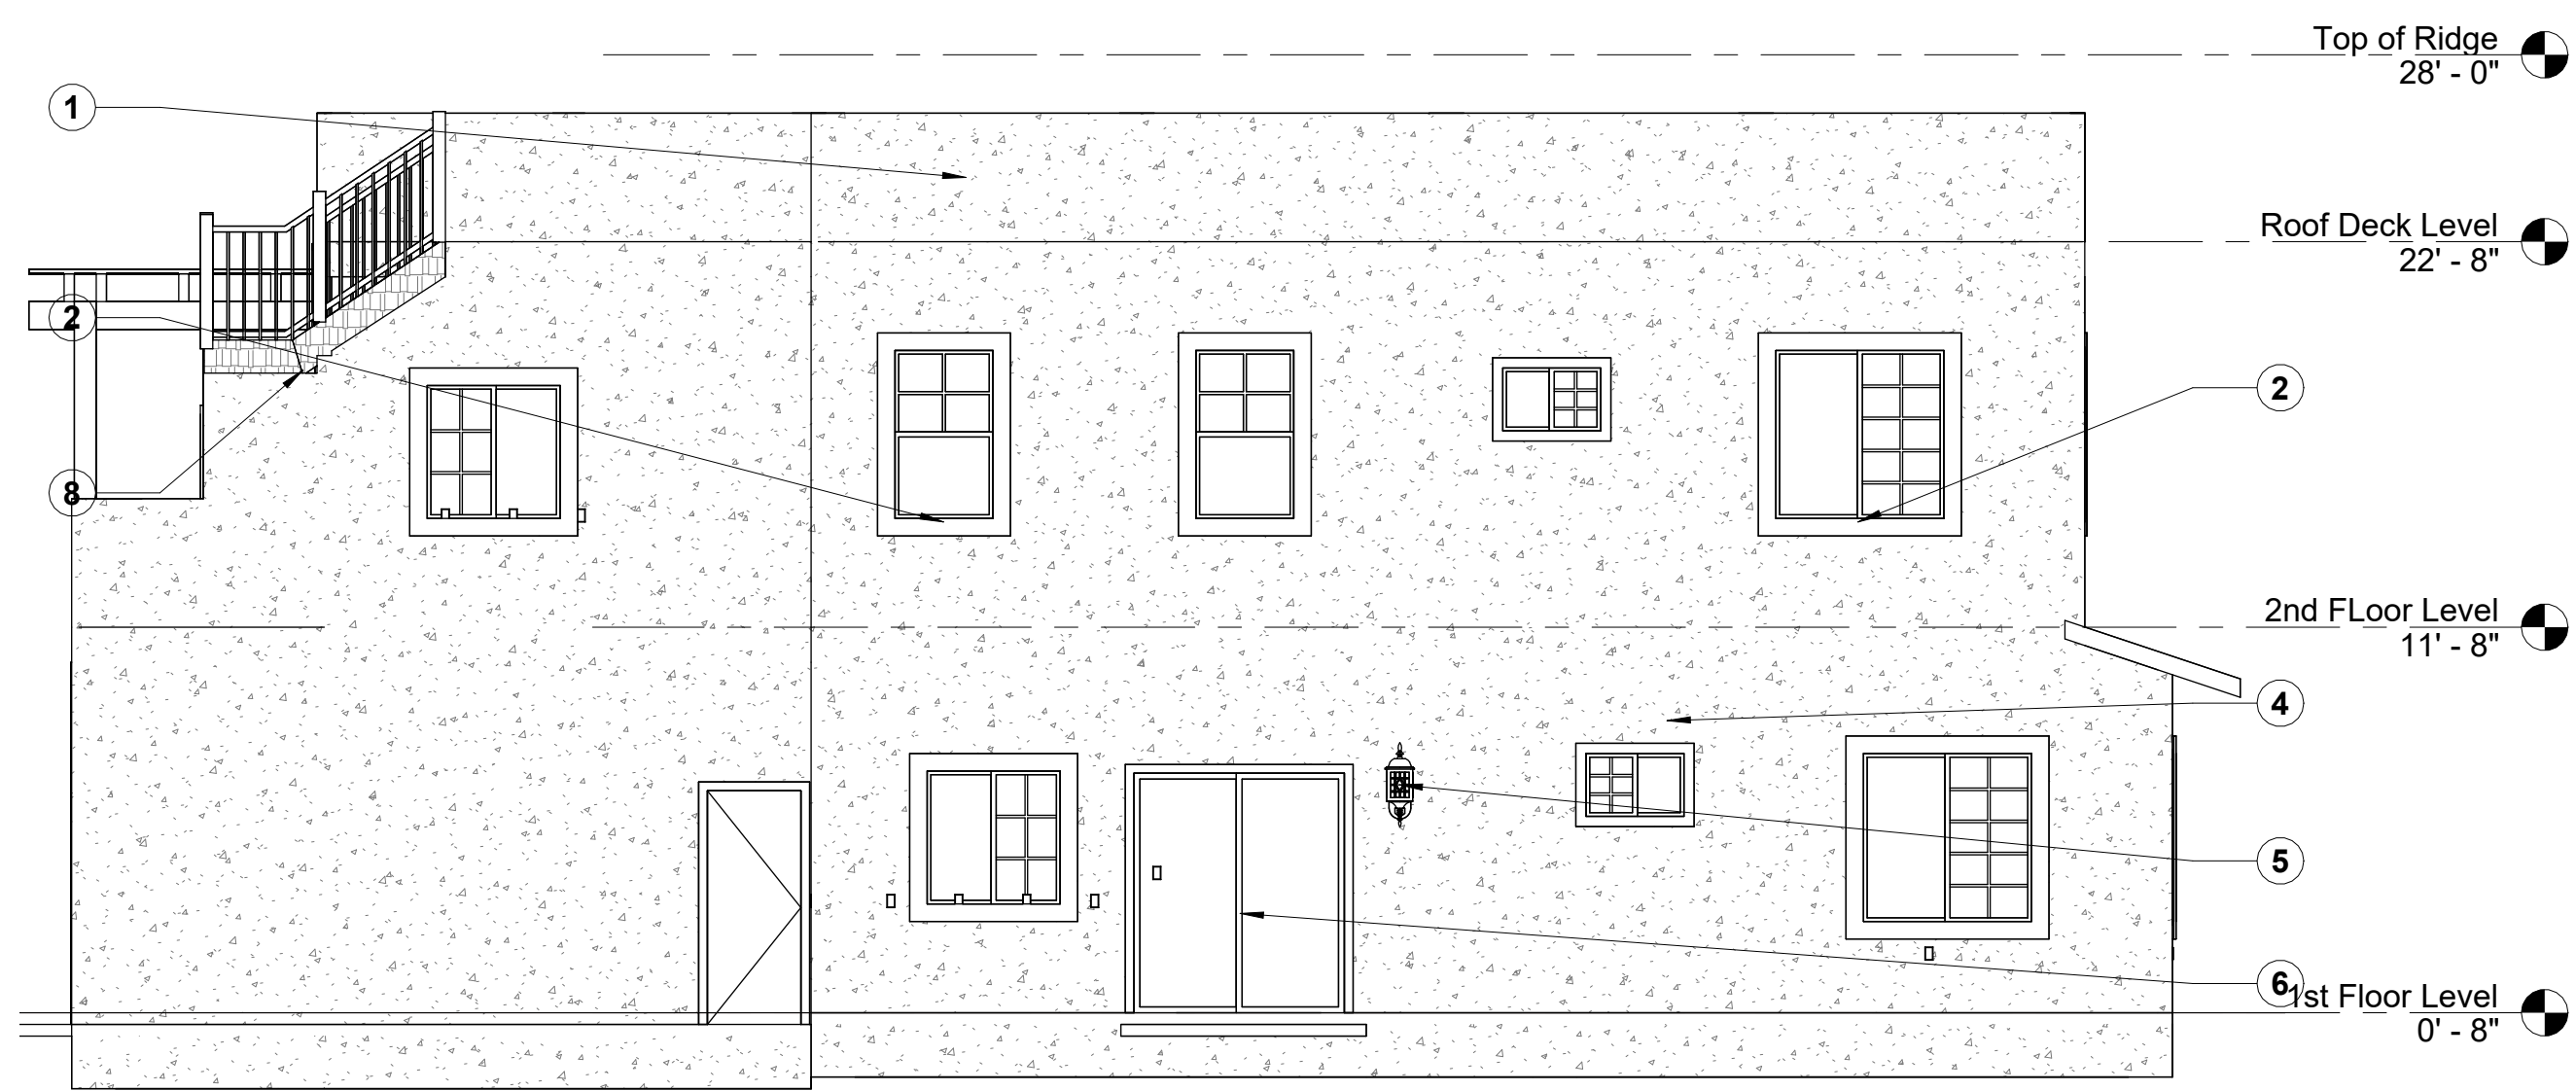


2 *North Elev.*
3/16" = 1'-0"

KEYNOTES:

- 1 42" HIGH GUARDRAIL @ ROOF DECK
- 2 WINDOW PER SCHEDULE
- 3 OPEN WOOD TRELLIS @ ROOF DECK
- 4 STUCCO AT EXTERIOR WALL TO MATCH EXISTING
- 5 EXTERIOR LIGHT
- 6 EXTERIOR DOOR PER SCHEDULE
- 7 SECTIONAL GARAGE DOOR
- 8 EXTERIOR MTL STAIR W/ 42" GUARDRAIL

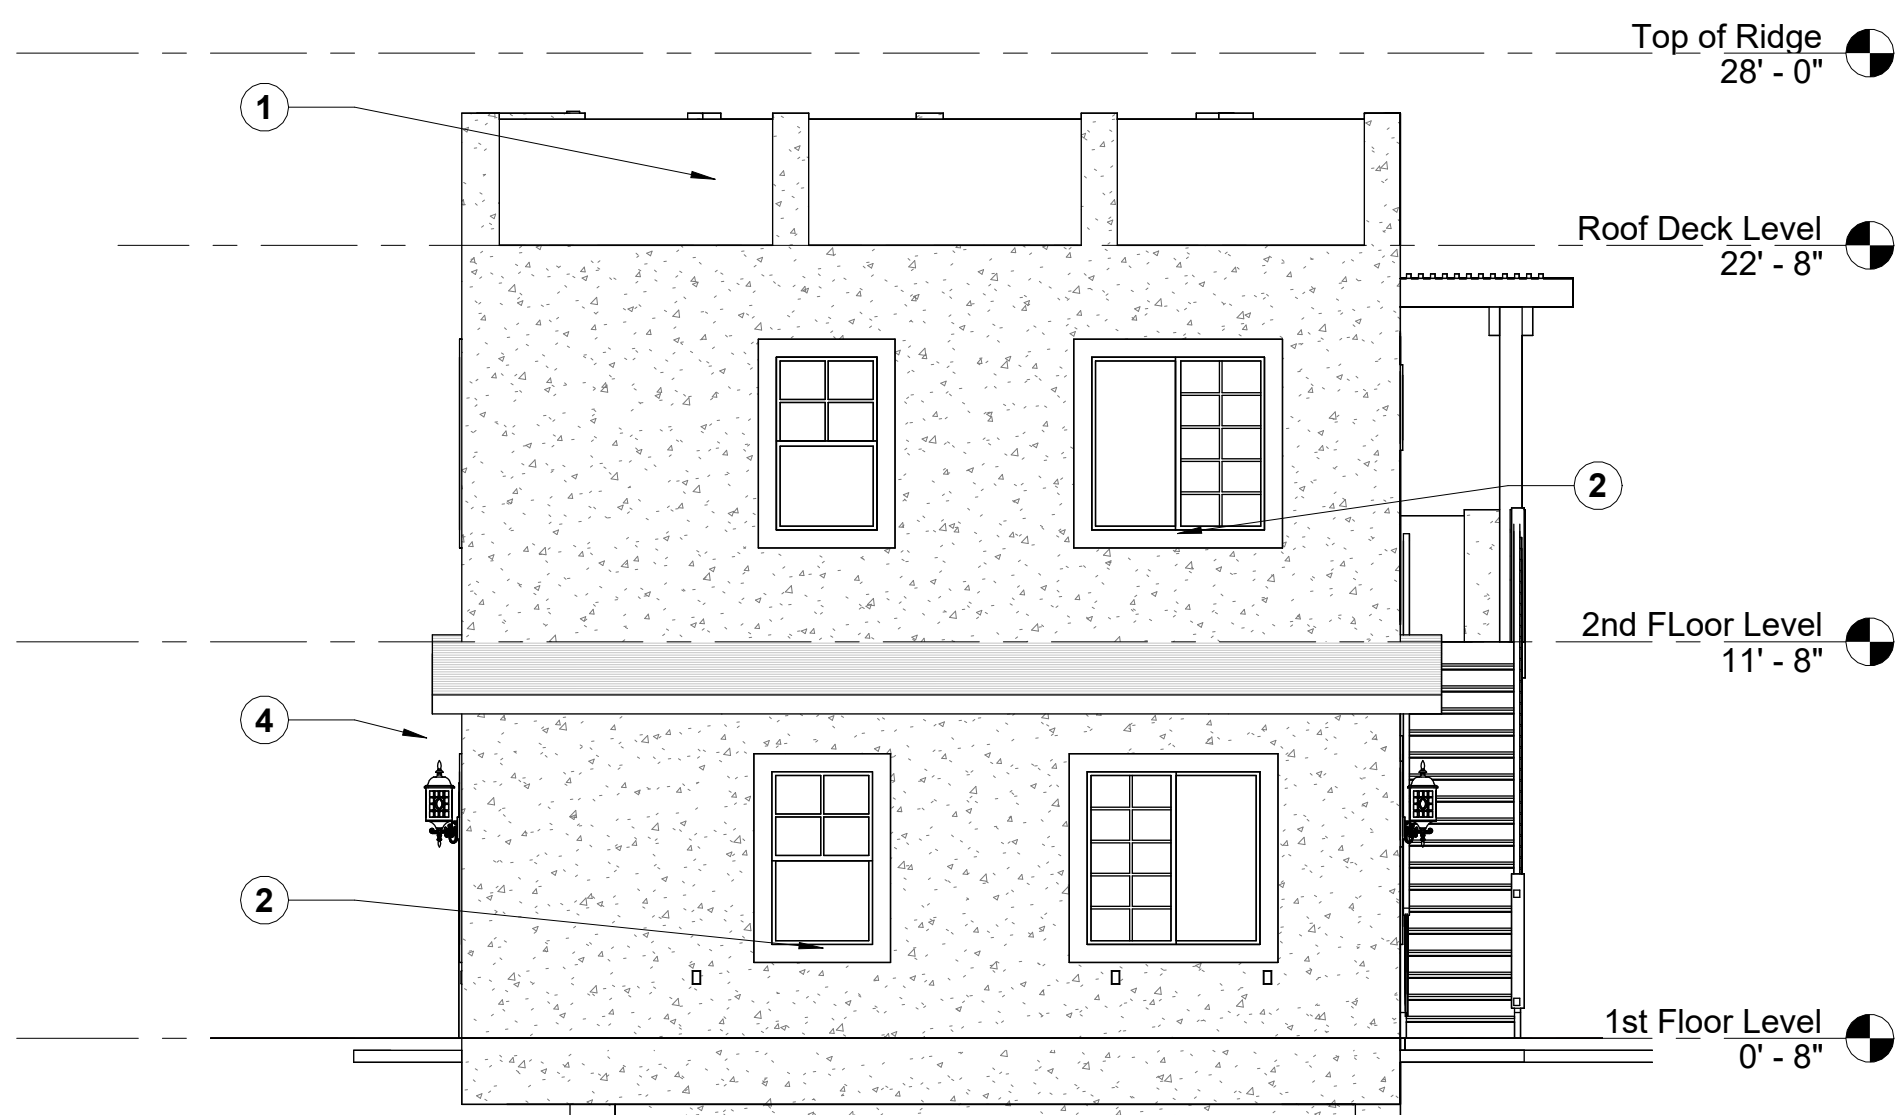

3 *West Elev.*
3/16" = 1'-0"

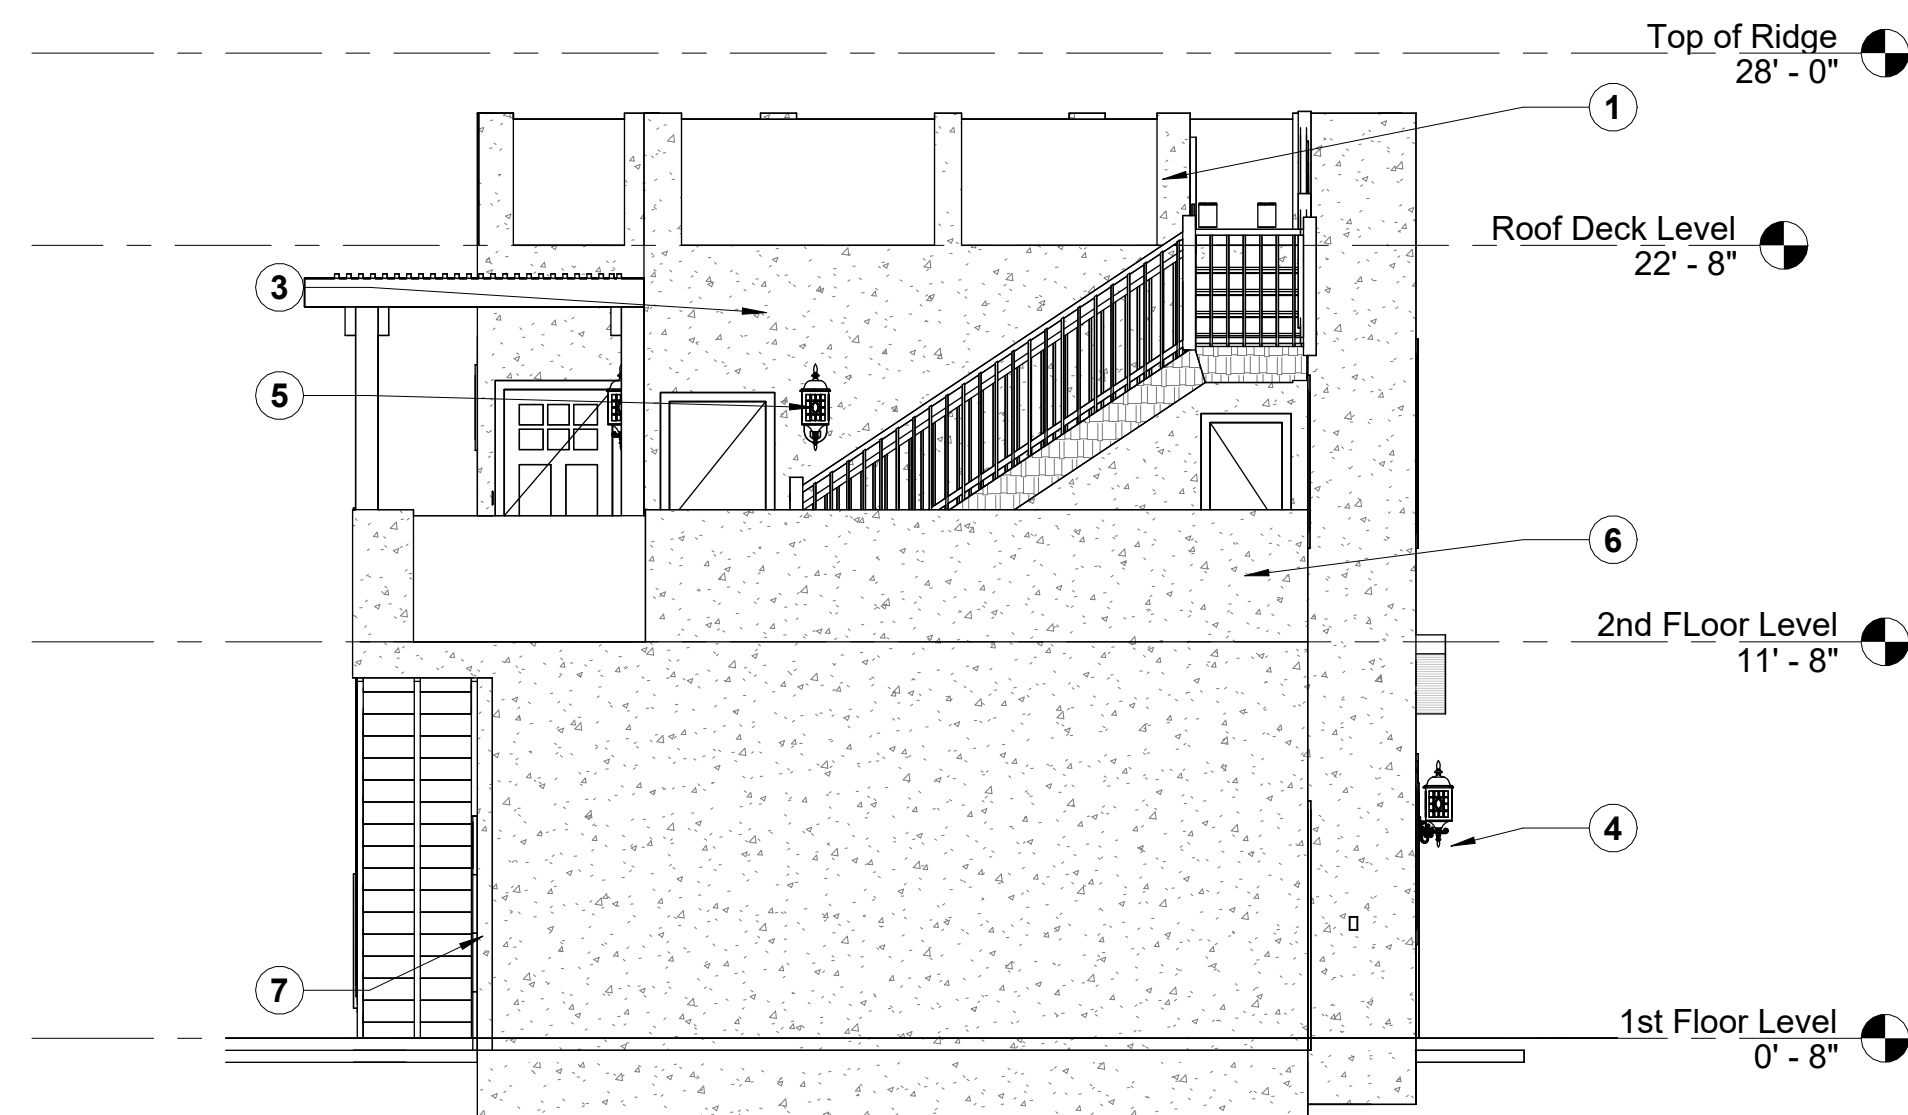

4 *East Elev.*
3/16" = 1'-0"