



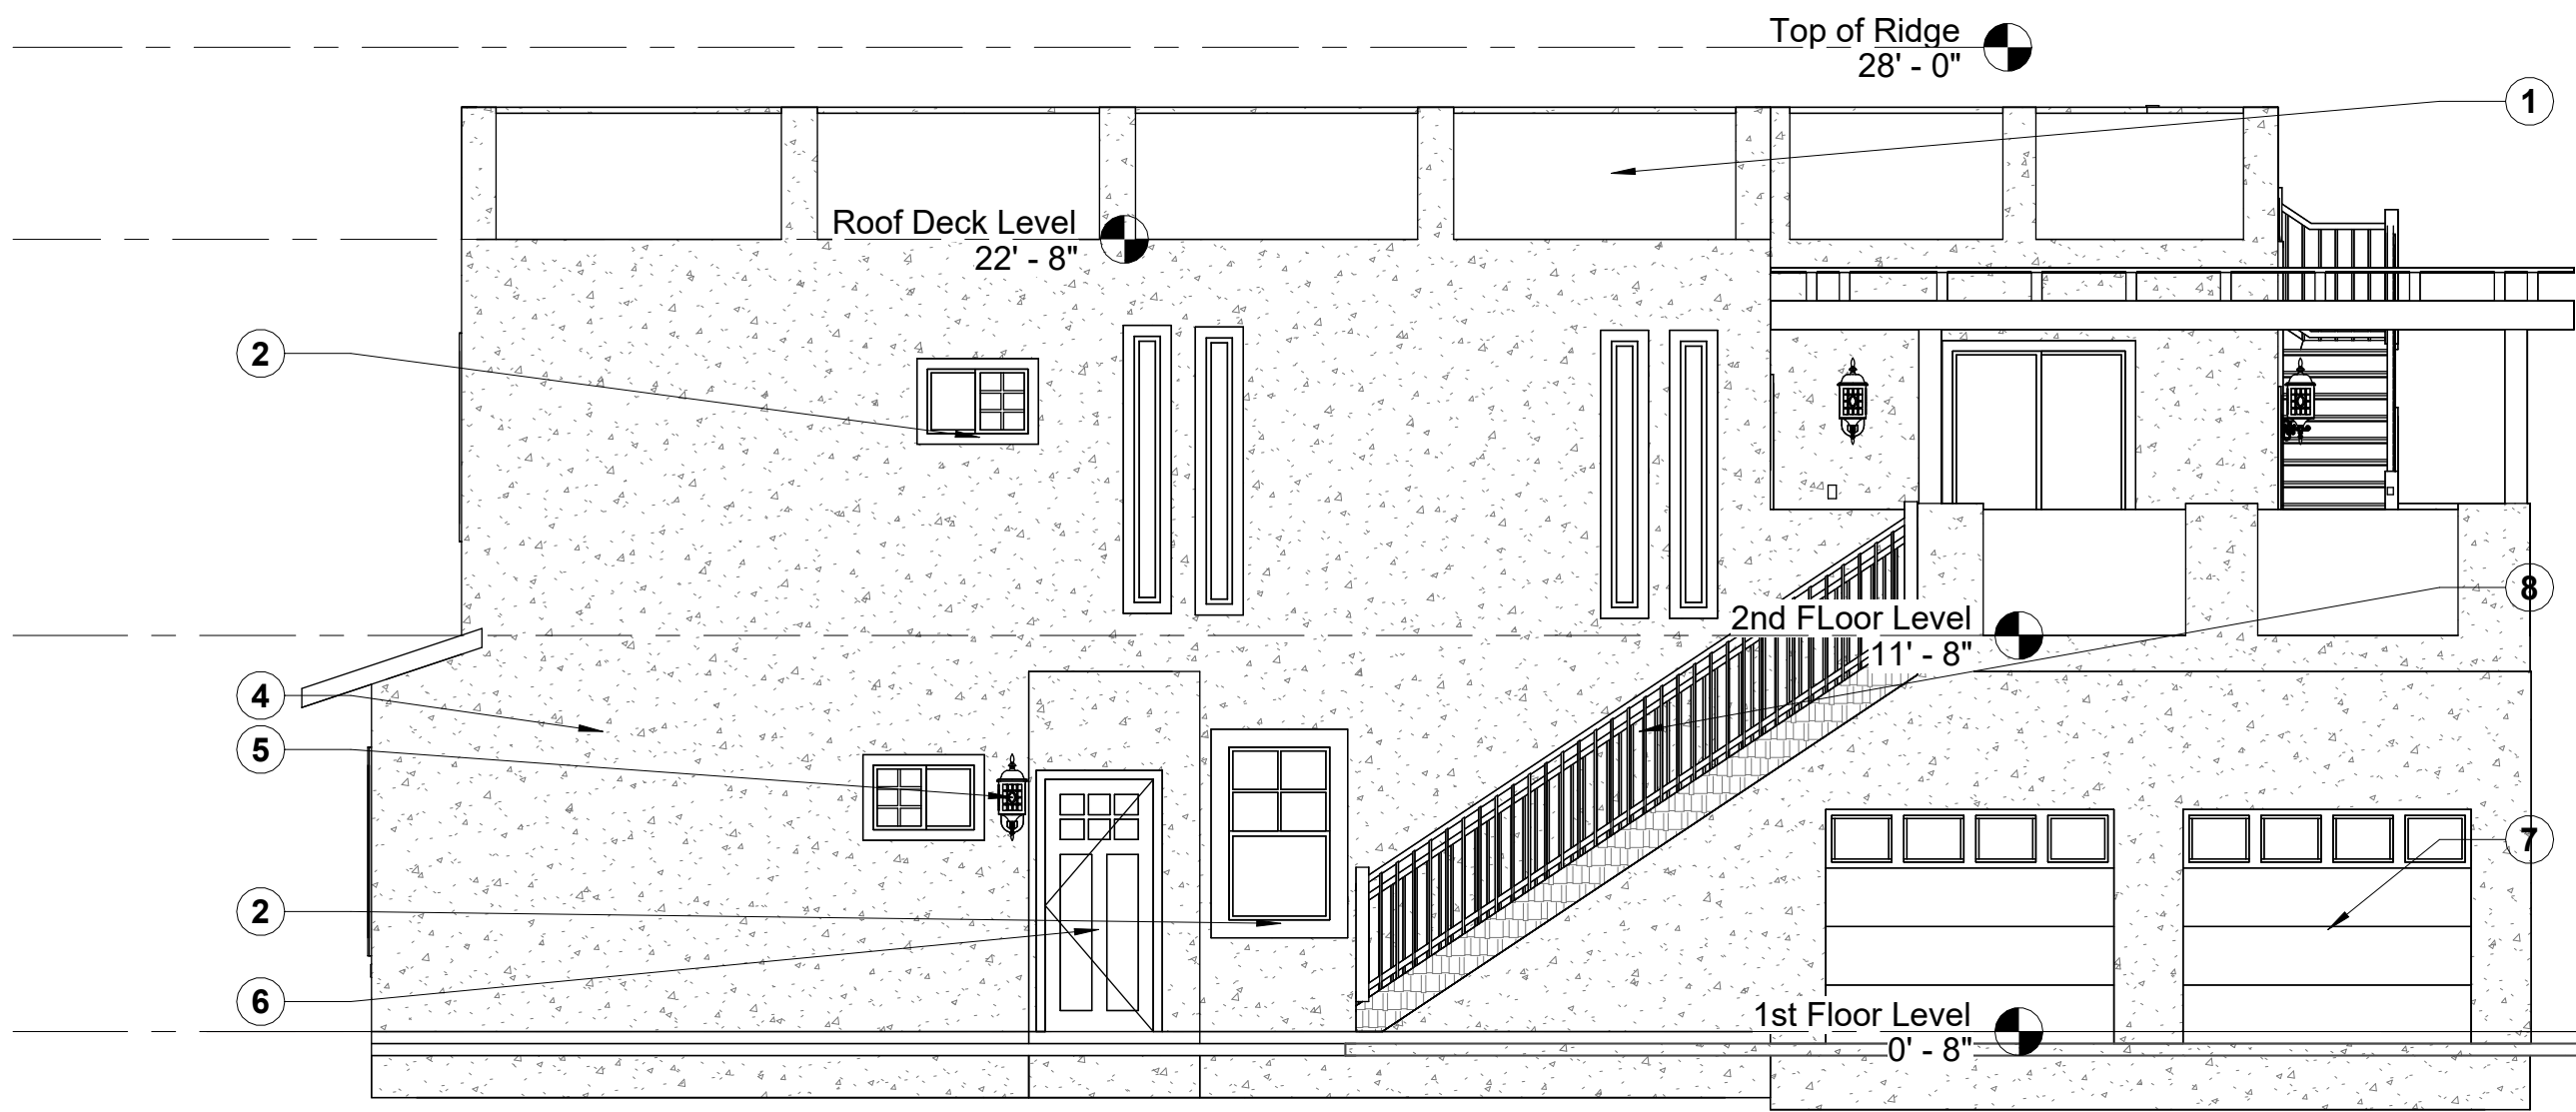

1 *South Elev.*
3/16" = 1'-0"

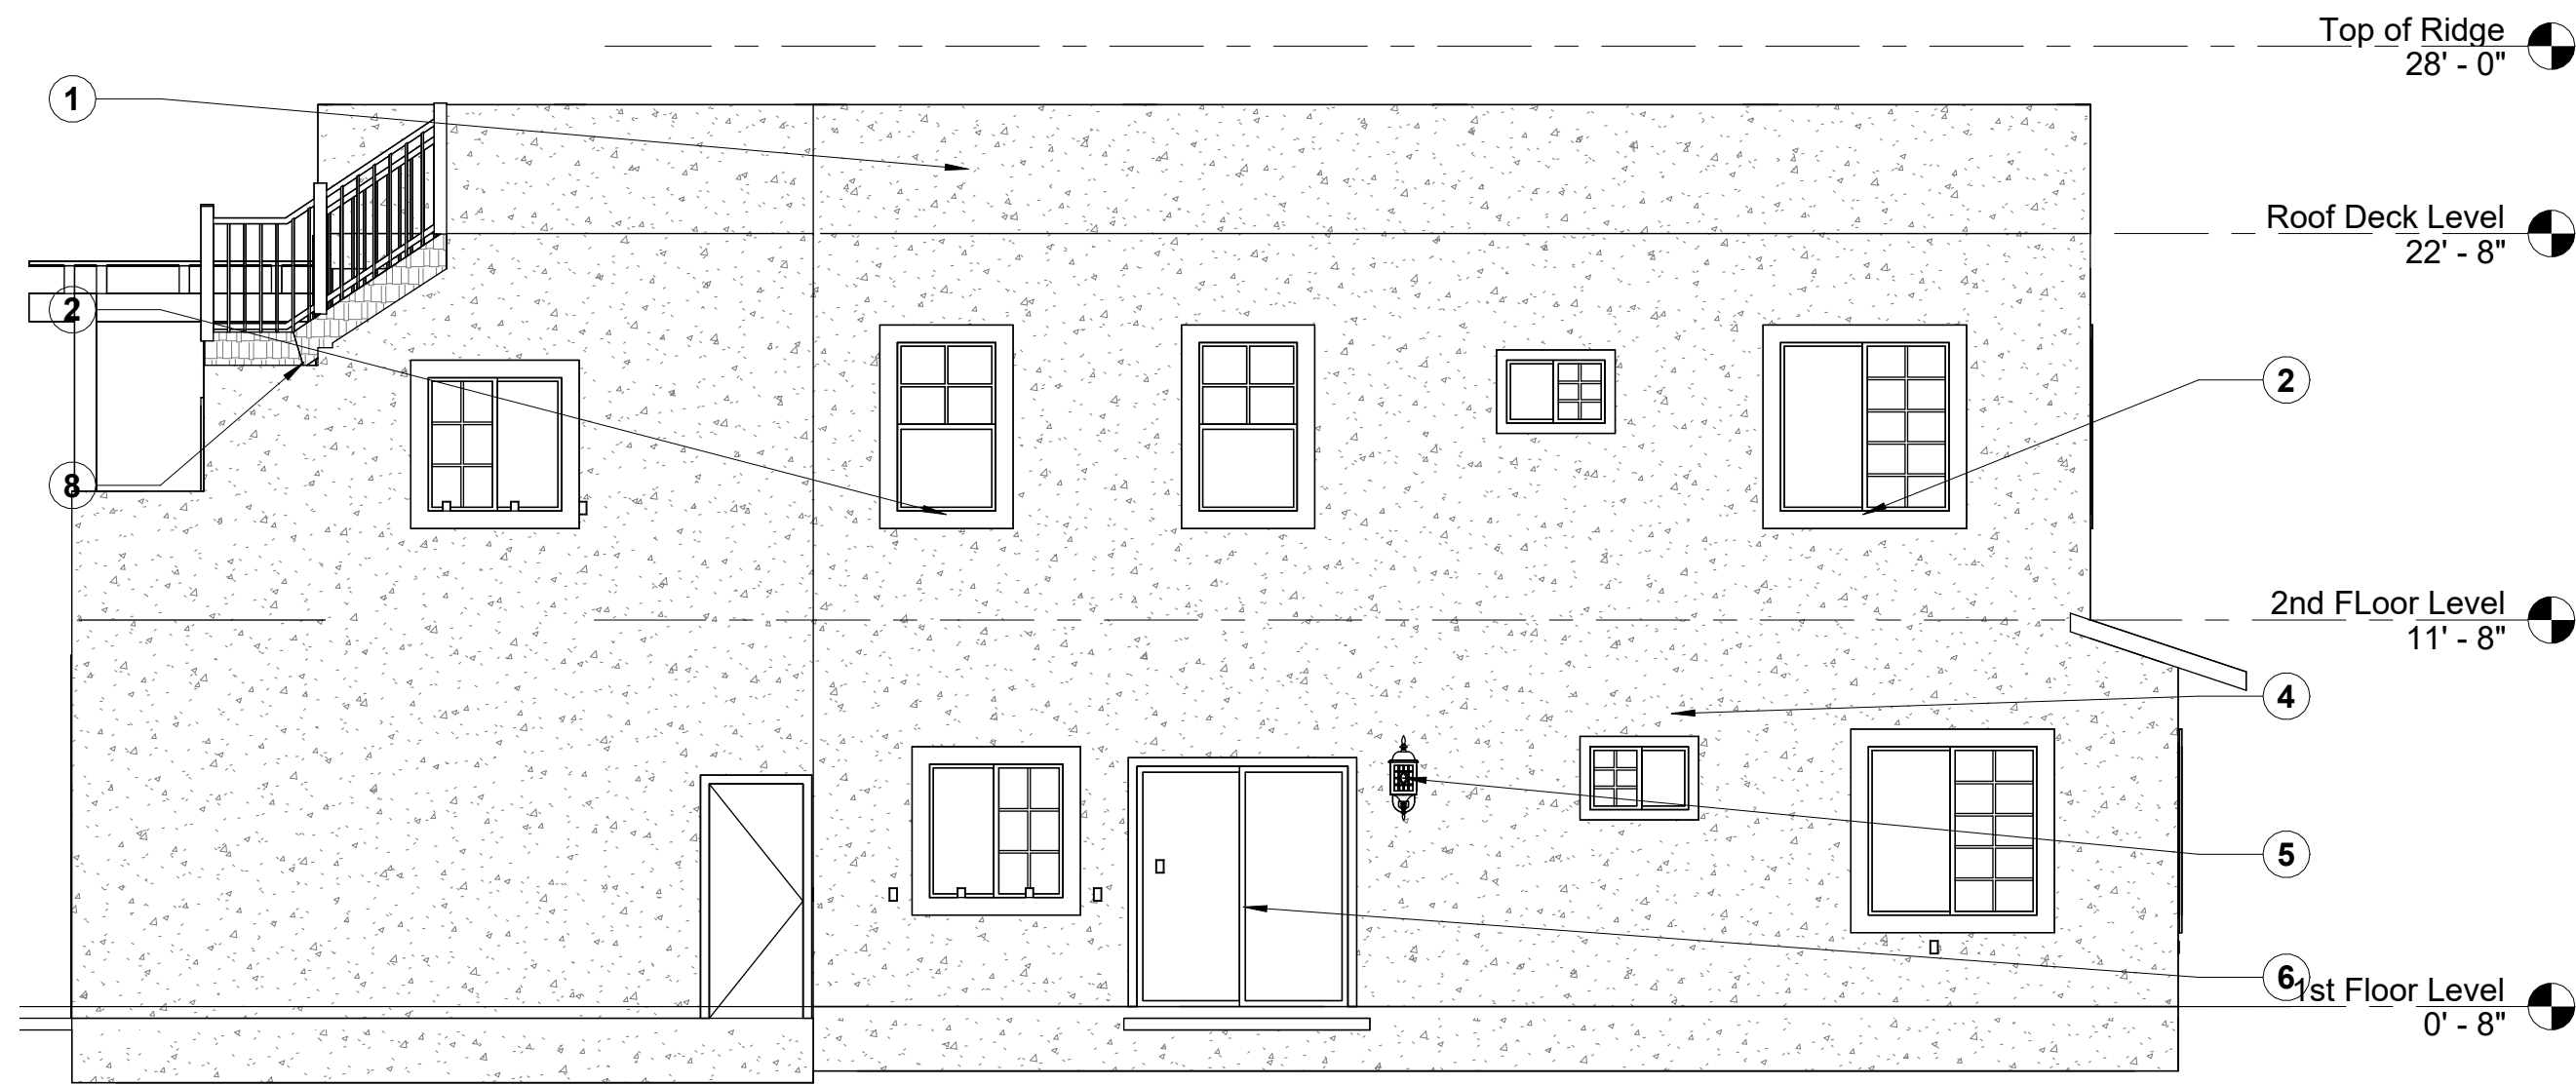


2 *North Elev.*
3/16" = 1'-0"

KEYNOTES:

- ① 42" HIGH GUARDRAIL @ ROOF DECK
- ② WINDOW PER SCHEDULE
- ③ OPEN WOOD TRELLIS @ ROOF DECK
- ④ STUCCO AT EXTERIOR WALL TO MATCH EXISTING
- ⑤ EXTERIOR LIGHT
- ⑥ EXTERIOR DOOR PER SCHEDULE
- ⑦ SECTIONAL GARAGE DOOR
- ⑧ EXTERIOR MTL STAIR W/ 42" GUARDRAIL



3 *West Elev.*
3/16" = 1'-0"

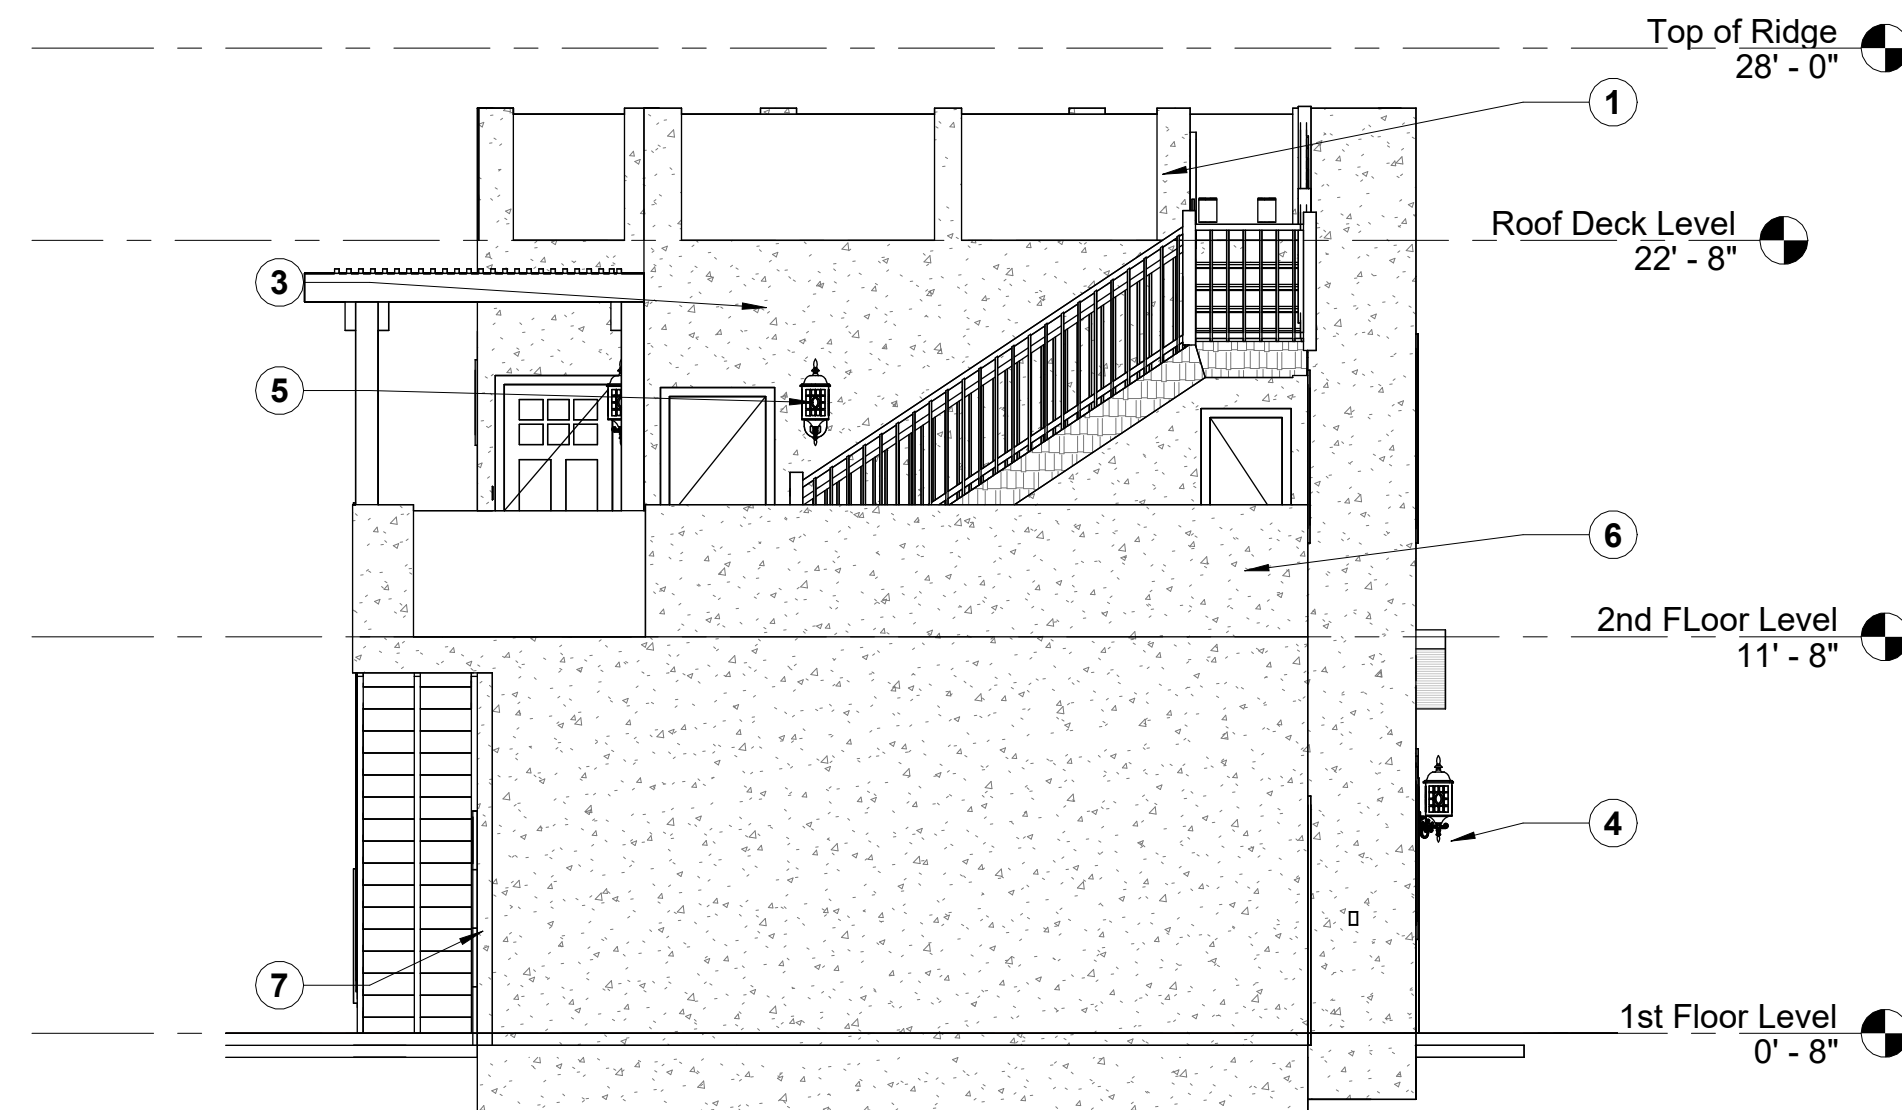

4 *East Elev.*
3/16" = 1'-0"