





SITE LOCATION

CITY PLANING:
CITY BUILDING:

11/ 6 / 2024

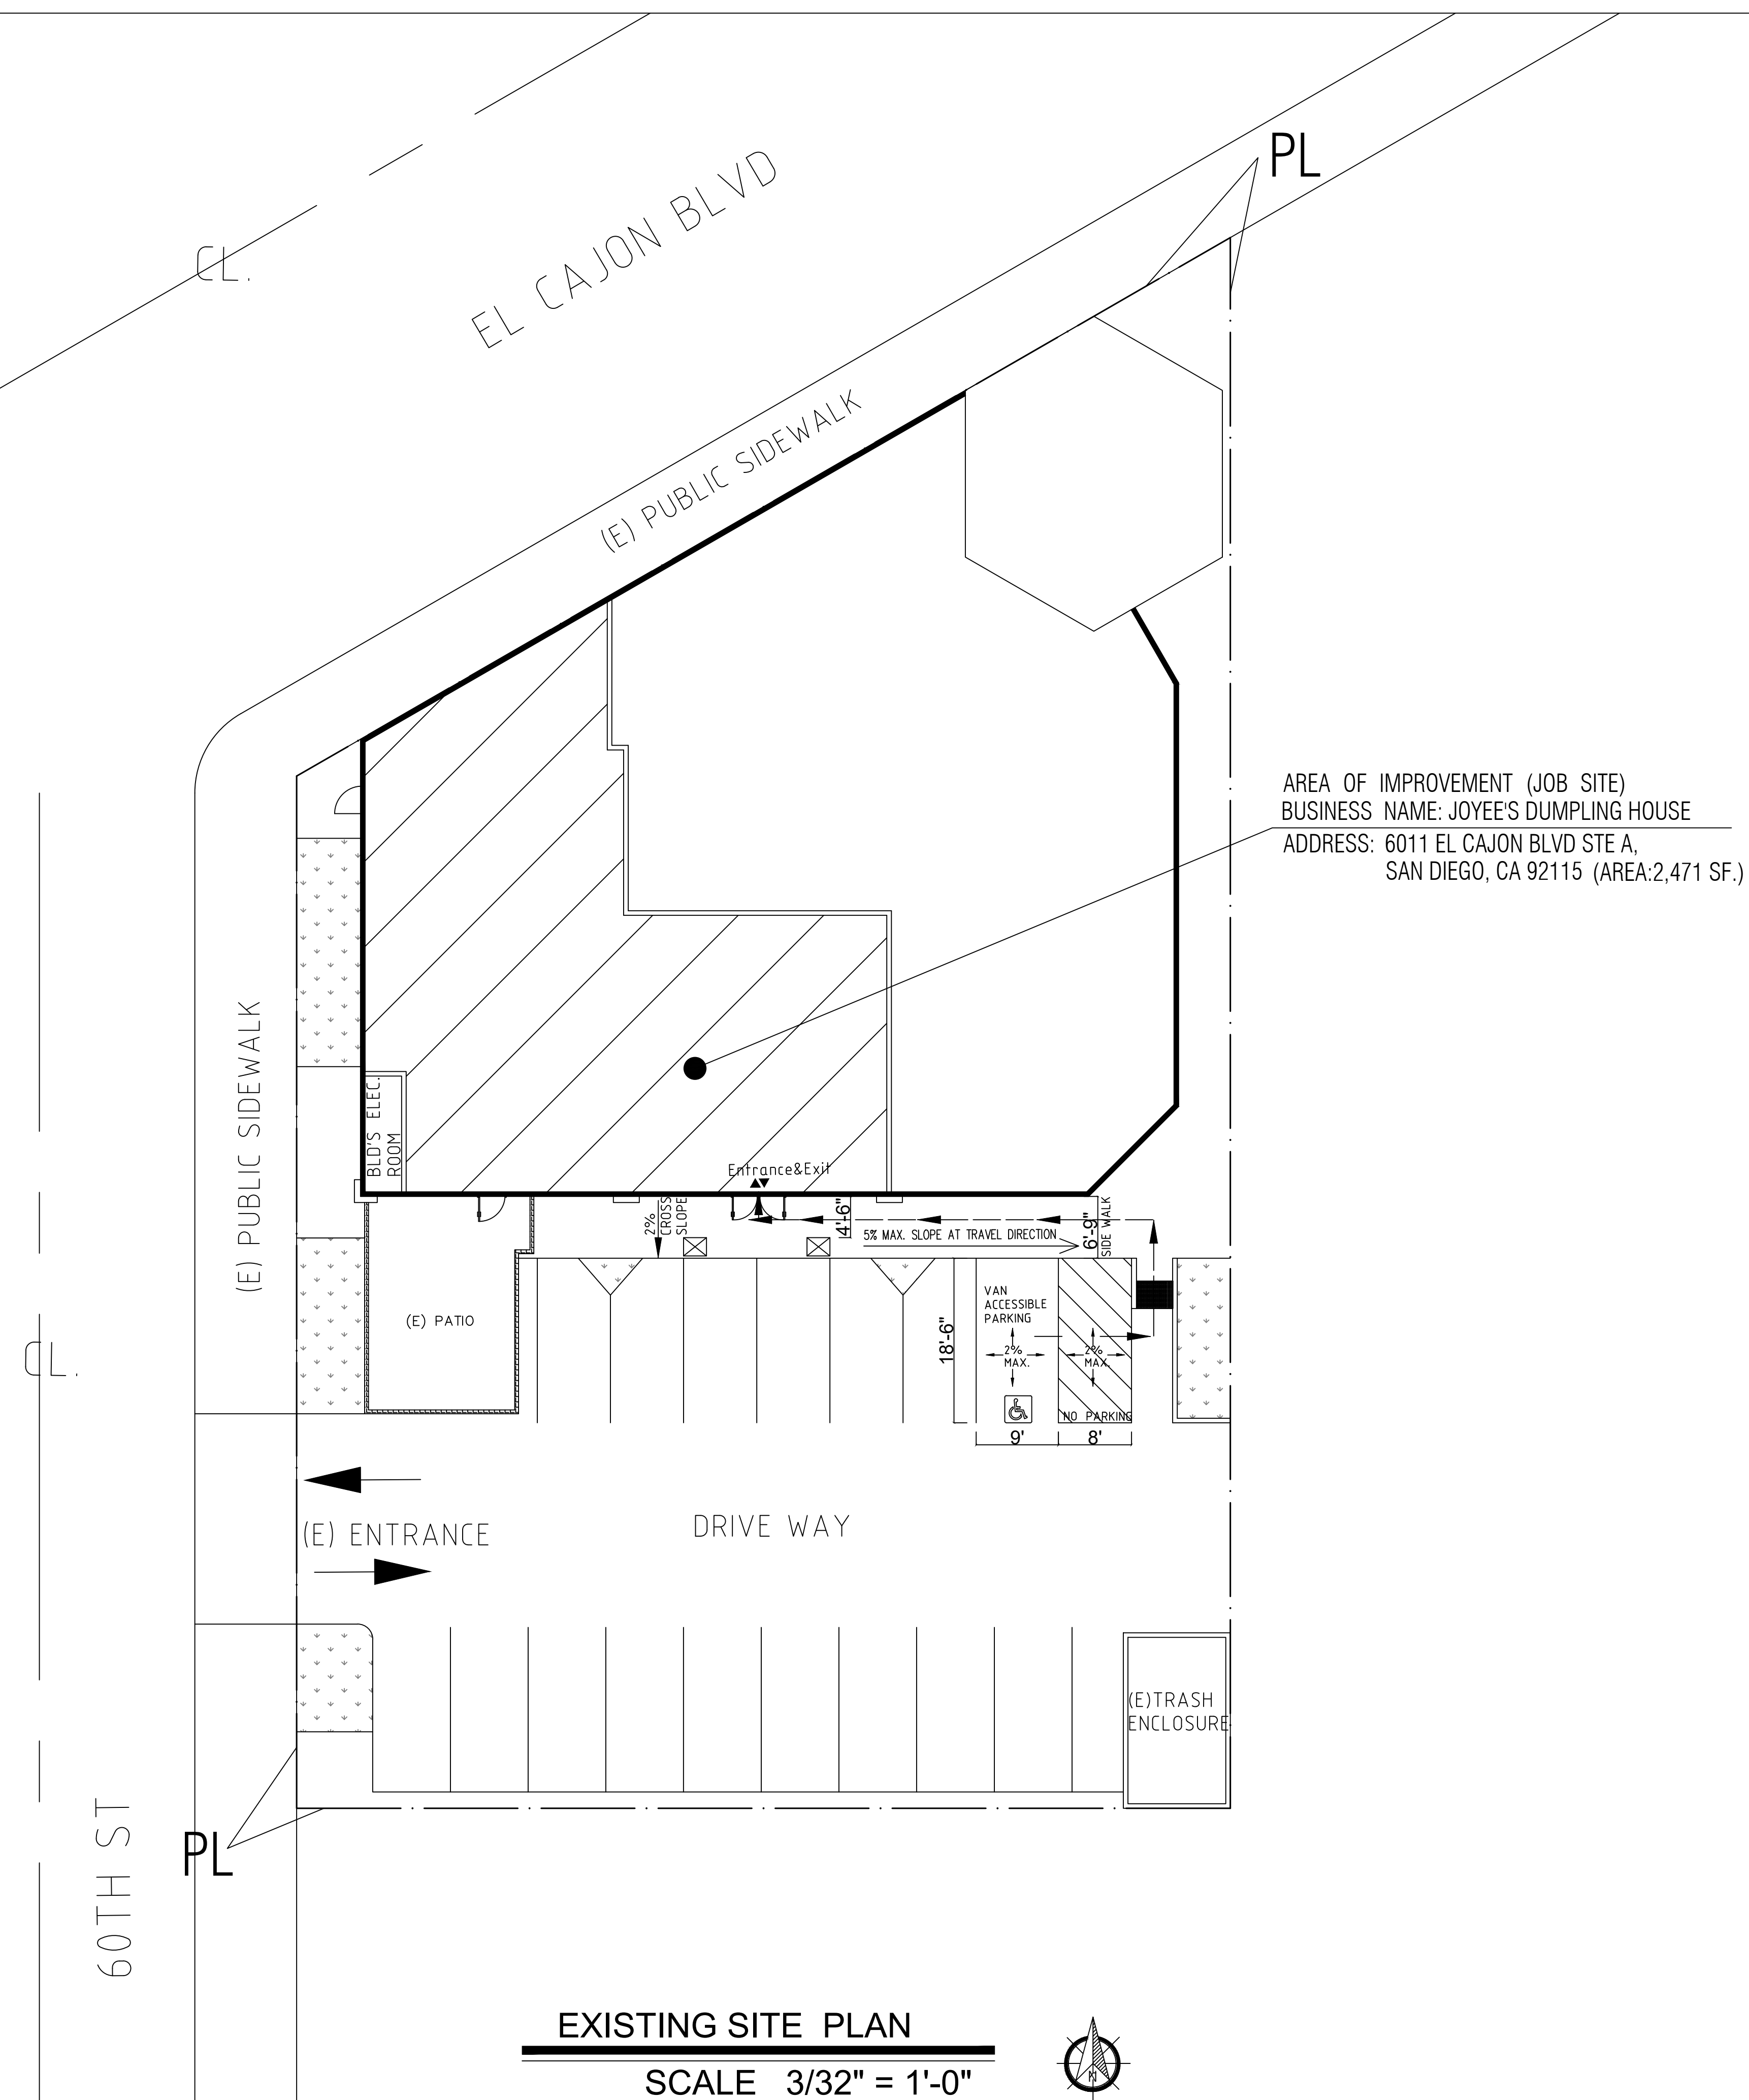

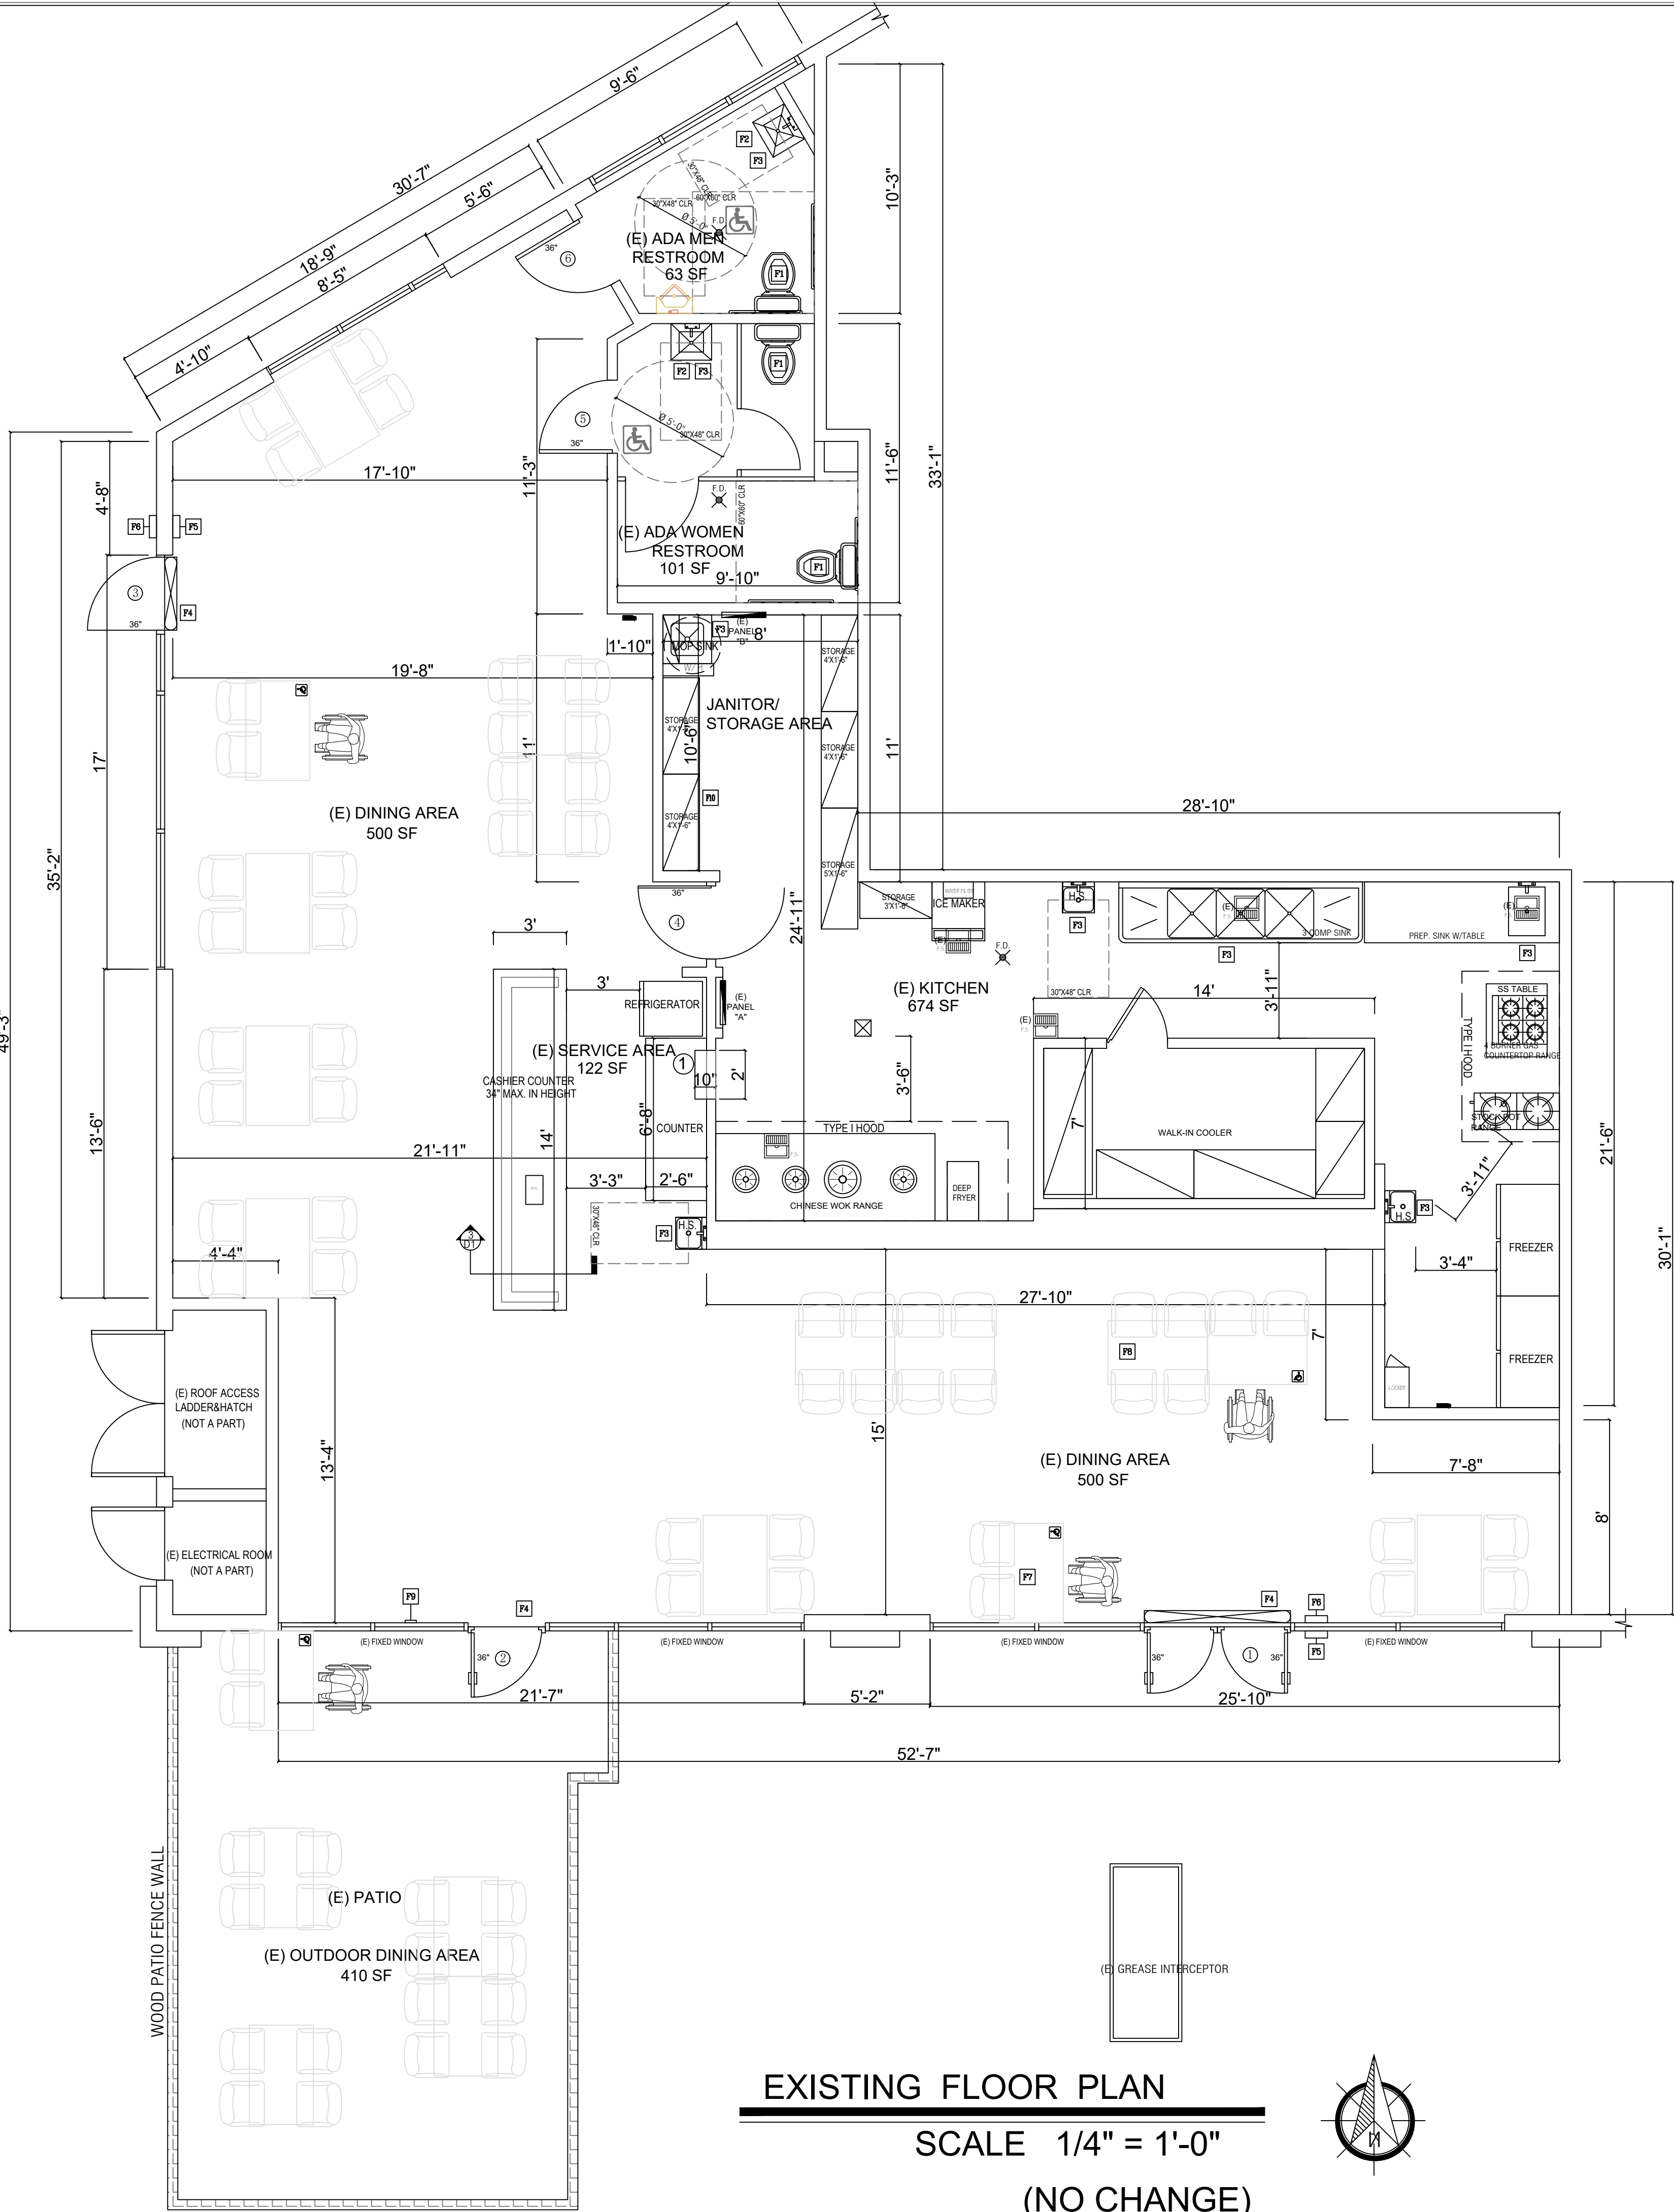



EXISTING FLOOR PLAN
SCALE 1/4" = 1'-0"
(NO CHANGE)

FLOOR PLAN KEY NOTES

- (E) TOILET WITH GRAB BAR & MEET ADA. REQUIREMENT. (TOILET DETAILS SEE 1/D2. GRAB BAR DETAIL SEE ① ③ /D-2.)
- (E) SINK & MEET ADA. REQUIREMENT. (SEE 1/D2.).
- ALL SINKS IN THE FACILITY IS PROVIDED WITH HOT AND COLD WATER
- PROVIDE A SIGN ADJACENT TO THE MAIN EXIT DOOR AS FOLLOWS: "THIS DOOR TO REMAIN UNLOCKED WHEN THIS SPACE IS OCCUPIED" THE SIGN SHALL BE IN LETTERS 1" HIGH ON A CONTRASTING BACKGROUND.
- (E) ADA ENTRY SIGN (SEE 3/D3).
- TACTILE SIGN (SEE 4/D3).
- ADA SEATING, DETAIL SEE 2/A3.
- MOVABLE TABLE AND CHAIRS.
- (E) MAXIMUM OCCUPANT LOAD SIGN.
- STORAGE OF FOOD: 96 LINEAL FEET.

LEGEND:

- EXISTING WALL TO REMAIN
- (E) POST
- DOOR NUMBER SEE DETAIL ON 1/D1
- (E) EXISTING
- (E) ELECTRICAL PANEL, 250 AMPS
- (E) ELECTRICAL PANEL, 250 AMPS
- F.S. = FLOOR SINK, SEE DETAIL ON 2/D-1.
- F.D. = FLOOR DRAIN, SEE DETAIL ON 3/D-2.
- (E) FIRE EXTINGUISHER RATED 2-A/10B/C.

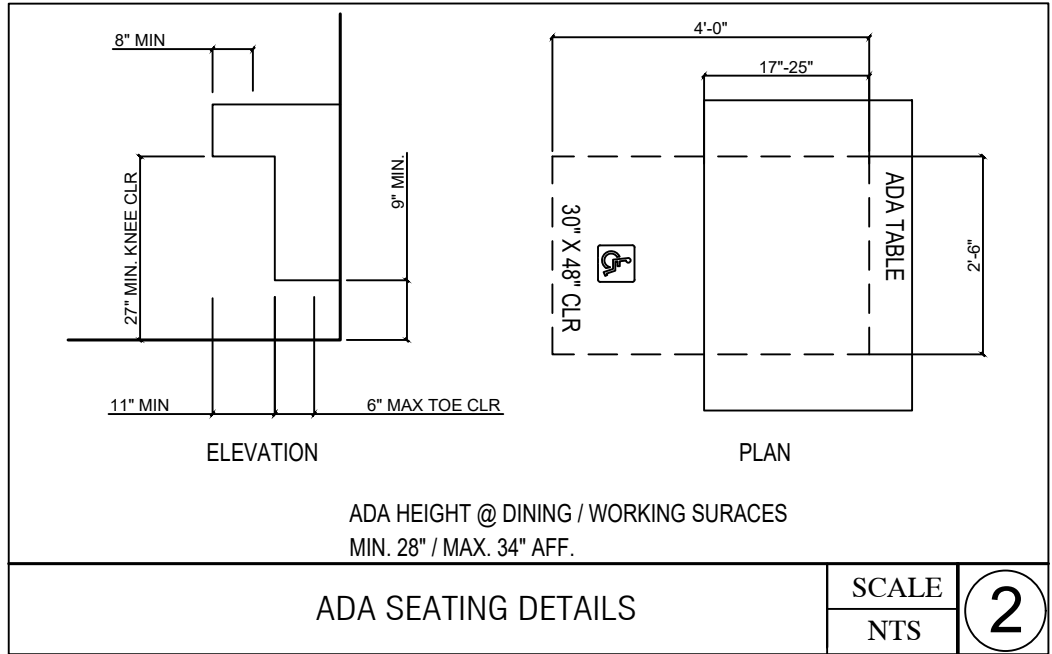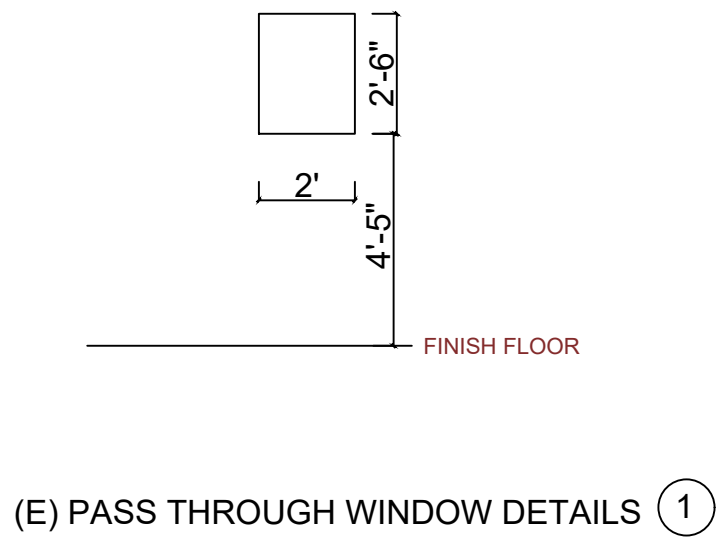

SCALE	N.T.S.	INTERIOR FINISH SCHEDULE	
		BUSINESS NAME: JOYEE'S DUMPLING HOUSE	
		JOB ADDRESS: 6011 E. CAJON BLVD STE A, SAN DIEGO, CA 92115	
DETAIL	ITEM		FLOOR				BASE				WALL				CEILING	
	ROOM NAME		QUARRY TILE SMOOTH	CONCRETE	PORCELAIN TILES	CERAMIC TILES	S. STEEL	VINYL FLOORING	PREFAB GALLY METAL	WOOD	VINYL BASE	QUARRY TILE R.F. SMOOTH	QUARRY TILE R.F. SMOOTH	STAINLESS STEEL	CERAMIC TILE R.F. SMOOTH	QUARRY TILE R.F. SMOOTH	QUARRY TILE R.F

REVISIONS

PLAN CHECK CORRECTION	
R-1	
R-2	
R-1	
R-1	
1ST. SUBMITAL:	
2ND. SUBMITAL:	
3RD. SUBMITAL:	
PERMIT#	
CITY PLANING:	
CITY BUILDING:	

TOPWAY ARCHI
DESIGN/BUILD
COMMERCIAL AND RESIDENTIAL
CAROLYN ZENG 626-400-0736


JOYEE'S DUMPLING HOUSE

6011 EL CAJON BLVD STE A

SAN DIEGO, CA 92115

(E) FLOOR PLAN

SHEET
A-2
DATE
11/ 6 / 2024

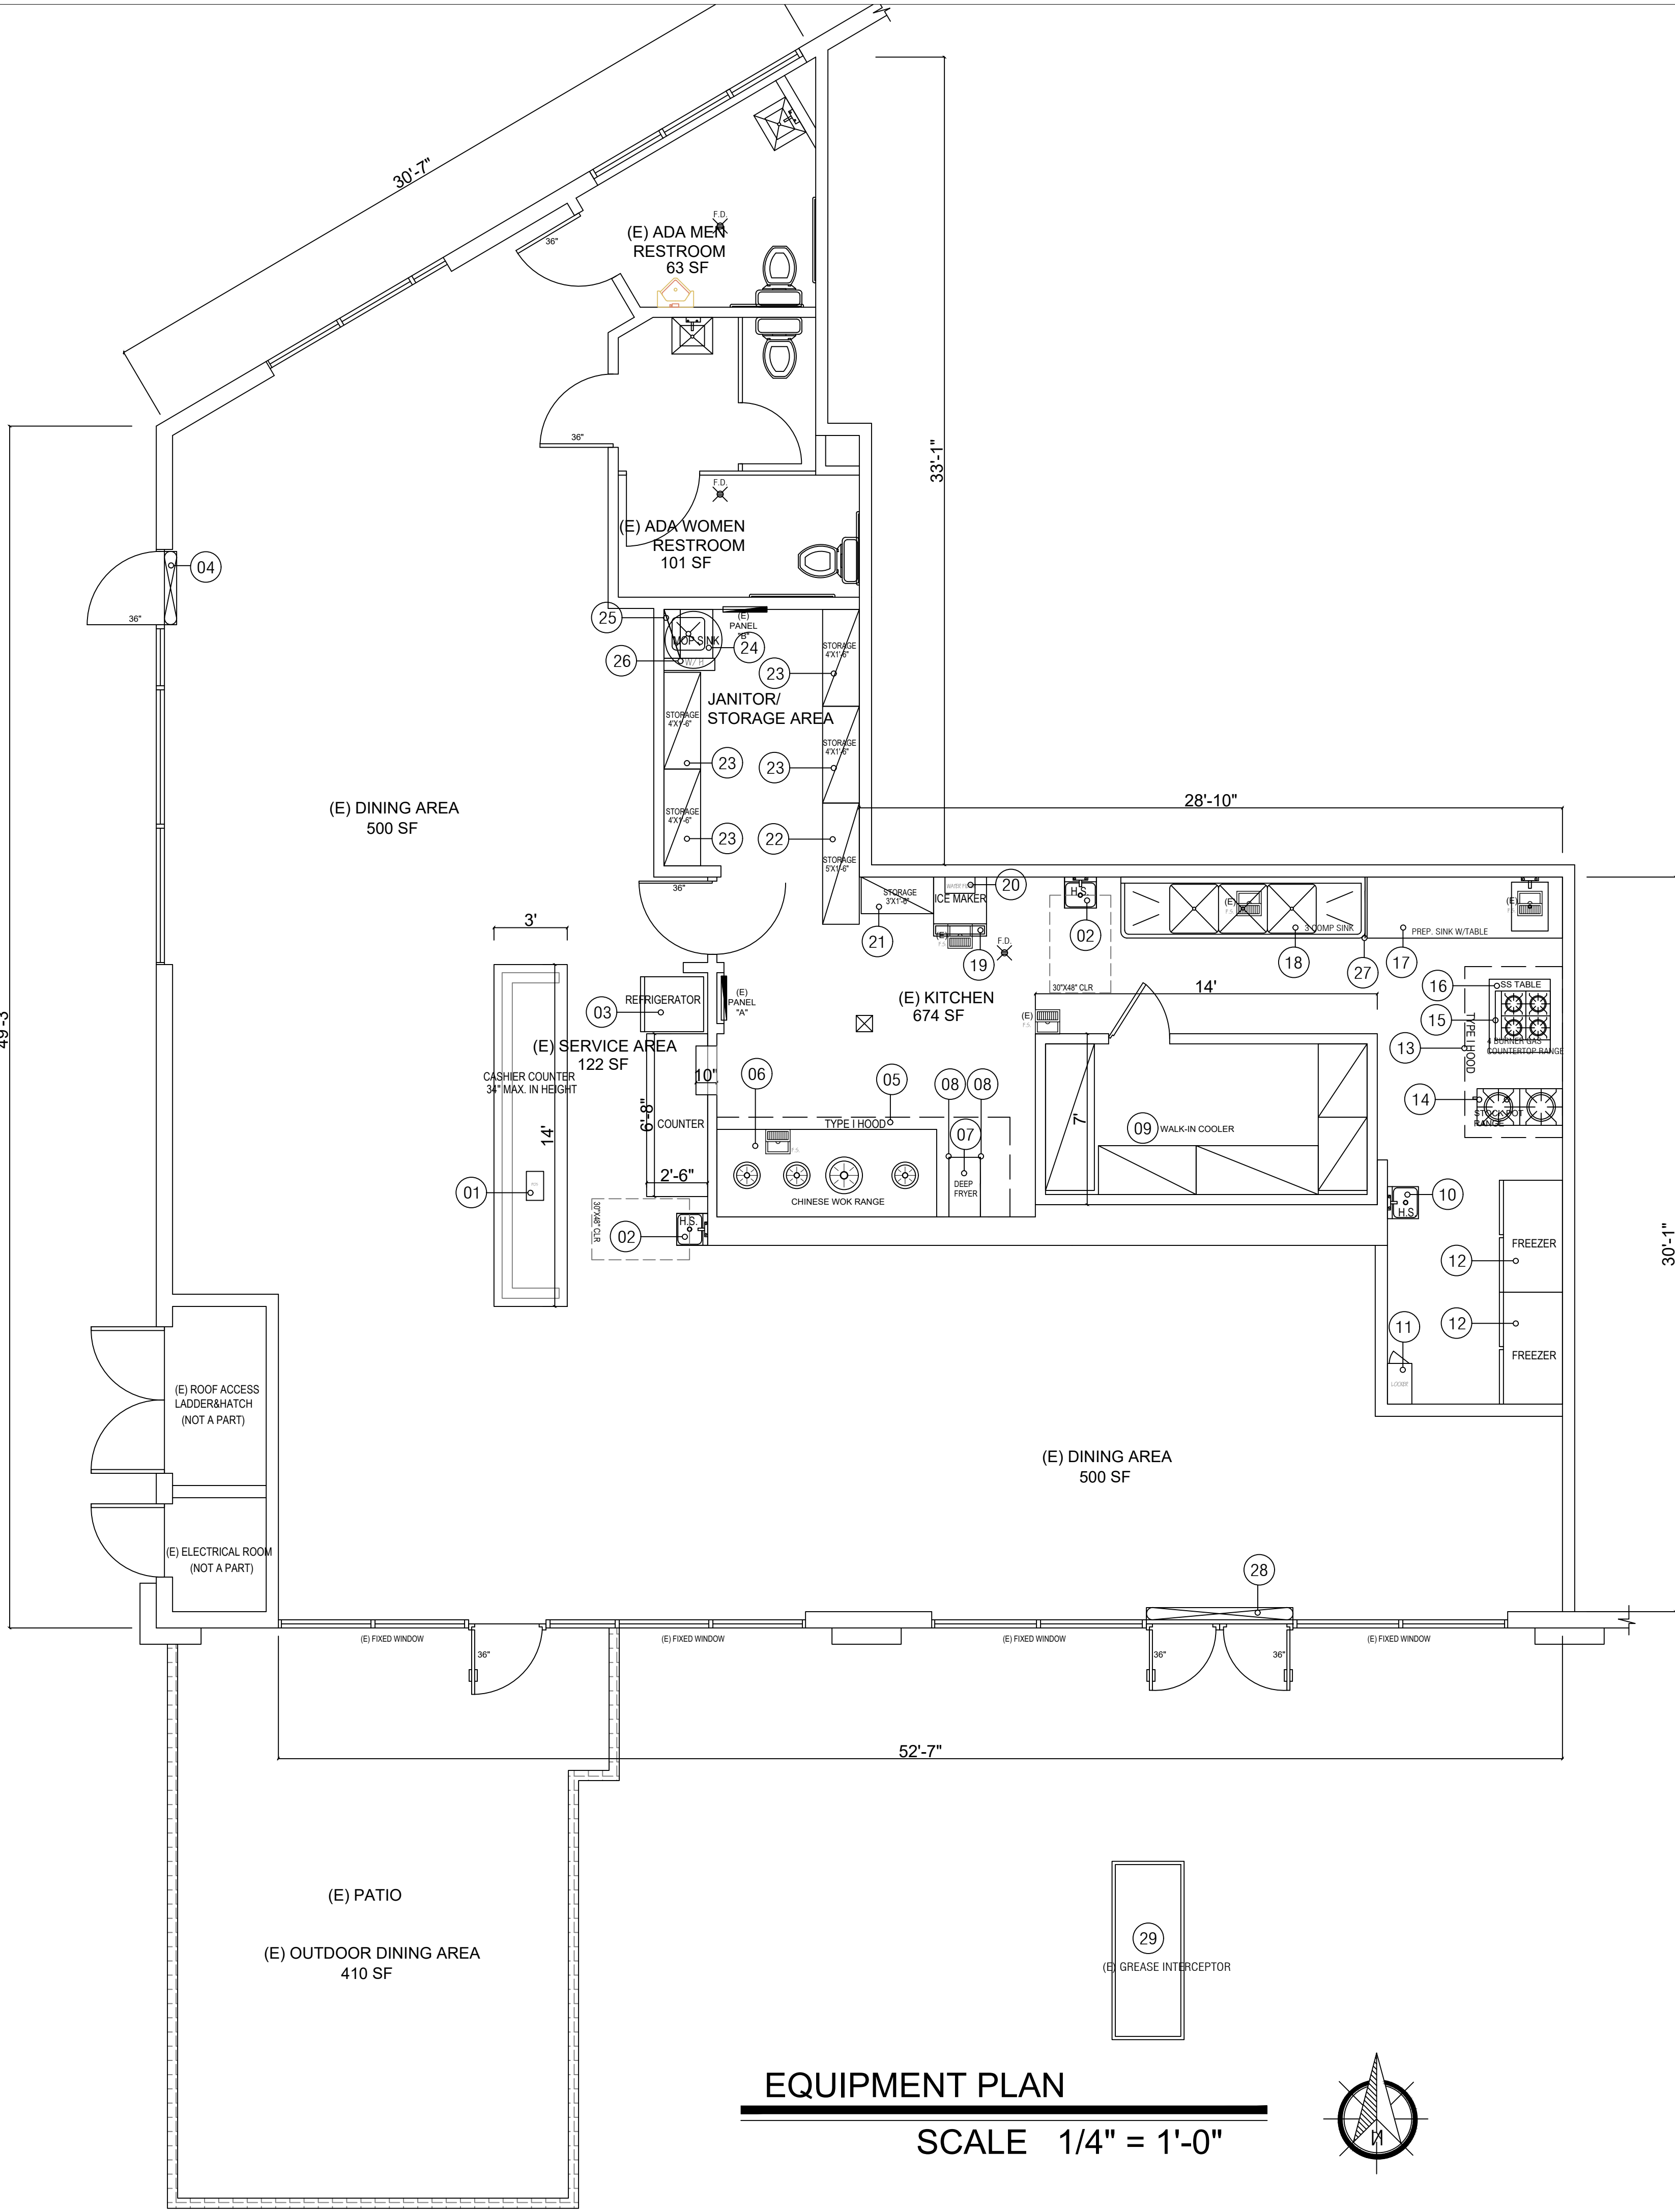

EQUIPMENT PLAN
SCALE 1/4" = 1'-0"

EQUIPMENT SCHEDULE					
ITEM	DESCRIPTION	QTY	MANUFACTURER	MODEL	STATUS
01	ELEC. POS	1	—	—	EXISTING
02	HAND SINK ,WALL-MOUNT W/SPLASH GUARD STAINLESS STEEL/NSF, W/ SOAP & TOWEL DISPENSER OVERALL:15-1/4" W X 15-3/4" D X 14-3/8" H	2	"GSW"	HS-1615S	EXISTING
03	SINGLE GLASS DOOR REFRIGERATOR (W:27"x D:31 1/2"x H:81 1/4") SUPPORTED BY 4" HIGH CASTERS	1	"BLUEAIR"	BKGM23-HC	EXISTING
04	AIR CURTAIN W/ MICRO SWITCH. (WALL- MOUNT)	1	"MARS"	LPV236-1U-0B	EXISTING
05	TYPE I HOOD (12"W X 4'D)	1	"CAPTIVEAIRE"	4824ND-2	EXISTING
06	CHINESE WOK RANGES (108" X 42" X 32"), 440,000 BTU DRAIN TO A FLOOR SINK	1	"ABC RESTAURANT EQUIPMENT"	ABC-4	EXISTING
07	GAS DEEP FRYER (15 3/5"W X 30 1/10"D X 44 2/5"H) SUPPORTED BY 6" CASTERS	1	"ATOSA"	ATFS-50	EXISTING
08	STAINLESS STEEL SPLASH GUARD FOR DEEP DRYER(20.5"W X 18"H)	2	"ASSURE"	190FG1820	EXISTING
09	WALK IN COOLER DRAIN TO A FLOOR SINK	1	"KOLPAK"	—	EXISTING
10	HAND SINK ,WALL-MOUNT W/BACK SPLASH GUARD STAINLESS STEEL/NSF, W/ SOAP & TOWEL DISPENSER OVERALL:15-1/4" W X 15-3/4" D X 14-3/8" H	1	"GSW"	HS-1615W	EXISTING
11	LOCKER (12"W X 20"D X 77"H) SUPPORTED BY 6" HIGH ROUND LEGS	1	"GSW"	EL-5DR	EXISTING
12	REACH-IN 2 DOOR FREEZER (54.1"W X 30.7"D X 81.9"H), WITH 4" CASTERS	2	"COOLER DEPOT"	KF-49B	EXISTING
13	TYPE I HOOD (7"W X 4'D)	1	"CAPTIVEAIRE"	4824ND-2	EXISTING
14	GAS STOCK POT STOVE, 2 BURNERS (18"W X 41.7"D X 22.8"H), WITH 4" LEGS	1	"ATOSA USA"	ATSP-18-2	EXISTING
15	4 BURNER GAS COUNTERTOP RANGE (24"W X 26 13/16"D X 15"H), WITH LEGS	1	"COOKING PERFORMANCE GROUP"	R-CPG-24-NL	EXISTING
16	STAINLESS STEEL WORK TABLE (36"W X 30"D X 34"H), SUPPORTED BY 6" HIGH ROUND LEGS	1	"REGENCY"	600TS3036S	EXISTING
17	PREP. SINK W/TABLE (SINK: 18"W X 24"D X 14"H, TABLE: 96"W X 30"D X 45"H) DRAIN TO A FLOOR SINK	1	"ADVANCE TABCO"	TKMS-308 TA-11L	EXISTING
18	3 COMP SINK W/2 24"x24" DRAINBOARDS W/SPLASH GUARD, SIZE: 103" W X 27"D X 45" H 11 3/4"H BACKSPLASH DRAIN TO A FLOOR SINK	1	"ADVANCE TABCO"	94-3-54-24RL	EXISTING
19	ELEC. SELF CONTAINED CUBE ICE MAKER(24.54"W X 26.27"D X 33"H) SUPPORTED BY 6" HIGH ROUND LEGS DRAIN TO A FLOOR SINK	1	"ICE-O-MATIC"	ICEU220	EXISTING
20	WATER FILTER	1	"PENTAIR"	QC71 HEAD/ 4FC-S F.C	EXISTING
21	STORAGE SHELVING 4 TIER, 18" DEEP 3'x1'-6" (6" ABOVE GROUND, 5' height TOTAL)	1 LOT	"REGENCY"	460EC1836	EXISTING
22	STORAGE SHELVING 4 TIER, 18" DEEP 5'x1'-6" (6" ABOVE GROUND, 5' height TOTAL)	1 LOT	"REGENCY"	460EC1860	EXISTING
23	STORAGE SHELVING 4 TIER, 18" DEEP 4'x1'-6" (6" ABOVE GROUND, 5' height TOTAL)	4 LOT	"REGENCY"	460EC1848	EXISTING
24	MOP SINK (24"W X 24"D X 14"H) DIRECT DRAINAGE	1	"GSW"	SE2424FM	EXISTING
25	SS MOP SINK UTILITY SHELF (24"W X 8"D) WITH MOP/BROOM HOLDERS & RAG HOOKS	1	"REGENCY"	600WSU824	EXISTING
26	GAS TANK WATER HEATER, 81 GAL. 154,000 BTU INDIRECT DRAIN TO FLOOR SINK	1	"AO SMITH"	BTR-154	EXISTING
27	CUSTOM STAINLESS STEEL LEFT/RIGHT SPLASH (30"W X 18"H)	1	CUSTOM	CUSTOM	EXISTING
28	AIR CURTAIN W/ MICRO SWITCH. (WALL- MOUNT)	1	"MARS"	LPV272-1U-0B	EXISTING
29	GREASE INTERCEPTOR	1	—	—	EXISTING

NOTES: ALL EQUIPMENT SHALL BE NSF APPROVED

REVISIONS

PLAN CHECK CORRECTION

R-1

R-2

R-1

R-1

1ST. SUBMITAL:
2ND. SUBMITAL:
3RD. SUBMITAL:

PERMIT#
CITY PLANING:
CITY BUILDING:

TOPWAY ARCHI
DESIGN/BUILD
COMMERCIAL AND RESIDENTIAL
CAROL YN ZENG 626-400-0736

JOYEE'S DUMPLING HOUSE

6011 EL CAJON BLVD STE A


SAN DIEGO, CA 92115

EQUIPMENT PLAN &
EQUIPMENT SCHEDULE

SHEET

A-3

DATE
11/ 6 / 2024

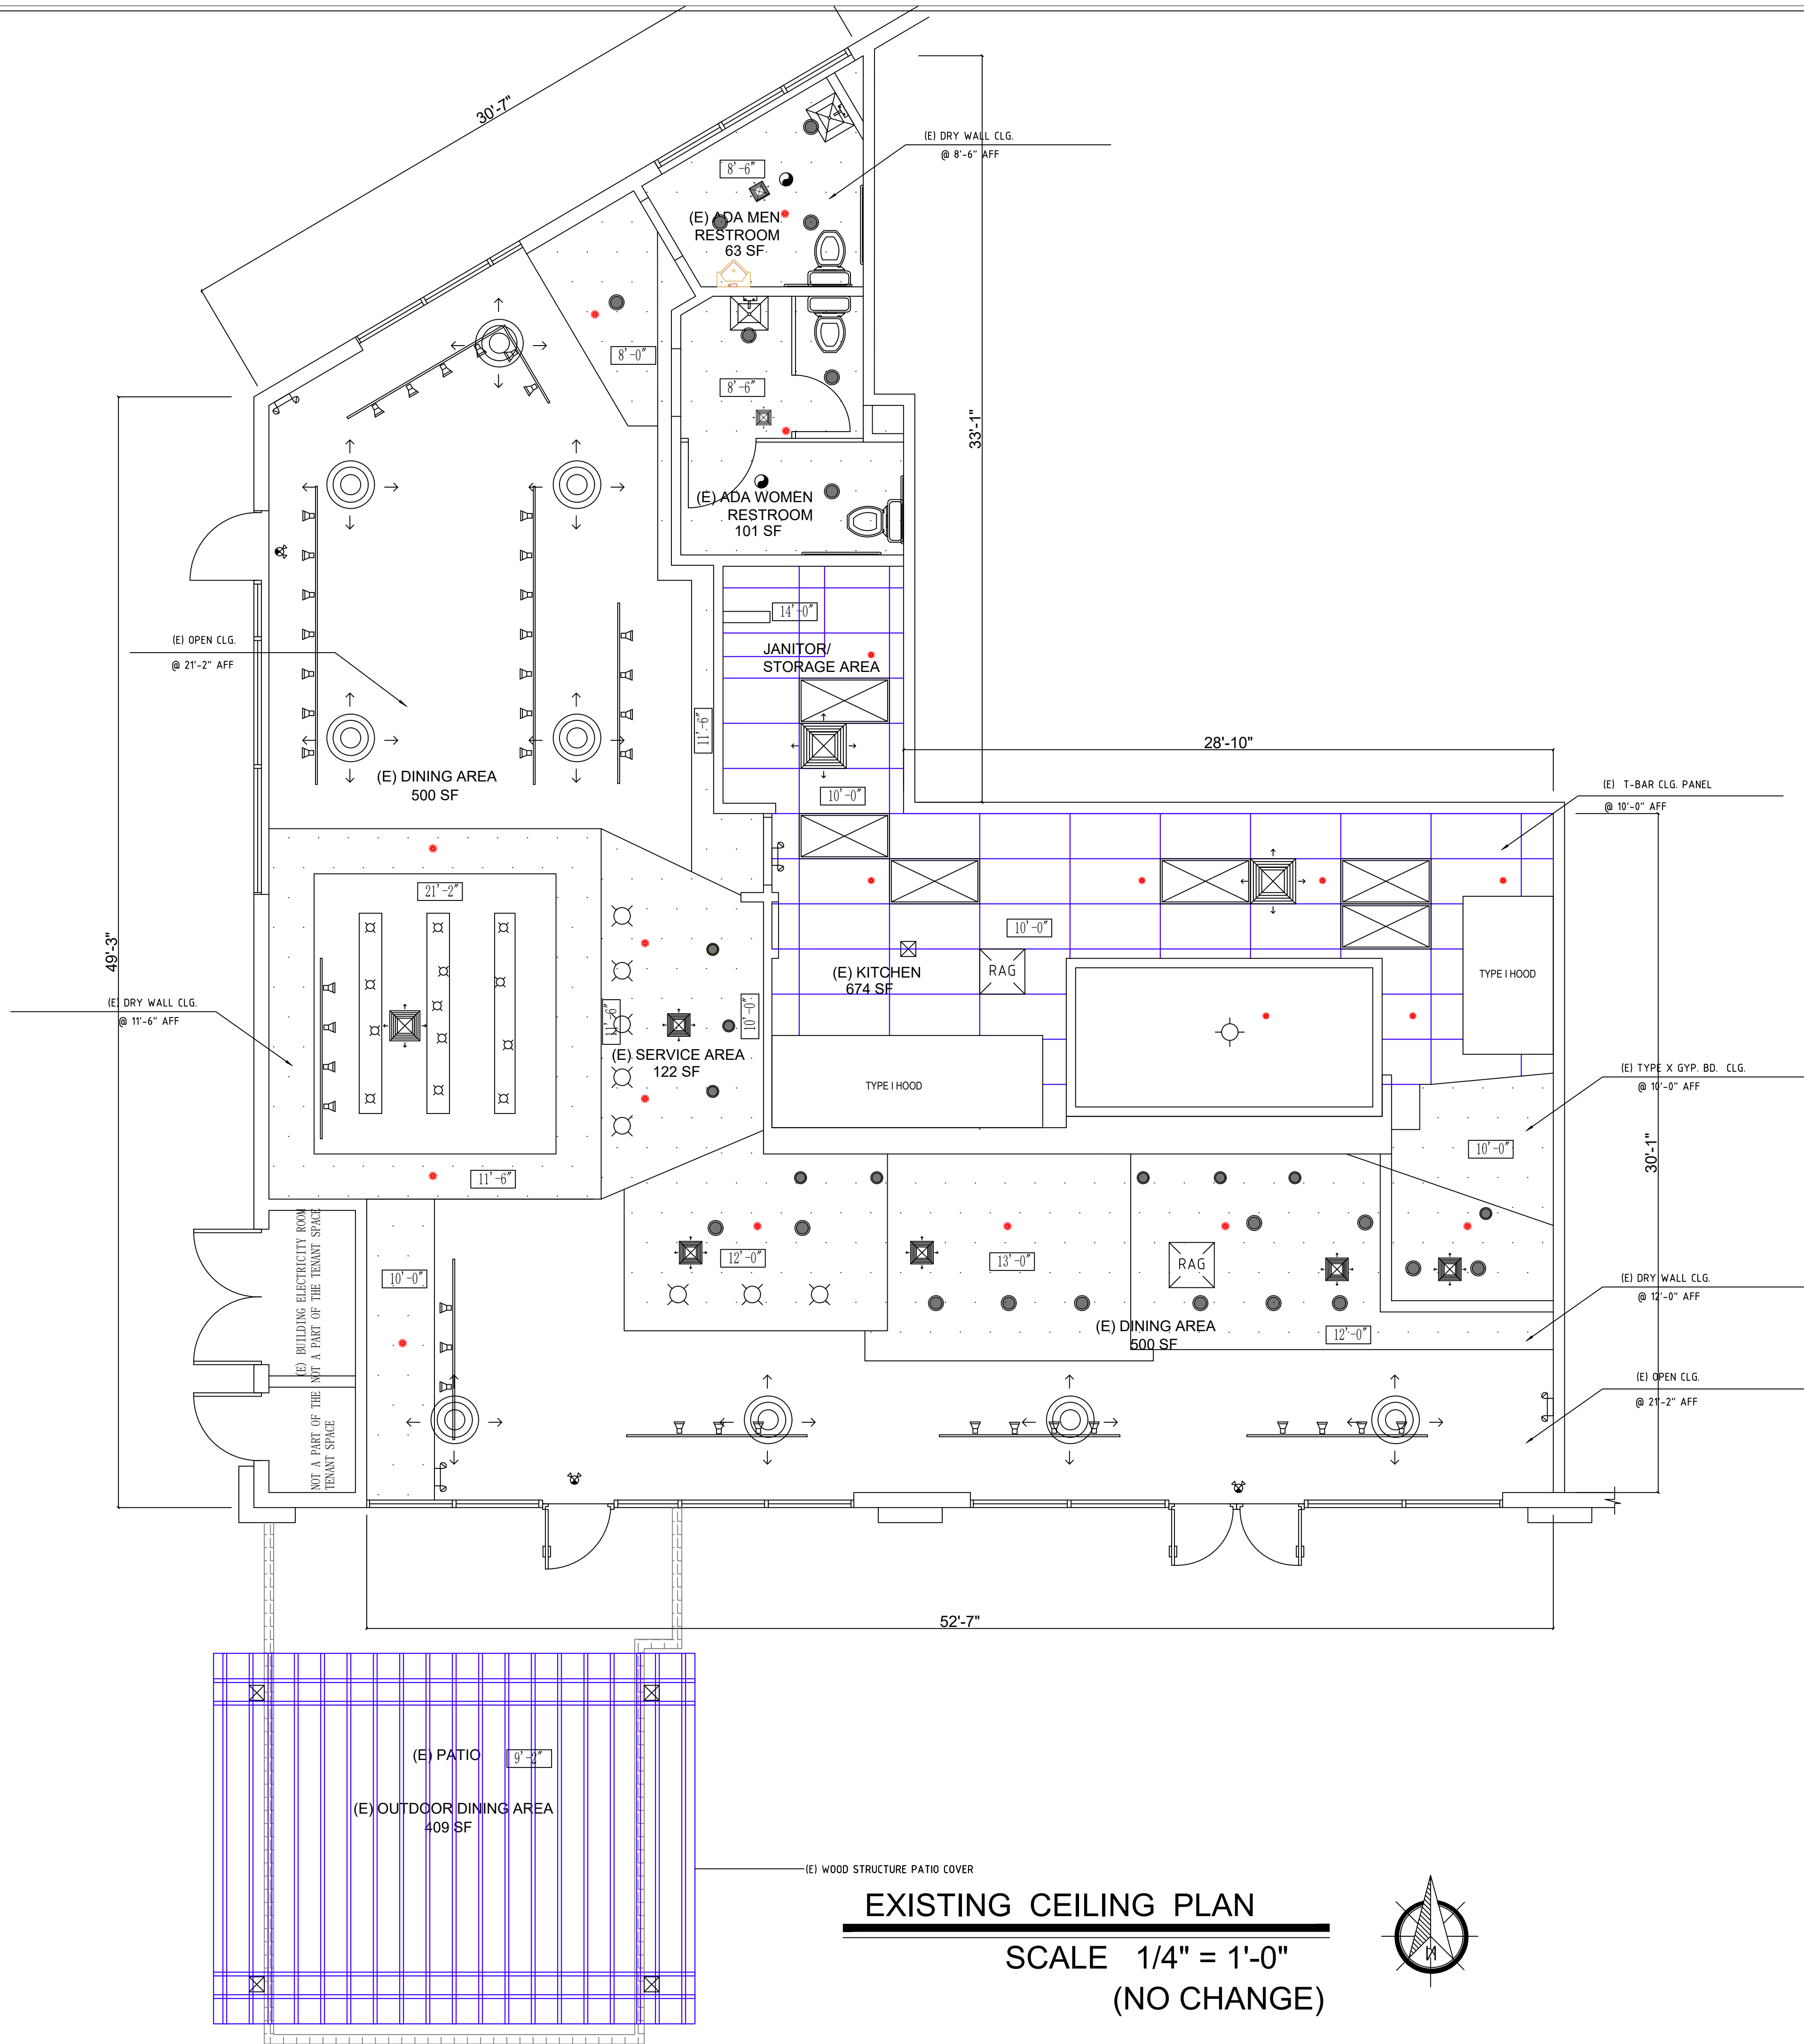

ABBREVIATIONS:

(E) EXISTING
(N) NEW
@ AT
CLG. CEILING

SYMBOLS:

- (E) 6" LED RECESSED FIXTURE
- EXISTING 2' X 4' FLUORESCENT LIGHT
- Ceiling Drop Light Fixture
- Ceiling Light Fixture
- (E) EXHAUST FAN
- EXISTING LED SPOTLIGHT FIXTURE
- (E) AIR SUPPLY
- (E) AIR RETURN
- (E) DINING AREA AIR SUPPLY
- EXIT SIGN WITH EMERGENCY LIGHTS - SEE 2/D3
- EMERGENCY LIGHTS W/ 90 MIN. BATTERY PACK LIGHTS - SEE 2.1/D3
- EXISTING FIRE SPRINKLER
- CEILING HIGH

NOTE:
1. Existing fire sprinkler system, no change.
2. (E) T-bar ceiling material at kitchen:
USG Sheetrock brand lay-in ceiling panels.

REVISIONS

PLAN CHECK CORRECTION	
R-1	
R-2	
R-1	
R-1	

1ST. SUBMITAL:
2ND. SUBMITAL:
3RD. SUBMITAL:

PERMIT#
CITY PLANNING:
CITY BUILDING:

TOPWAY ARCHI
DESIGN/BUILD
COMMERCIAL AND RESIDENTIAL
CAROLYN ZENG 626-400-0736

JOYEE'S DUMPLING HOUSE

6011 EL CAJON BLVD STE A

SAN DIEGO, CA 92115

(E) CEILING PLAN

SHEET

A-4


DATE
11/ 6 / 2024

1. LOCATE CLOSING SPEED FOR ENTRY/ INTERIOR DOORS COMPLY W/DISABLED ACCESS REQ.
2. ON RESTROOM DOOR PROVIDE A "PRIVACY LATCH" COMPLYING WITH LOCAL CODES SEC 11B.213 21 CBC.
3. ON EGRESS DOORS (EXIT ACCESS DOORS) SHALL BE READILY OPENABLE FROM THE EGRESS SIDE WITHOUT THE USE OF A KEY OR SPECIAL KNOWLEDGE OR EFFORT.
4. ENTRANCES, EXITS AND PATHS OF TRAVEL-ENTRANCES, LIMIT THRESHOLD WITH 1/4" VERTICAL OR 1/2" WITH BEVEL MAX. IN DIRECTION OF DOOR TO BE SMOOTH, UNINTERRUPTED SURFACE, ETC.
5. ACCESSIBLE SIGNAGE AS PER STATE & LOCAL CODES.
6. MAXIMUM EFFORT TO OPERATE DOORS SHALL NOT EXCEED 5 POUNDS FOR EXTERIOR DOORS AND INTERIOR DOORS, SUCH PULL OR PUSH EFFORT BEING APPLIED AT RIGHT ANGLES TO HINGED DOORS AND AT THE CENTER PLACE OF SLIDING OR FOLDING DOORS COMPENSATING DEVICES OR AUTOMATIC DOOR OPERATORS MAY BE UTILIZED TO MEET THE ABOVE STANDARDS. WHEN FIRE DOORS ARE REQUIRED, THE MAXIMUM EFFORT TO OPERATE THE DOOR SHALL BE INCREASED TO THE MINIMUM ALLOWABLE BY THE APPROPRIATE ADMINISTRATIVE AUTHORITY, NOT TO EXCEED 15 POUNDS.
7. DOOR OPERABLE PART SHALL BE MOUNTED AT 34" TO 44".
8. MAXIMUM EFFORT TO OPERATE DOORS SHALL NOT EXCEED 5 POUNDS.
9. THE MINIMUM CLEAR OPENING HEIGHT OF DOORS SHALL NOT BE LESS THAN 80 INCHES.

Architectural drawing of a window unit. The drawing shows a side elevation of a window assembly. On the left, a vertical dimension line indicates a total height of 10' and a height of 7' for the main window pane. Below the main pane, a smaller section is dimensioned as 3'-6" high. The main window pane is labeled 'TEMP GLASS' and features a diagonal line pattern. To the right of the main pane, there are three smaller rectangular sections, each also labeled 'TEMP GLASS' and featuring a diagonal line pattern. The bottom of the drawing shows a horizontal dimension line indicating a width of 3'. A vertical dimension line on the left side of the main pane indicates a height of 10'.

3'-0" x 7'-0" DOOR

(D) = 60" MAX AFF TO BOT/BASELINE OF HIGHEST LINE OF RAISED CHARACTER, 48" MIN TO BASELINE OF LOWEST BRAILLE CELLS

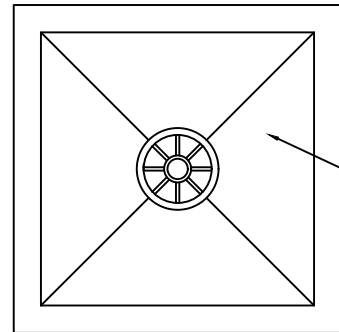


RAIN TO CLEAN DOME DRAINER


MOVABLE GRATE FOR ACCESS TO CLEAN DOME DRAINER

INDIRECT DRAIN PIPE W/1" AIR GAP

FLOOR CONTRACTOR TO GROUT-IN GAP BETWEEN SINK AND FLOOR

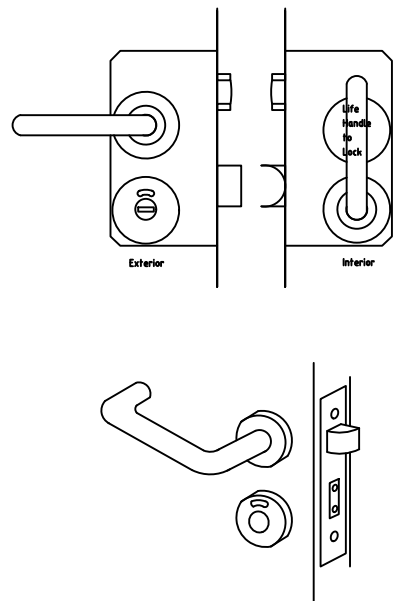

HAND ACTIVATED DOOR
OPENING HARDWARE SHALL BE
CENTERED BETWEEN 30" & 44"
ABOVE THE FLOOR. AND SHALL BE A
TYPE (SHAPE) THAT IS EASY TO OPEN
WITH ONE HAND AND DOES NOT
REQUIRE TIGHT GRASPING, TIGHT
PINCHING OR TWISTING OF THE WRIST
TO OPERATE.

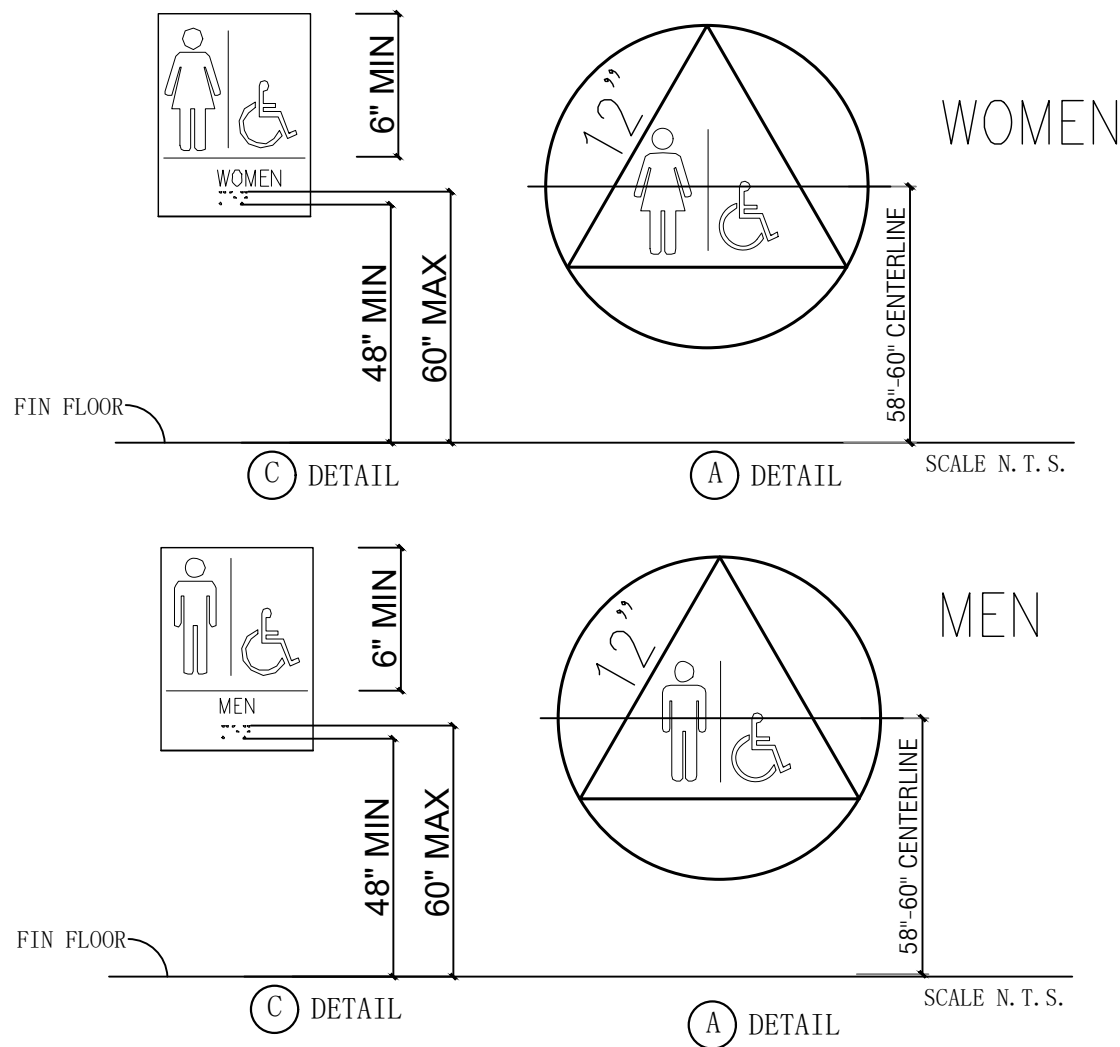

SCALE
NTS

SCALE (2)
M.T.C.

Y PLANING:
Y BUILDING:


DESIGN/BUILD
COMMERCIAL AND RESIDENTIAL
CAROLYN ZENG 626-400-0736

SAN DIEGO, CA 92115


DETAIL 1

D-1


DATE
11/ 6 / 2024

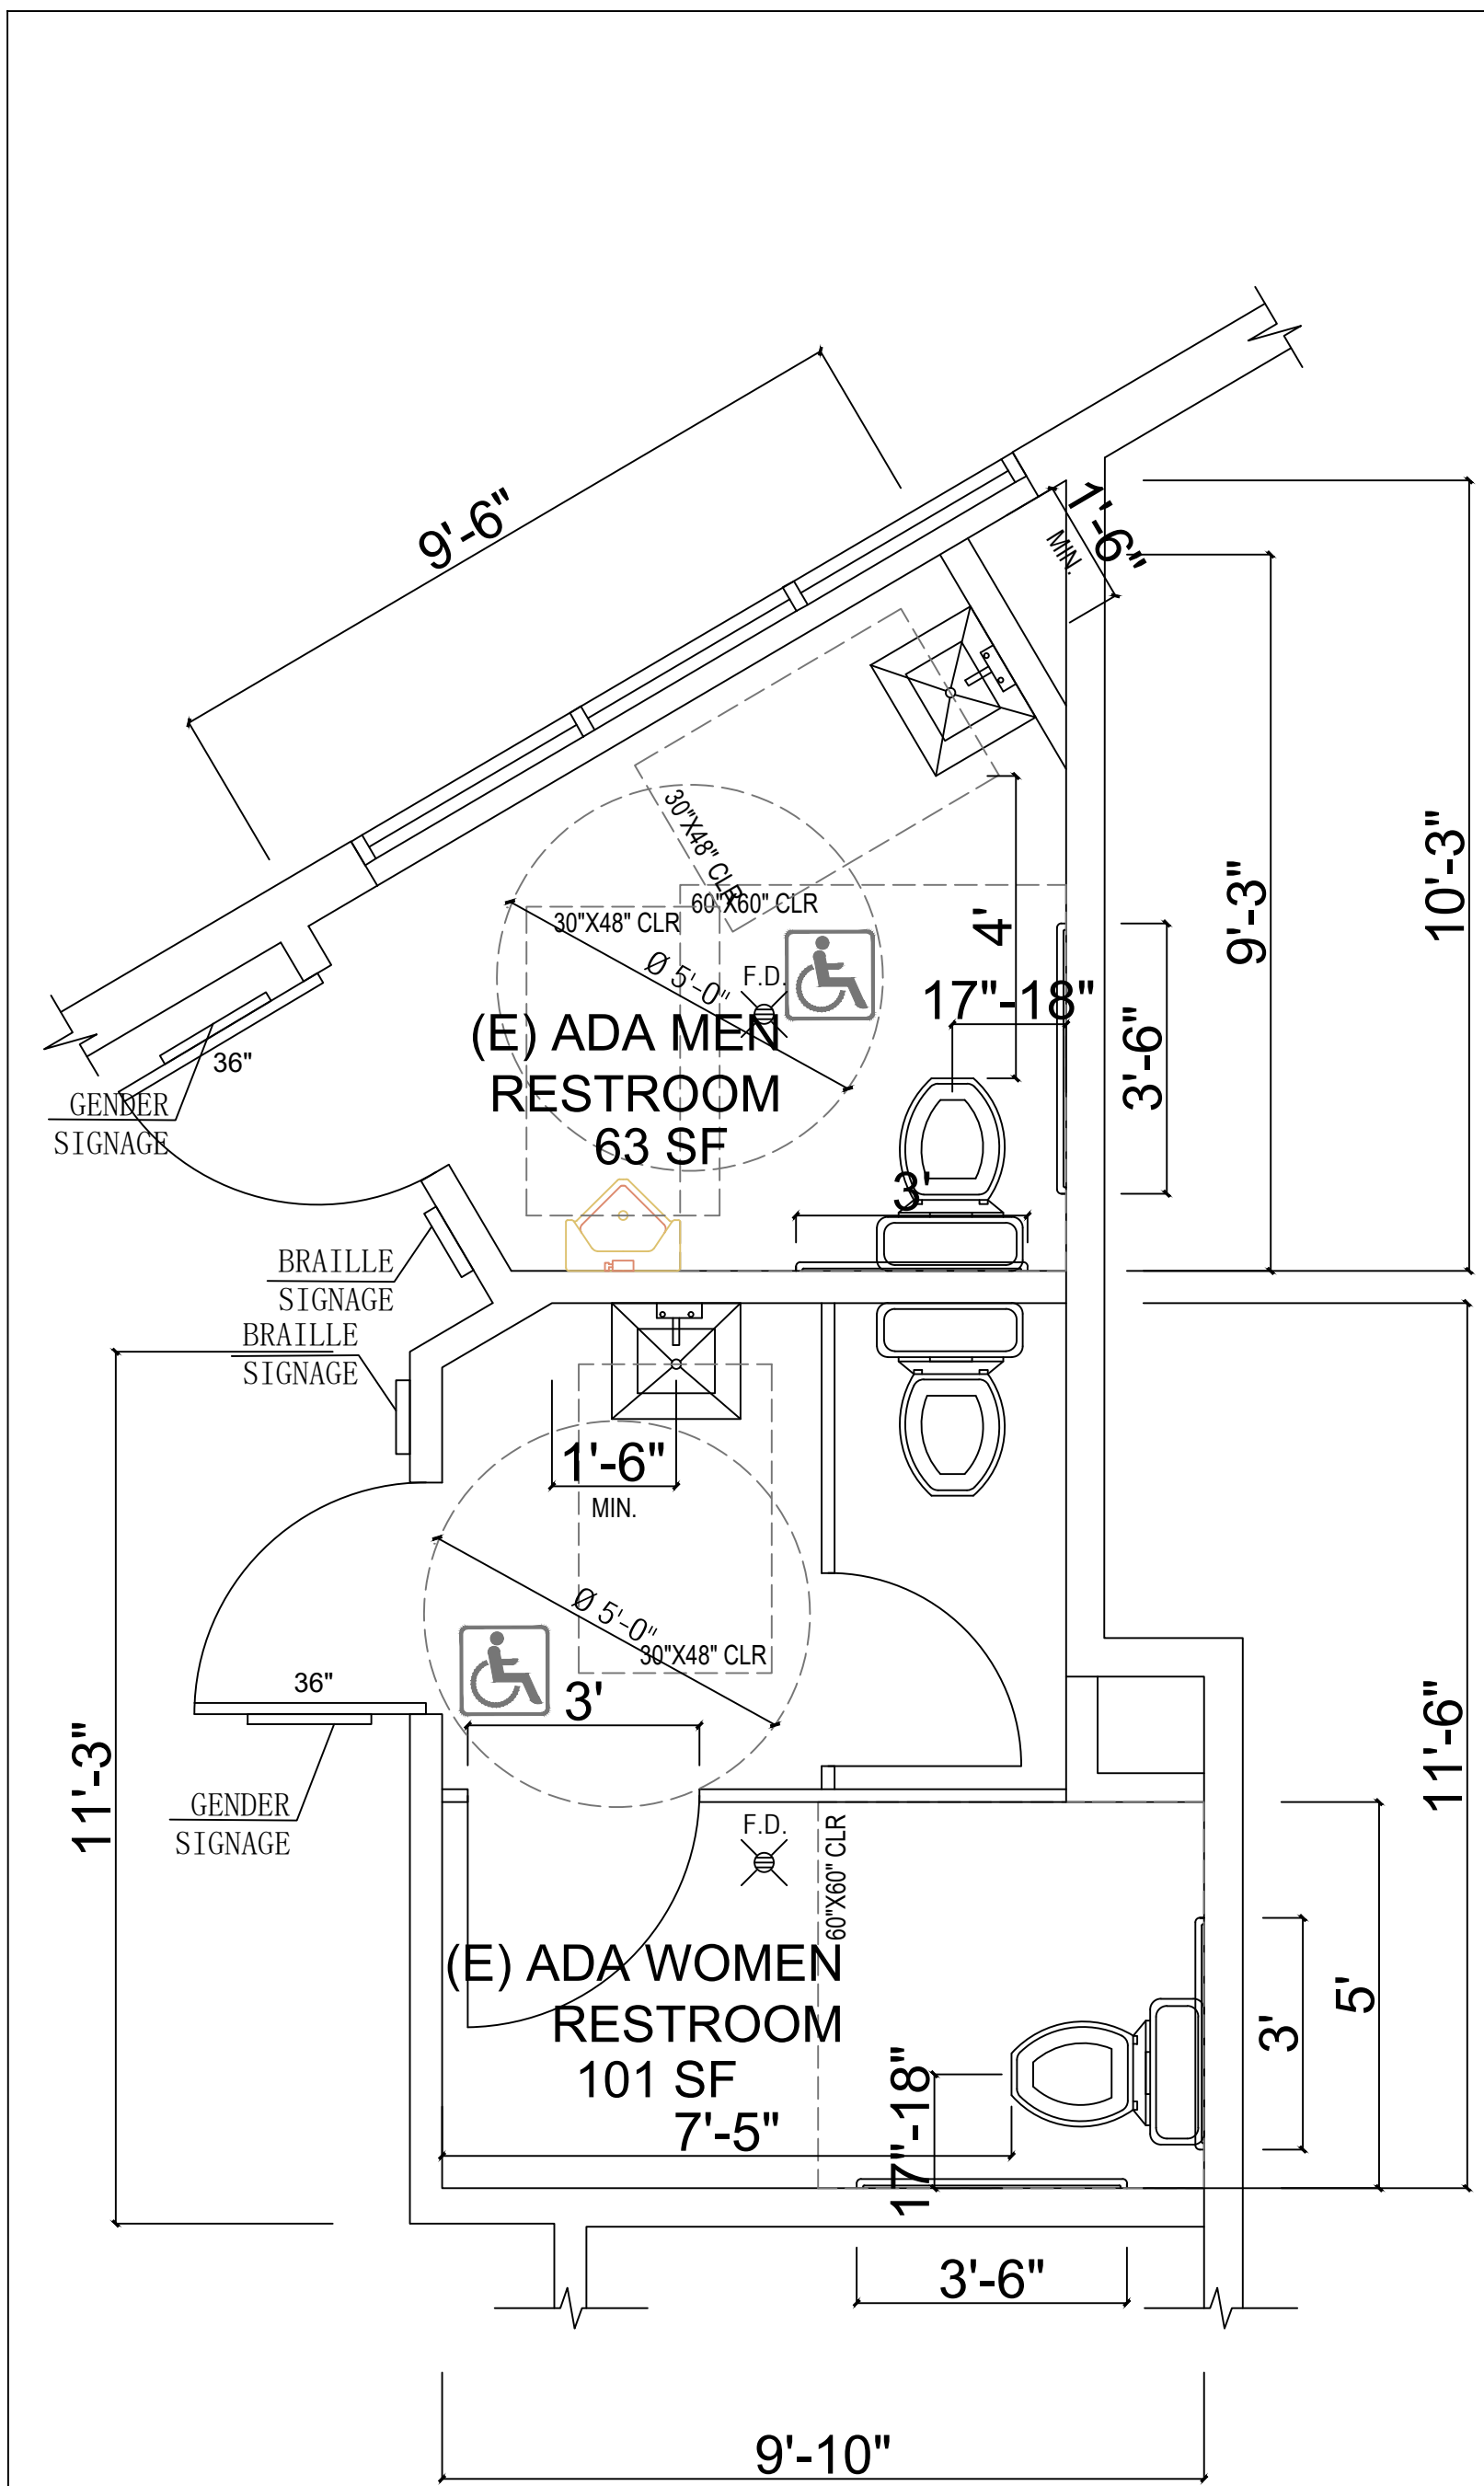


(E) RESTROOM PLAN VIEW
SCALE N. T. S.

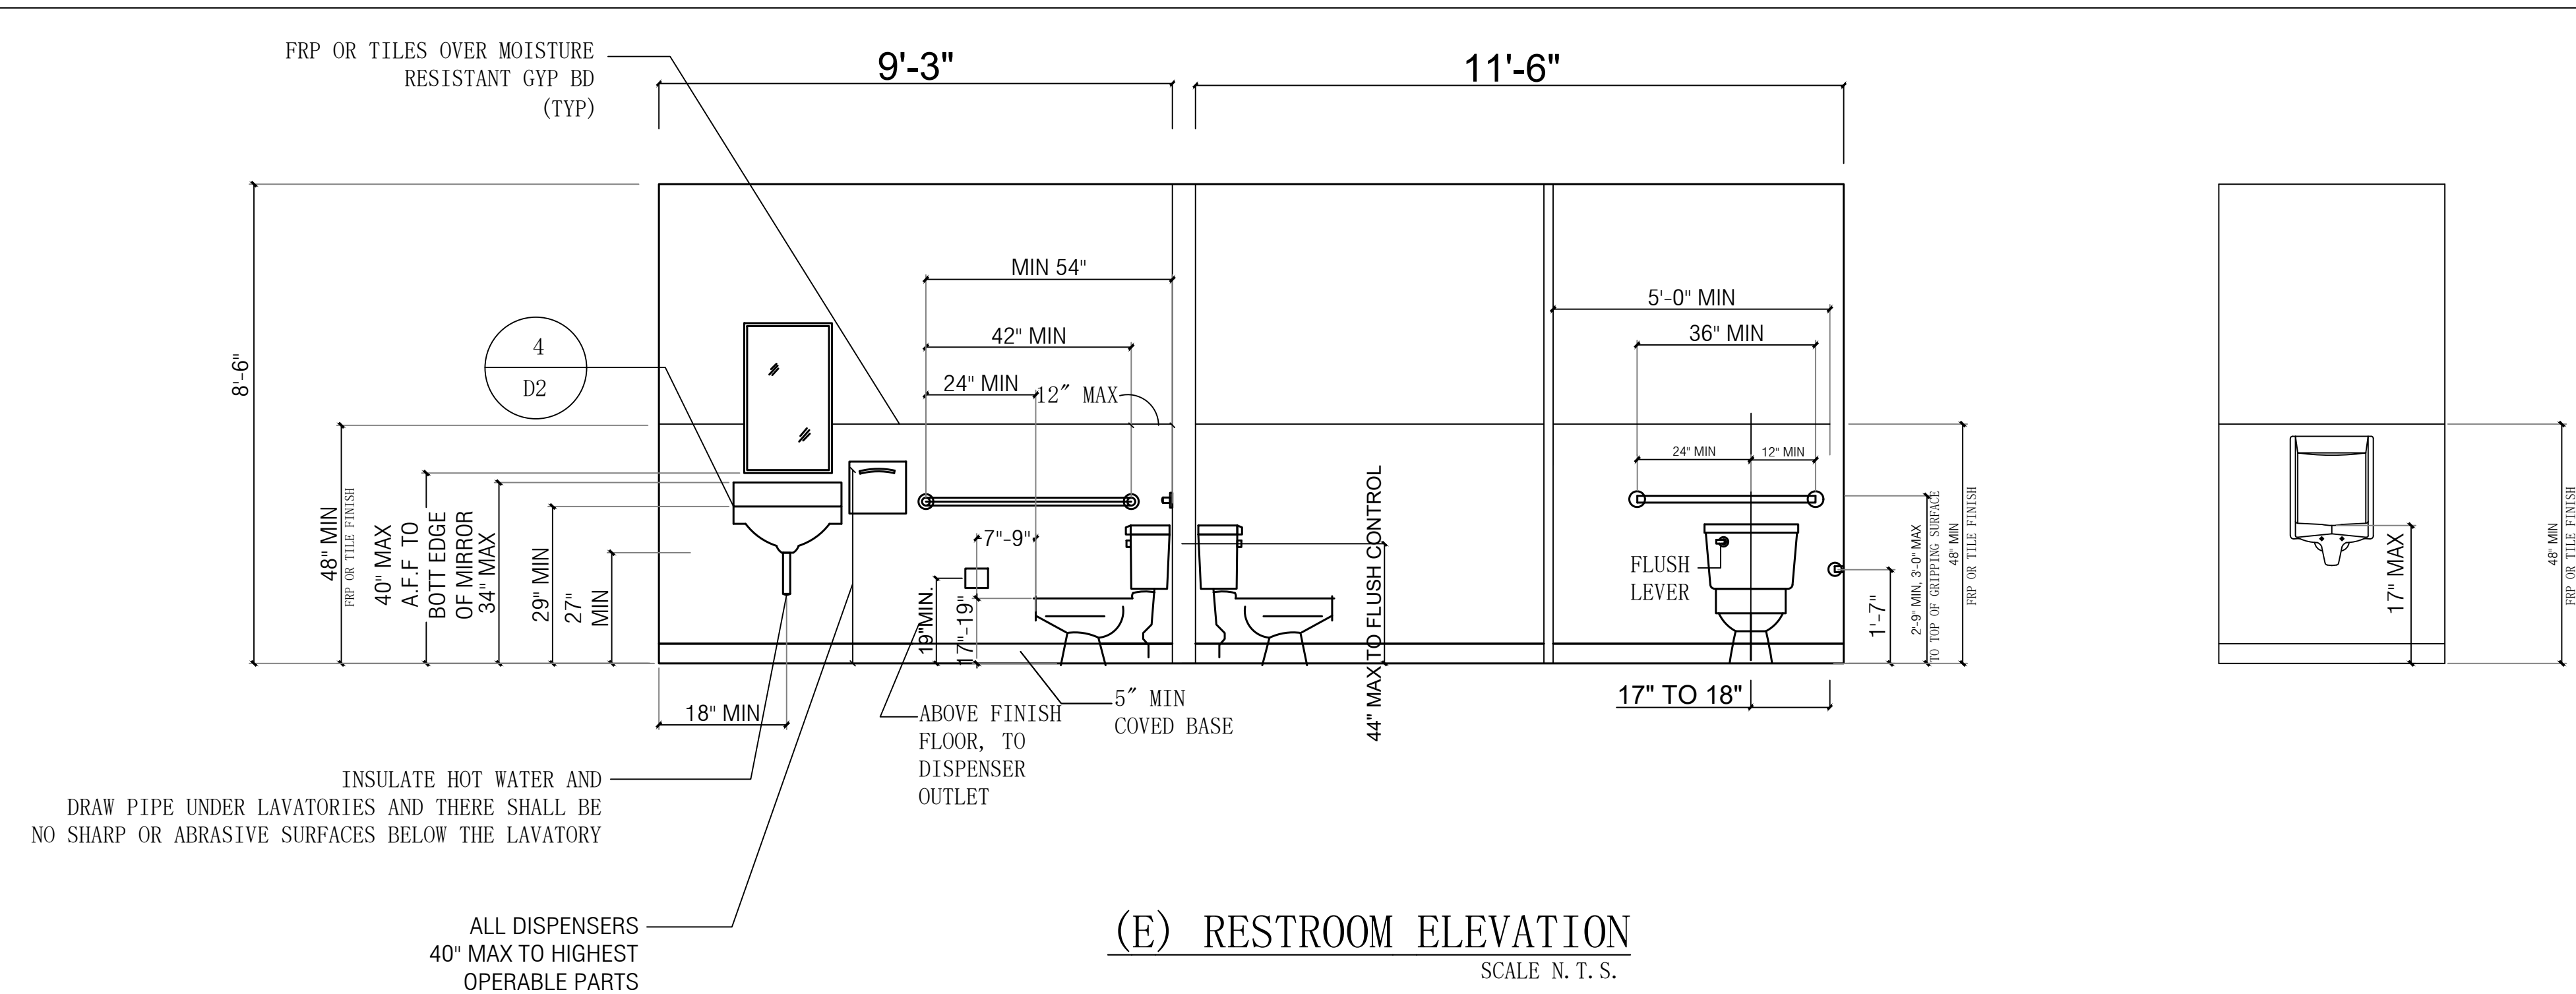

(E) RESTROOM ELEVATION
SCALE N. T. S.

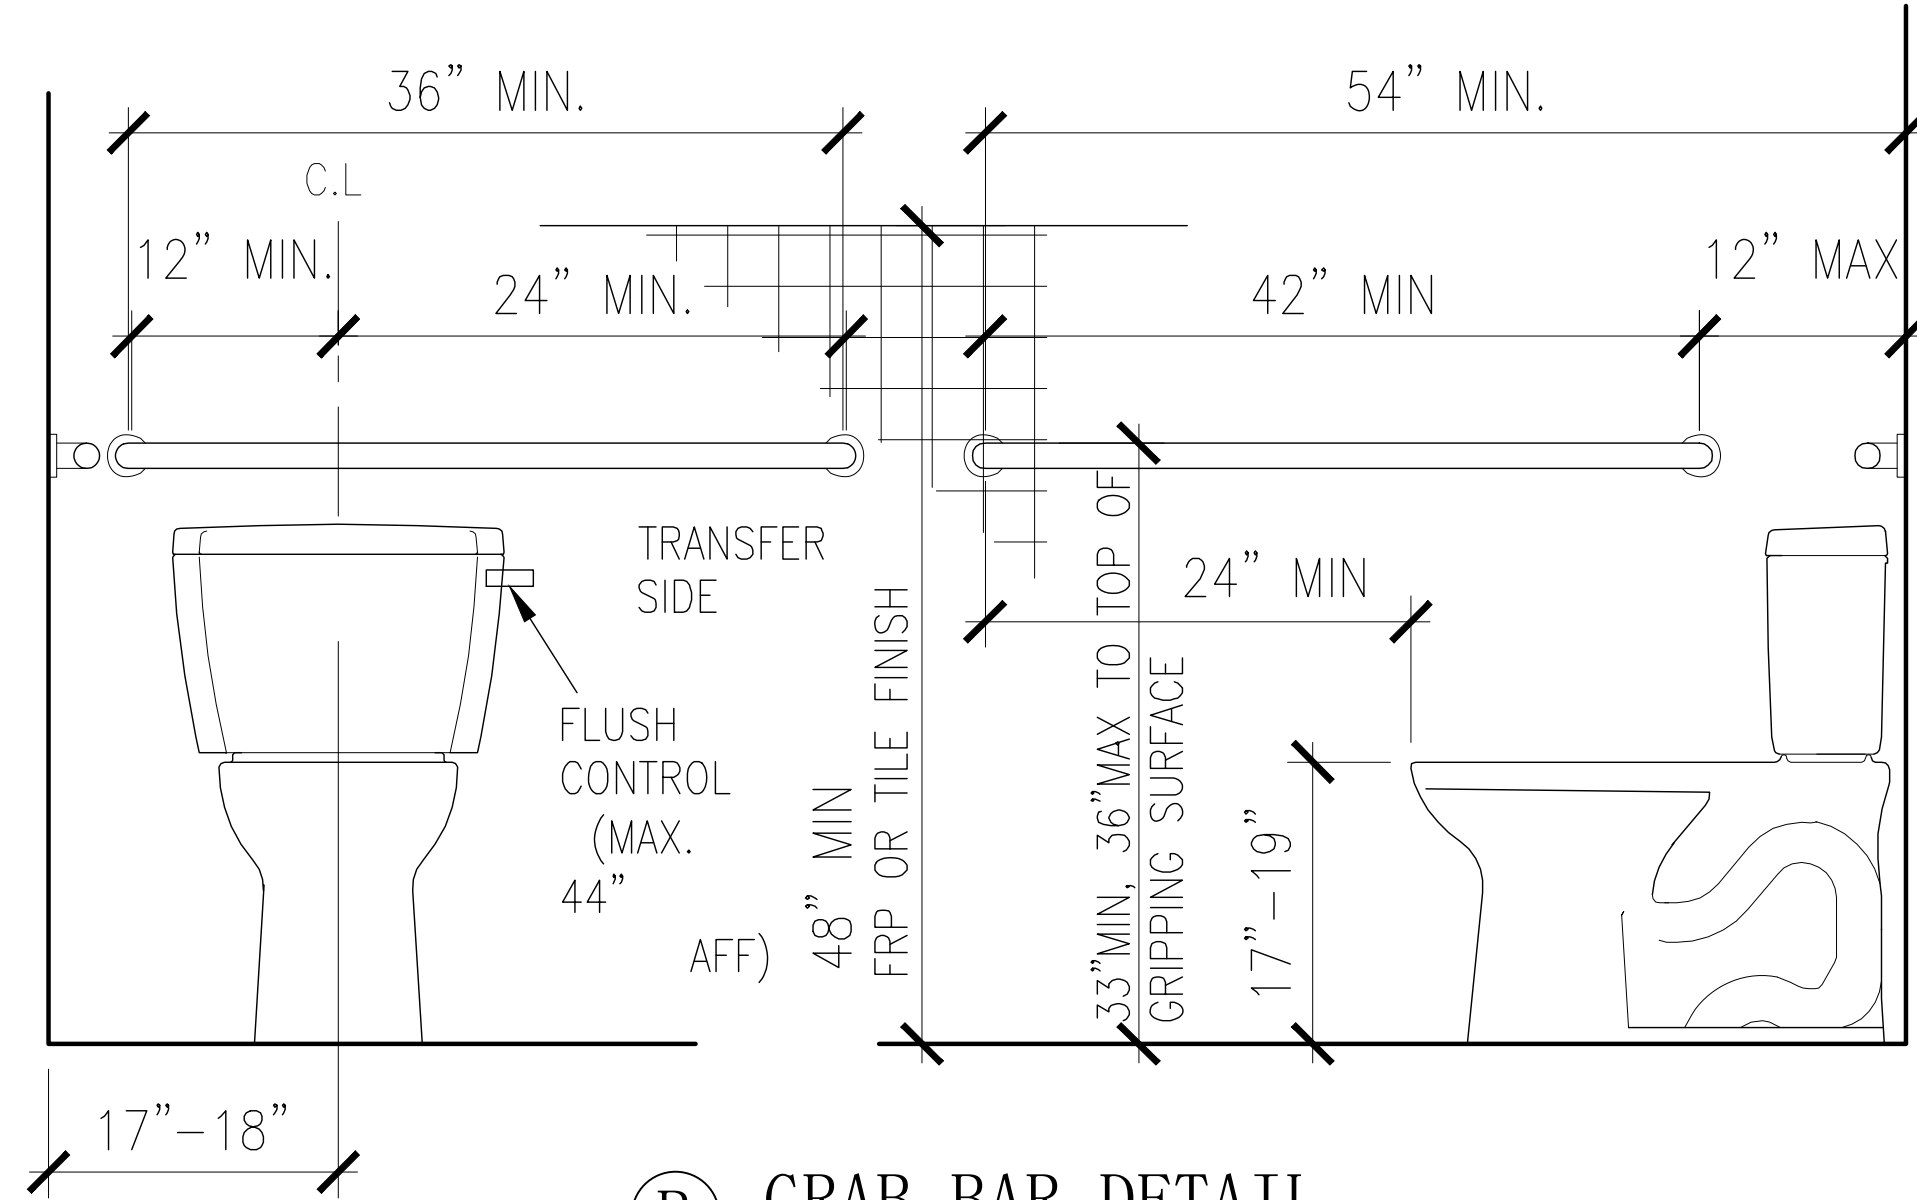

(B) GRAB BAR DETAIL
SCALE N. T. S.

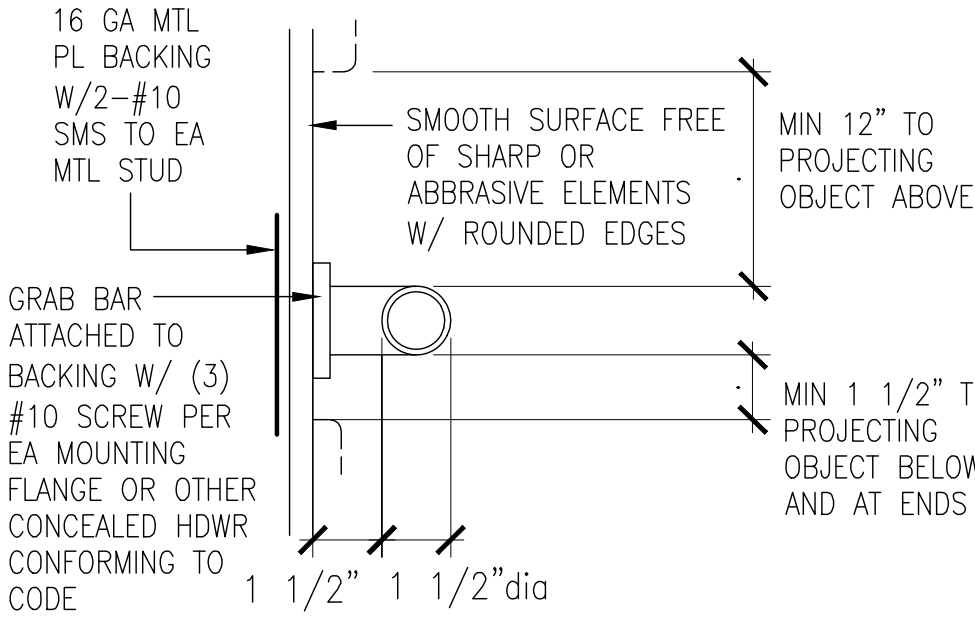


ALLOWABLE STRESS SHALL NOT BE EXCEEDED FOR MATERIAL USED WHEN A VERTICAL OR HORIZONTAL FORCE OF 250 POUND IS APPLIED AT ANY POINT ON THE GRAB BAR, FASTNER, MOUNTING DEVICE, OR SUPPORTING STRUCTURE.

GRAB BAR STRUCT STRENGTH REQ' MT
SCALE N. T. S.


1 (E) ADA RESTROOM DETAILS

NOTE:
Toilet room floors shall have a smooth, hard, nonabsorbent surface such as portland cement, concrete, ceramic tile or other approved material which extend upward onto the walls at least 4". Walls within 24" of the service sinks, water closets and urinals shall be similarly finished to a height of 48" and, except for structural elements, the materials used in such walls shall be type which is not adversely affected by moisture. Lavatory tailpipe and hot water lines shall be insulated or covered per CBC 11B-606.5

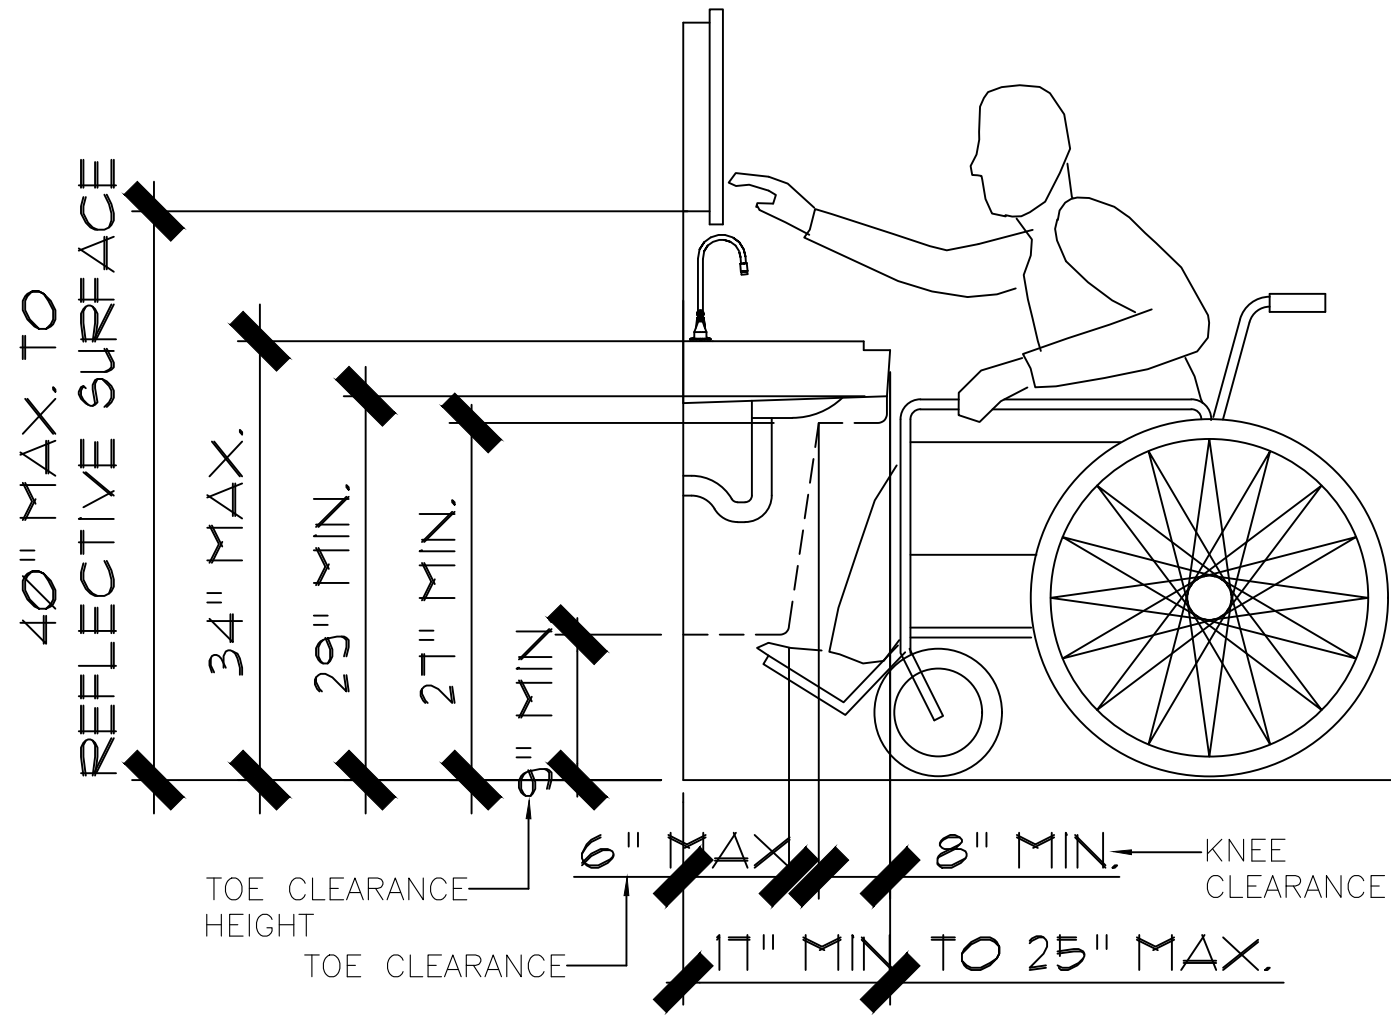


SINK DETAIL

SCALE
N.T.S. 4

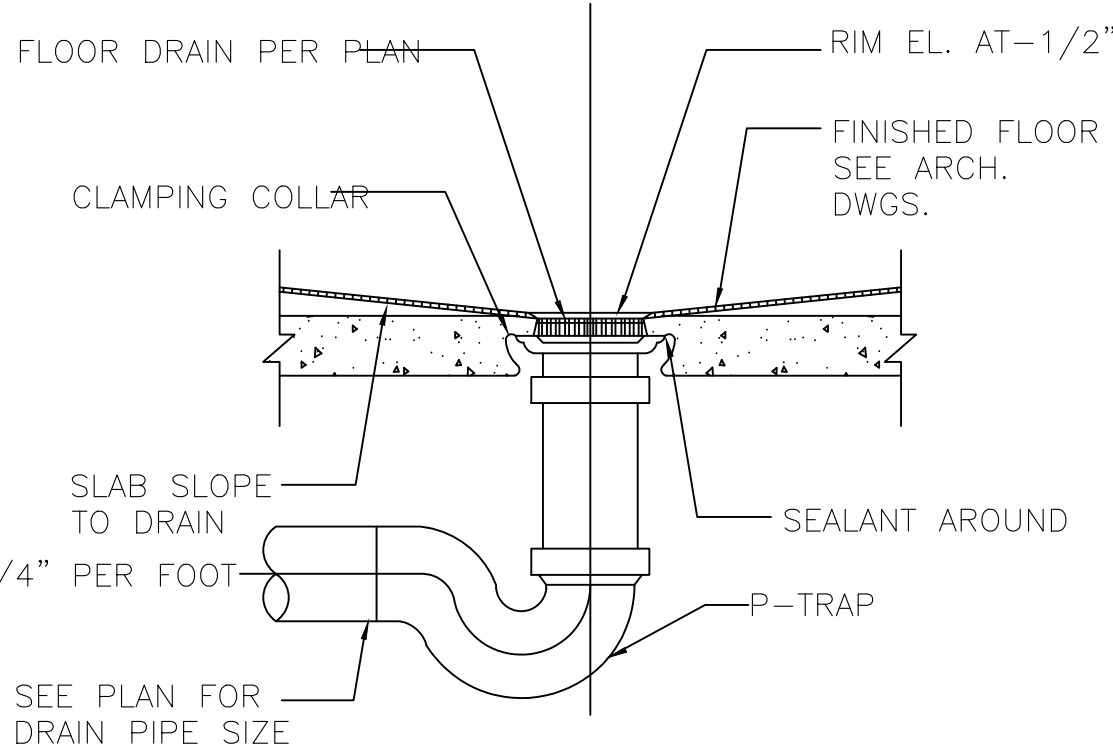

FLOOR DRAIN DETAIL

SCALE
N.T.S. 3

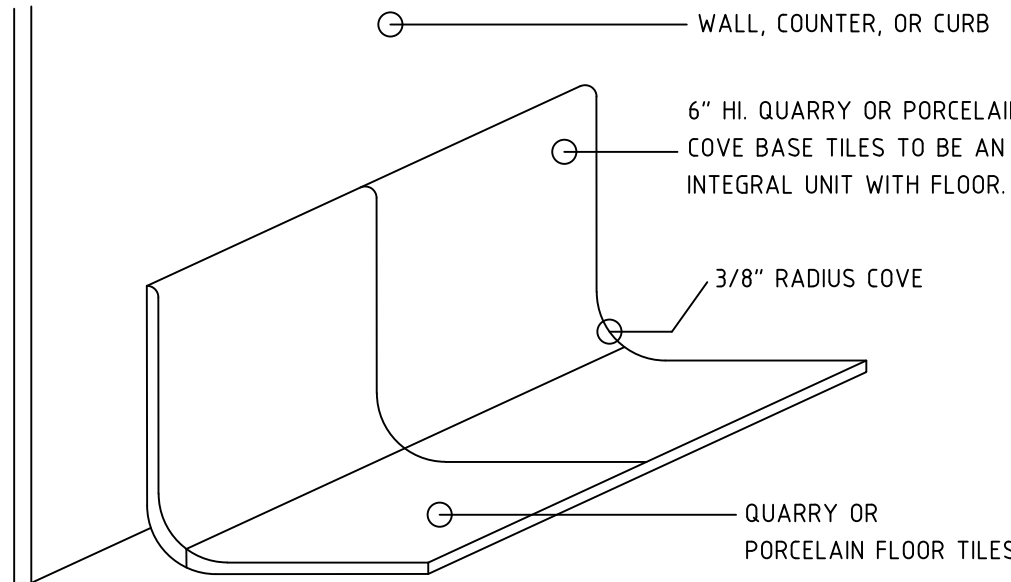

BASE DETAIL




SCALE
N.T.S. 2

REVISIONS	
PLAN CHECK CORRECTION	
R-1	
R-2	
R-1	
R-1	
1ST. SUBMITAL:	
2ND. SUBMITAL:	
3RD. SUBMITAL:	
PERMIT#	
CITY PLANING:	
CITY BUILDING:	
TOPWAY ARCHI	
DESIGN/BUILD	
COMMERCIAL AND RESIDENTIAL	
CAROLYN ZENG 626-400-0736	

JOYEE'S DUMPLING HOUSE	6011 EL CAJON BLVD STE A	SAN DIEGO, CA 92115	
------------------------	--------------------------	---------------------	--

DETAIL 2			
----------	--	--	--

SHEET	
D-2	
DATE	
11/ 6 / 2024	

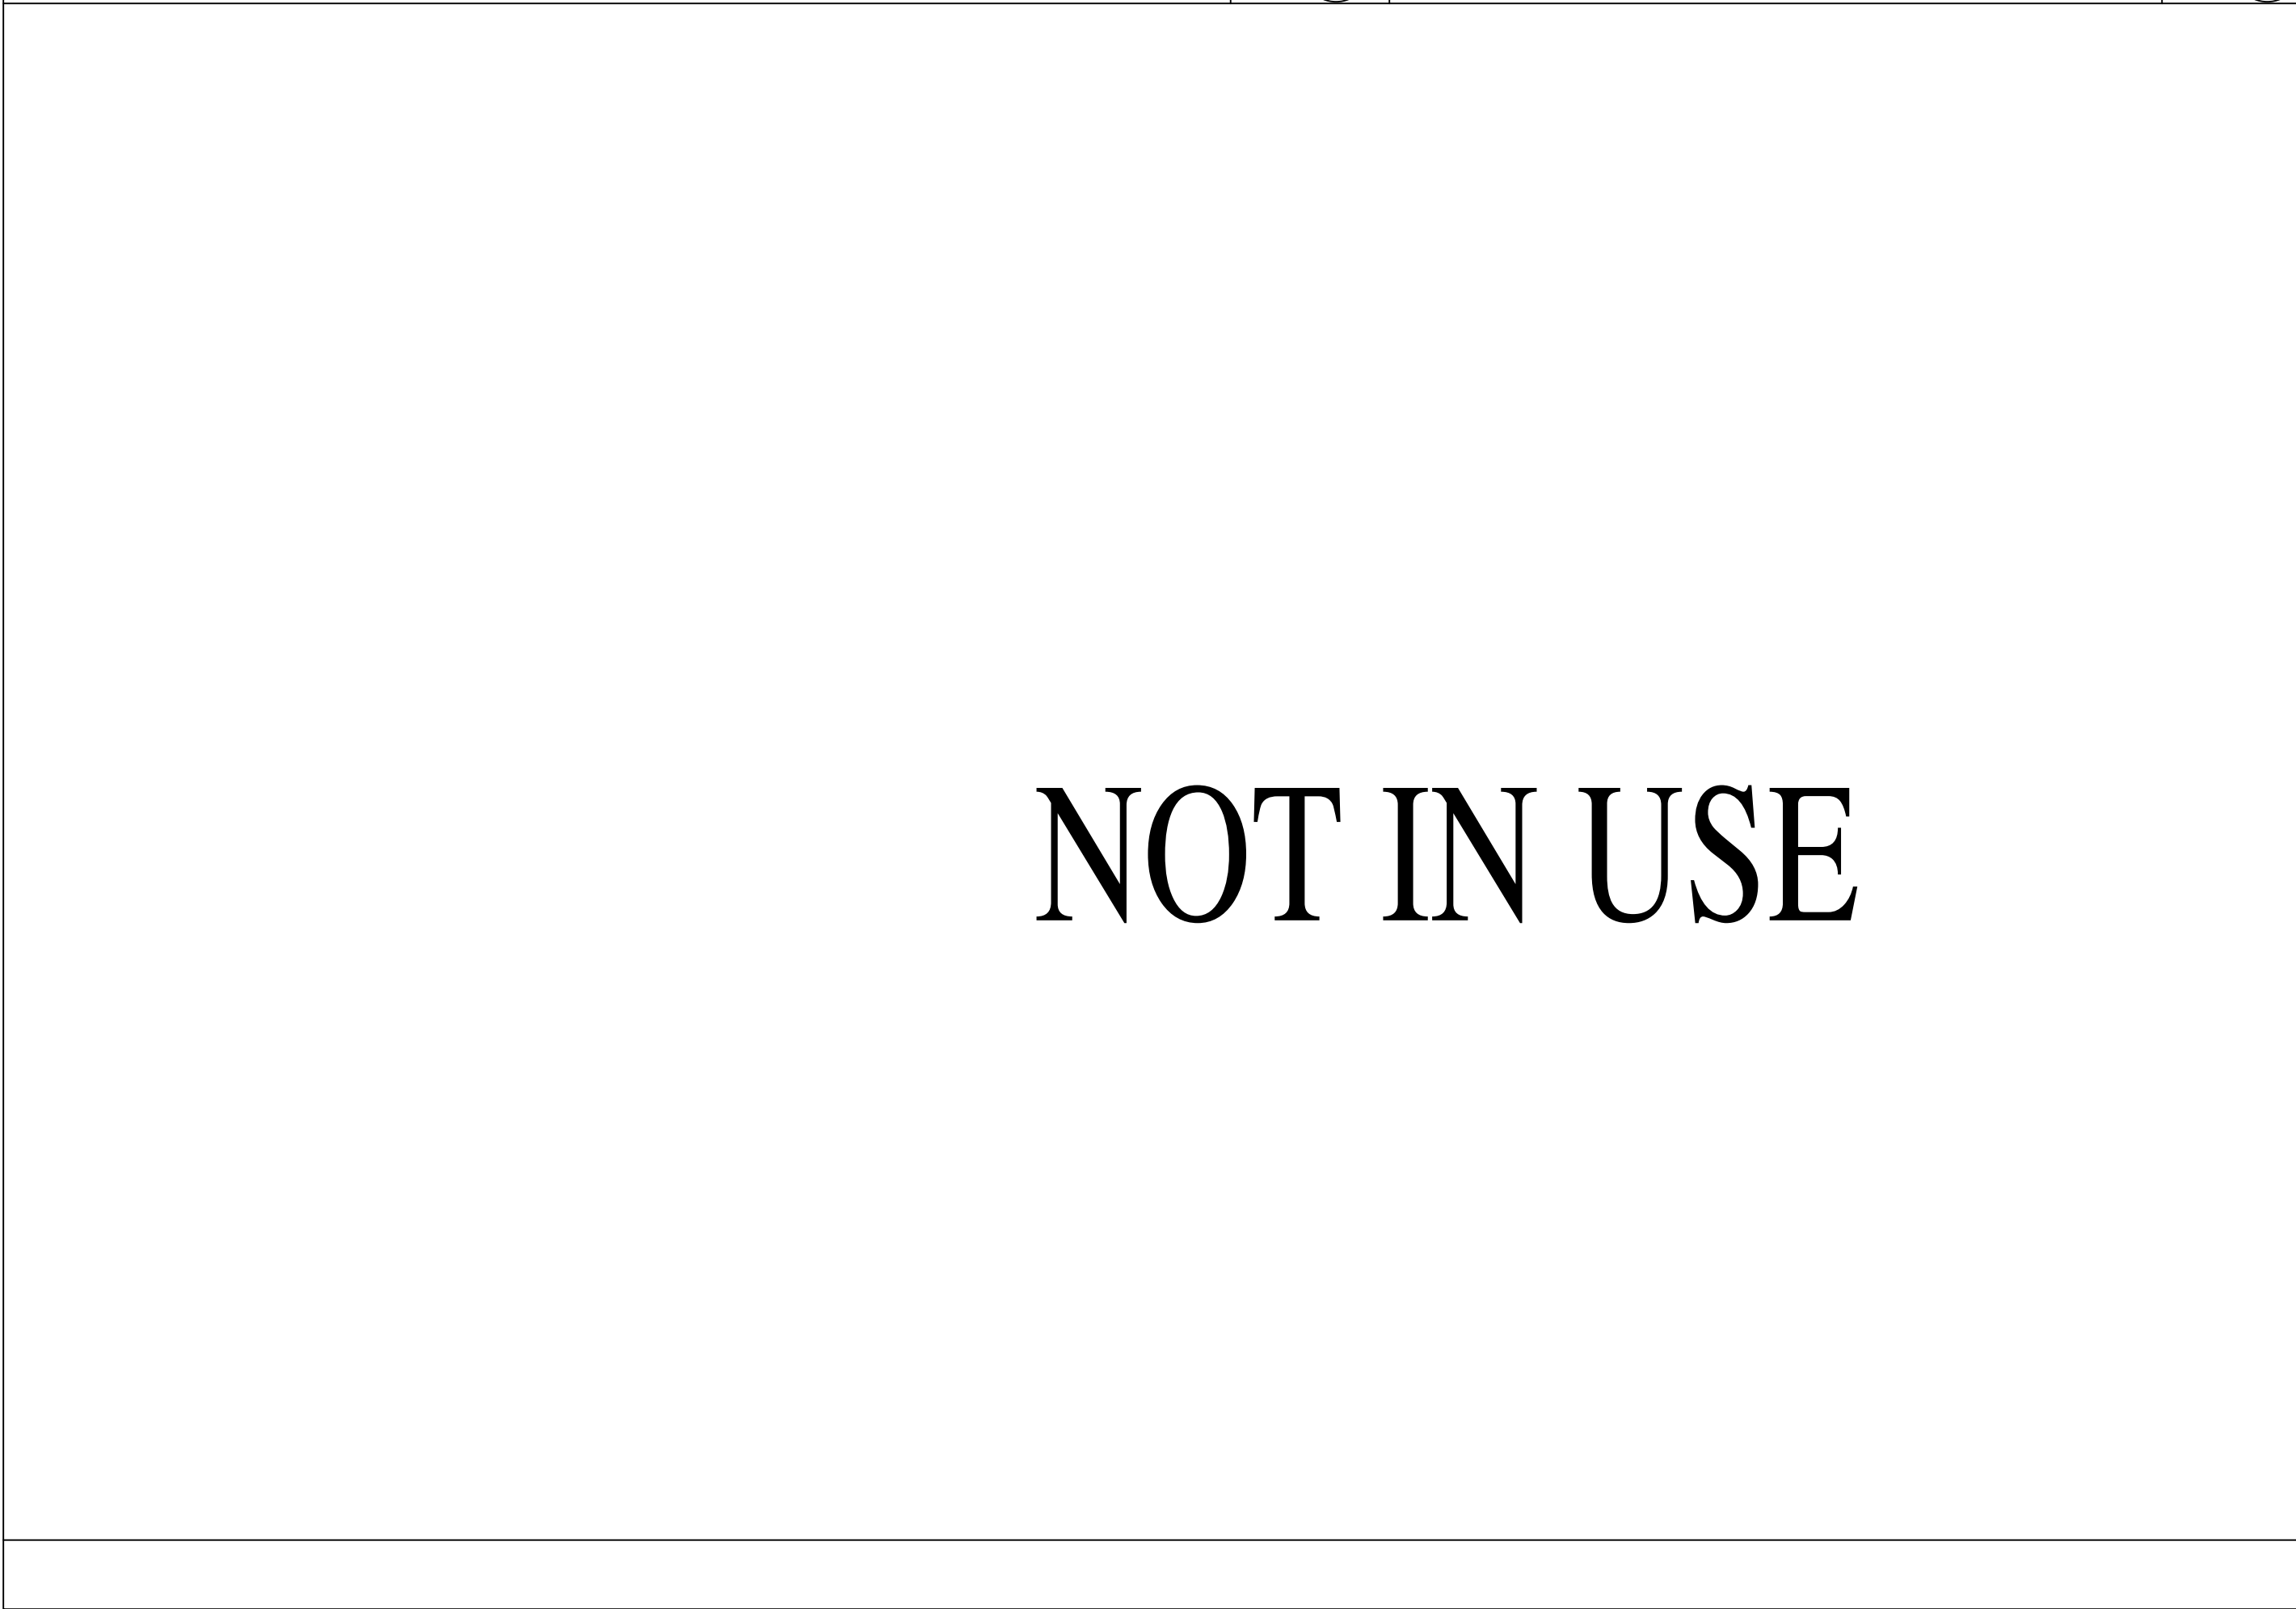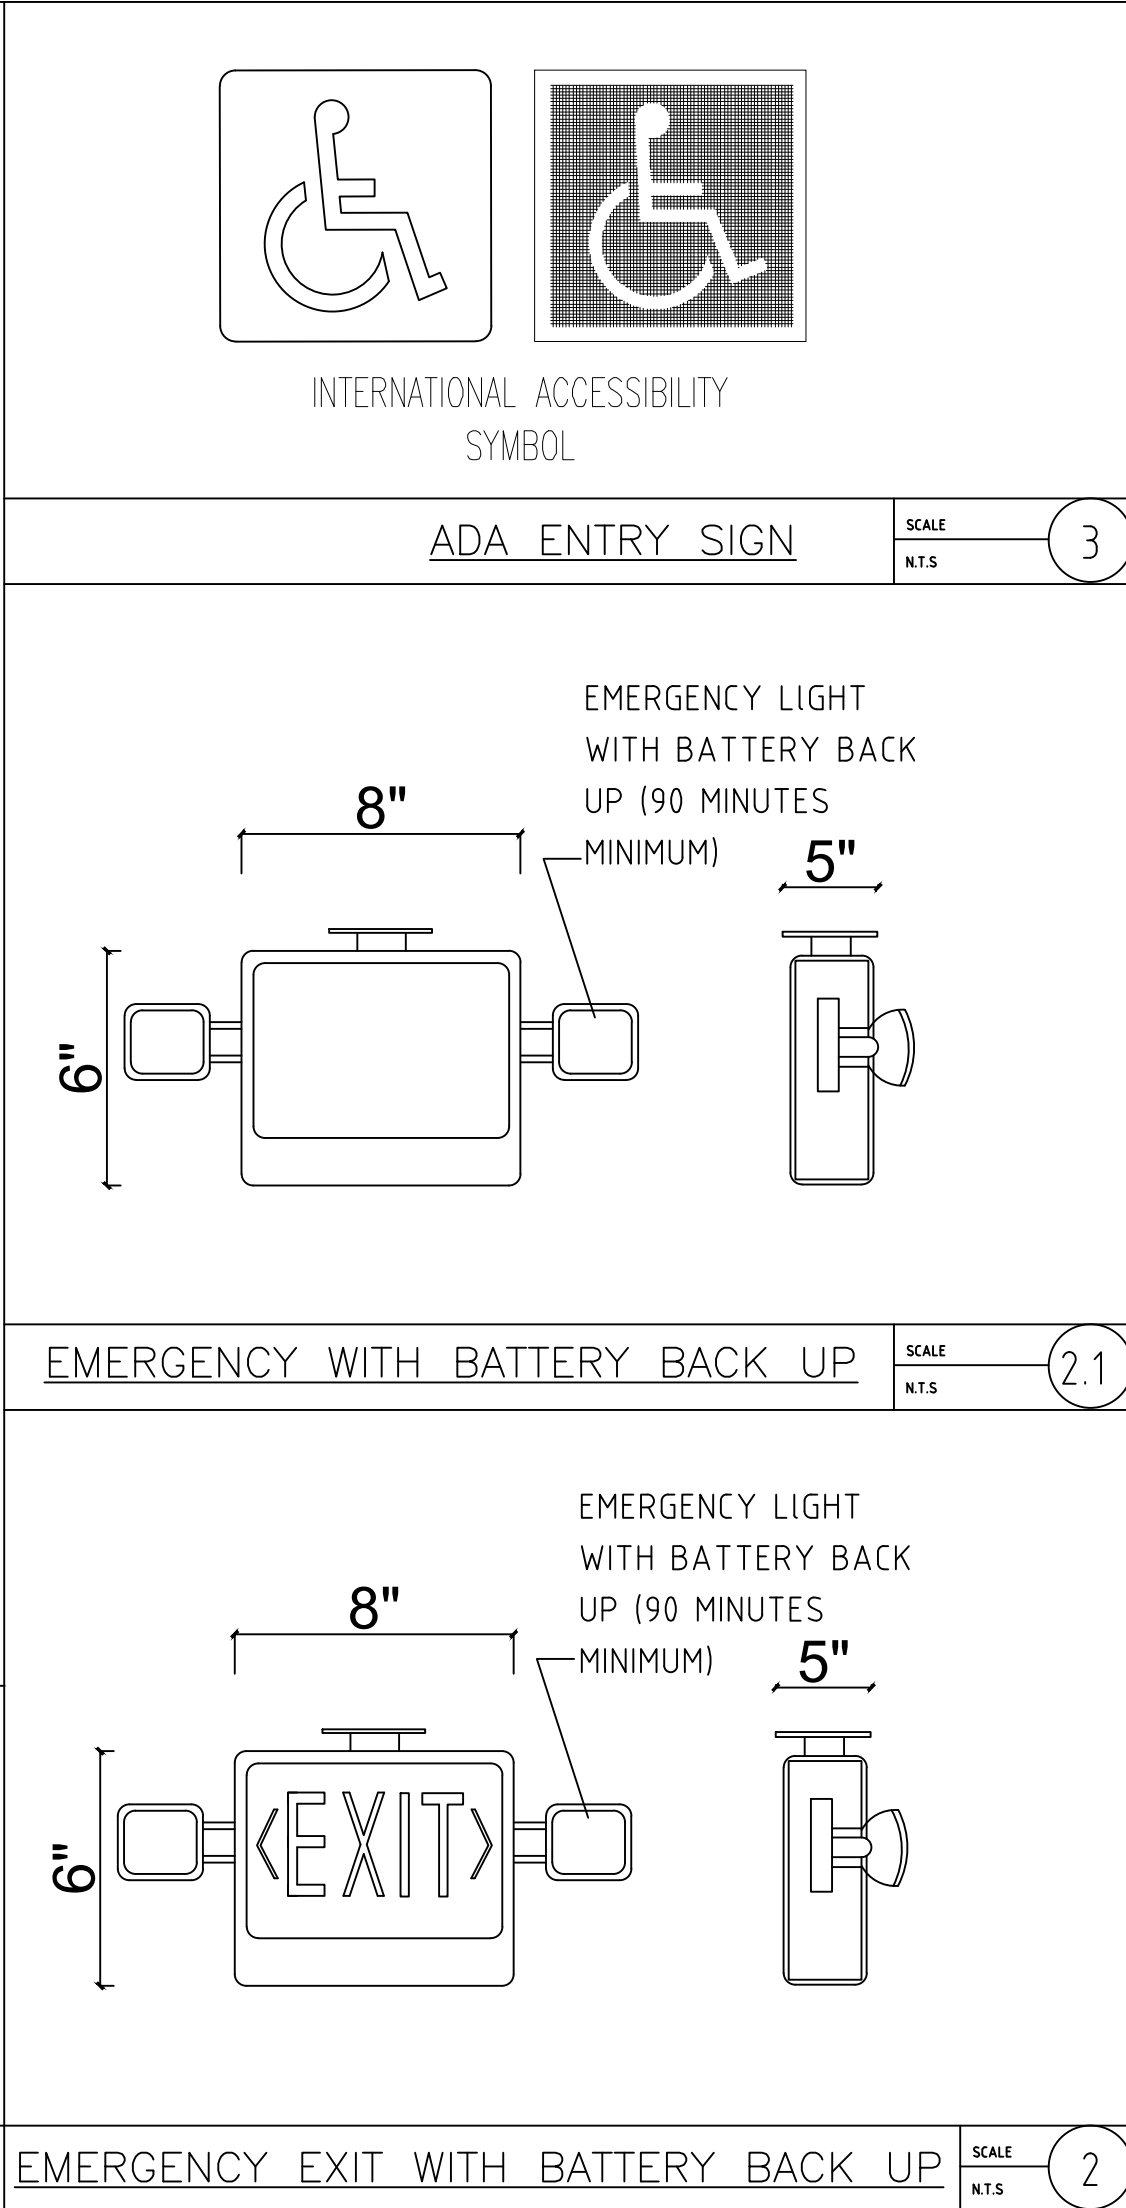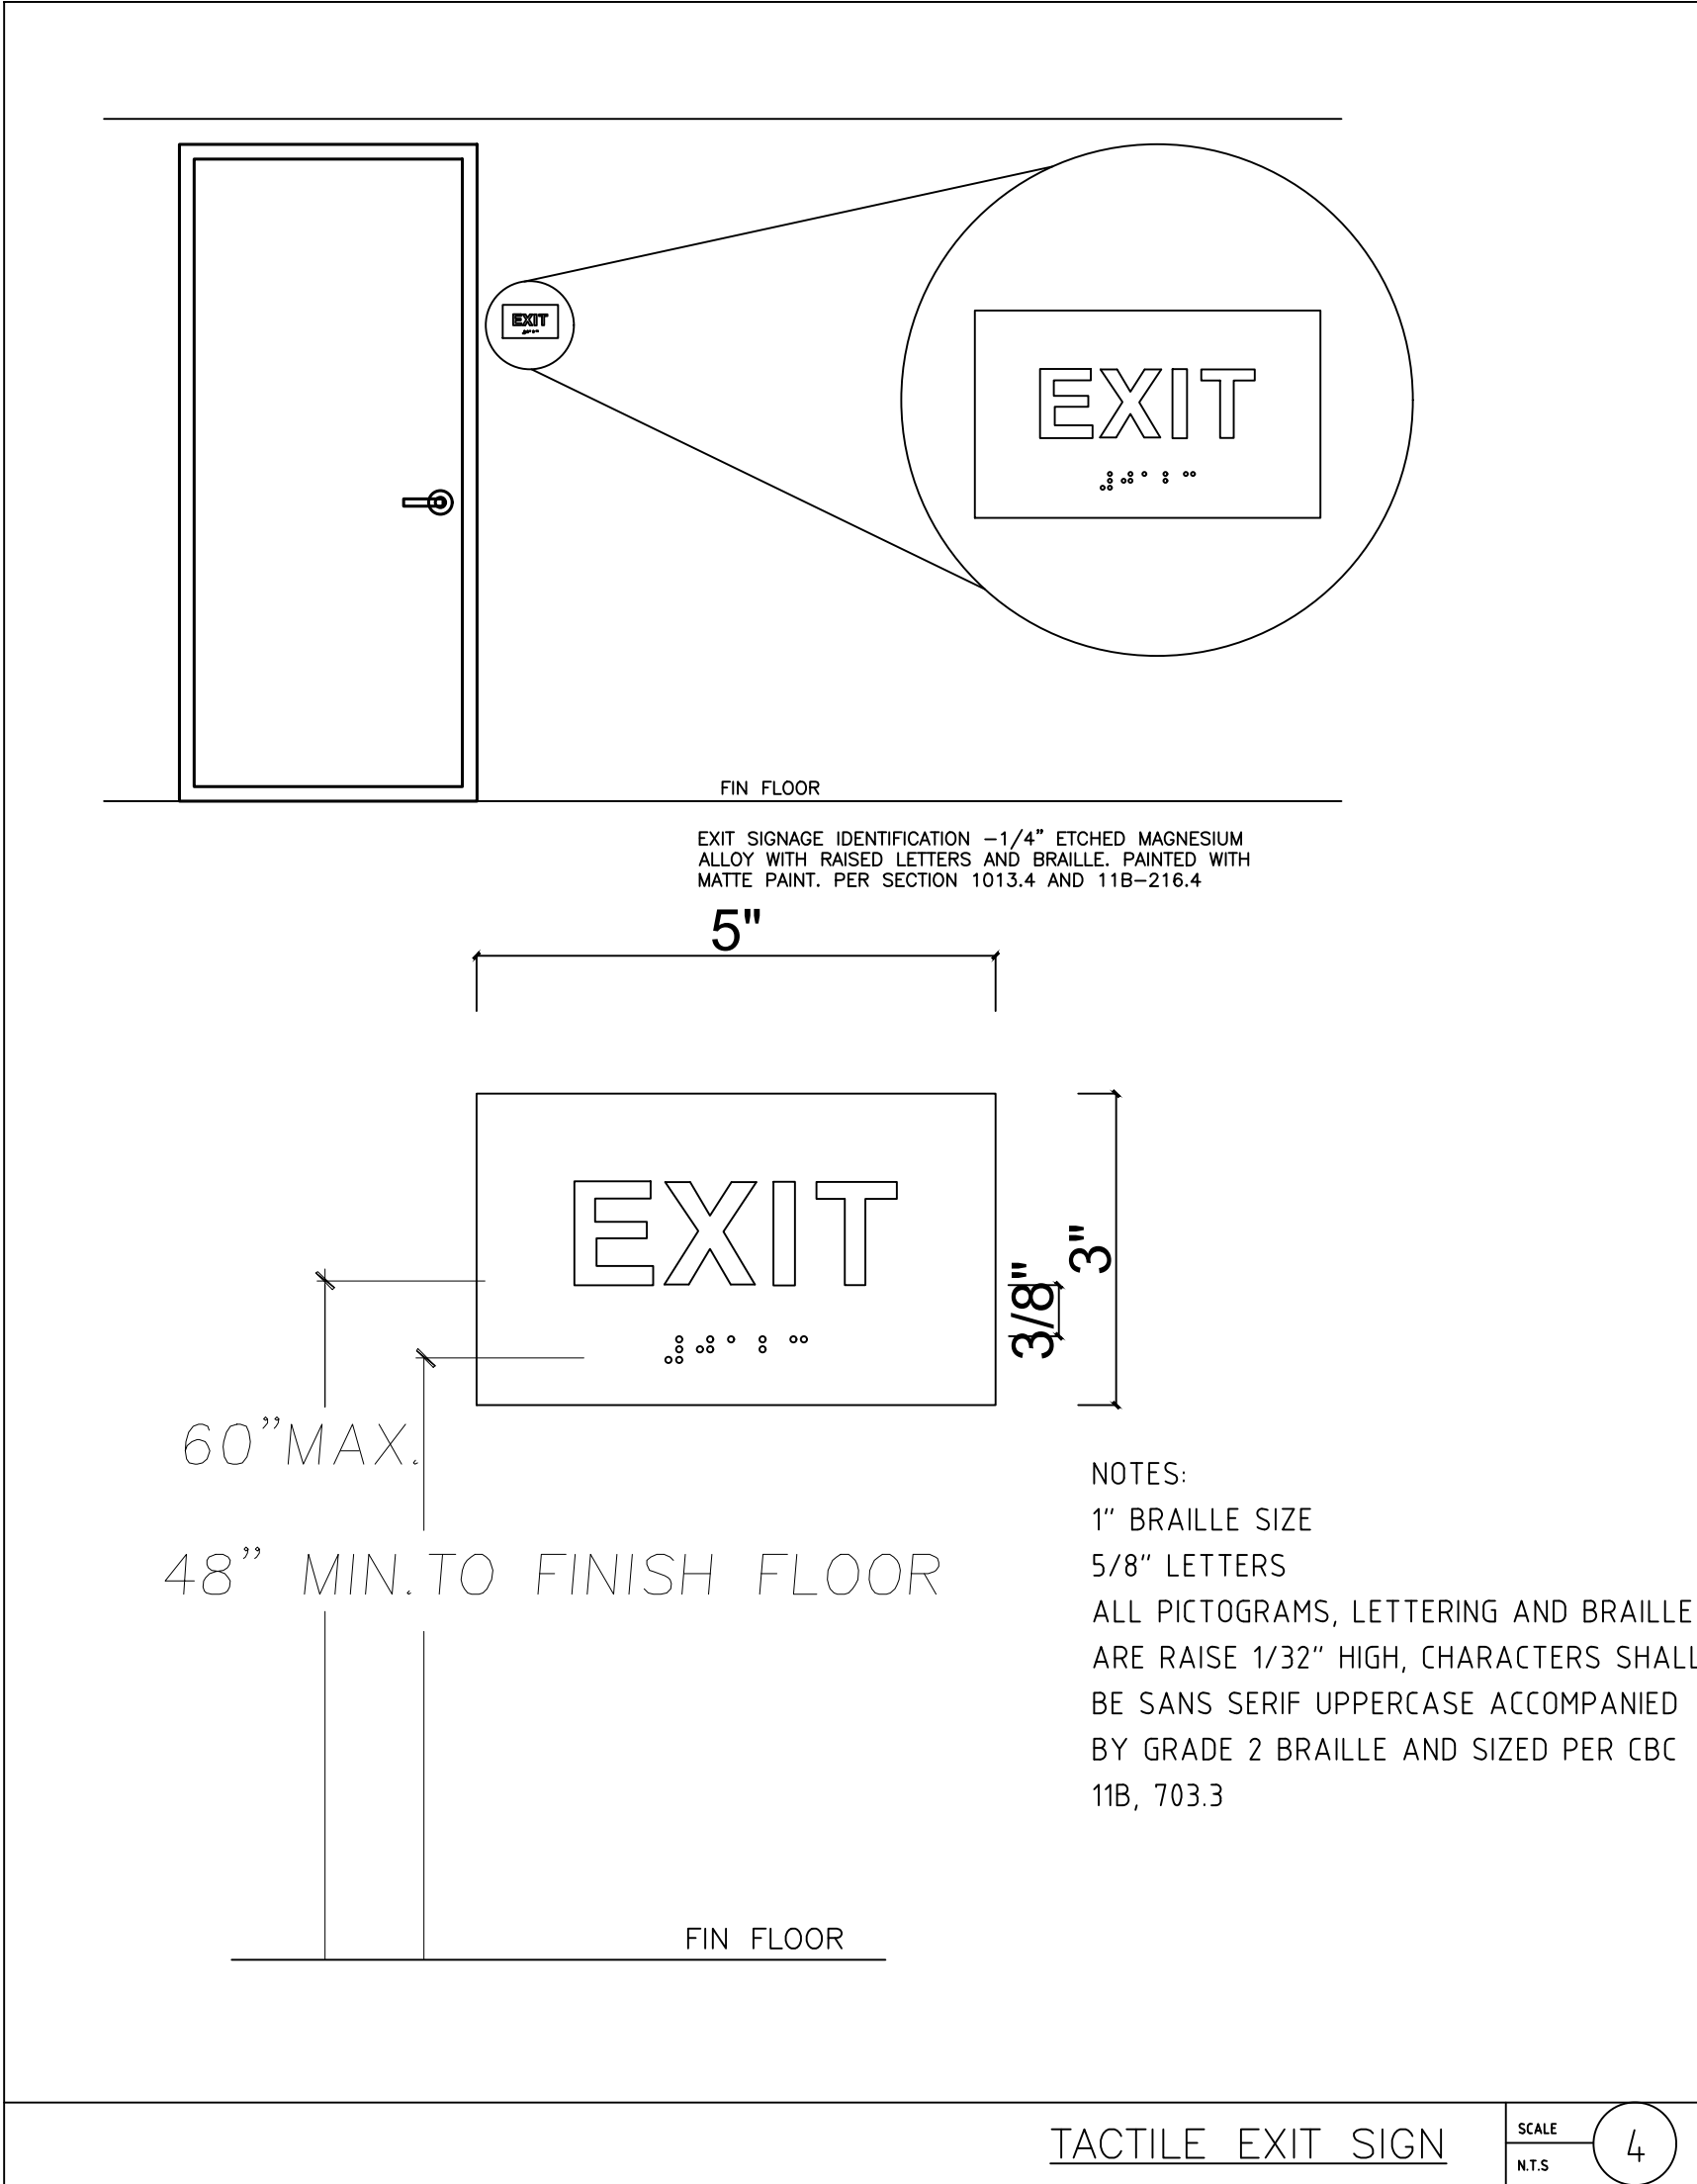

Joyee's Dumpling House			
Joyee Dumpling House-Vista 858-388-7688 1711 University Dr Ste 150, Vista, CA 92083			
Appetizers			
Wonton With Spicy Oil \$10.99	Pork Pancake \$12.99	Broccoli Beef \$12.99	Mongolian Beef \$12.99
Steam Chicken Feet \$12.99	Fried Cream Cheese Wontons (8) \$10.99	Beef Brisket With Jalapeno \$17.99	Curry With Beef \$17.99
Beef Wrap \$6.99	Cucumber Salad \$7.99	Beef Hot Pot \$18.99	Beef Belly W/ Pickled Cabbage \$18.99
Shrimp And Pork Shumai \$11.99	Steam Shrimp Dumplings (6) \$6.5	Rice Cake W/ Brown Sugar \$9.99	Sticky Rice With Pork \$10.99
Sesame Ball (8) \$4.99	Pot Stickers (8) \$5.99	Shredded Pork W/ Baked Tofu \$15.99	Shredded Pork W/ Bamboo \$15.99
Spring Roll (4) \$4.99	Scallion Pancake \$5.99	Sweet & Sour Pork W/ Pineapple \$15.99	Braised Pork Belly W/ Tofu \$17.99
Beef&Lamb			
Onion With Beef \$12.99	Kungpao Beef \$14.99	Cold Sliced Beef \$14.99	Black Pepper Beef \$12.99
Curry With Beef \$17.99	Beef Brisket With Jalapeno \$18.99	Beef Belly W/ Pickled Cabbage \$18.99	Beef Hot Pot \$18.99
Green Bean With Beef \$17.99	Cumin Beef \$17.99	Green Bean With Beef \$17.99	Cumin Lamb \$17.99
Onion With Lamb \$12.99	Broccoli Chicken \$14.99	Spicy Boiled Beef \$14.99	Spicy Crispy Chicken \$14.99
Chicken & Duck			
Salt & Pepper Chicken Wings \$14.99	Half BBQ Duck \$19.99	Kungpao Chicken \$14.99	Chicken With Mushroom \$14.99
BBQ Duck \$19.99	Popcorn Chicken \$14.99	Spicy Orange Chicken \$14.99	Spicy Chicken \$14.99
Broccoli Chicken \$14.99	Orange Chicken \$14.99	Spicy Boiled Fish \$16.99	Fish W/ Pickled Cabbage \$16.99
Salt & Pepper Shrimp \$12.99	Spicy Boiled Fish \$16.99	Fish W/ Pickled Cabbage \$16.99	Salt & Pepper Fish \$16.99
Pork			
Shredded Pork W/ Baked Tofu \$15.99	Shredded Pork W/ Bamboo \$15.99	Salt & Pepper Pork Ribs \$18.99	Steam Pork Belly With Preserved Vegetable \$18.99
Sweet & Sour Pork W/ Pineapple \$15.99	Braised Pork Belly W/ Tofu \$17.99	Spicy Pork Ribs \$18.99	Twice Cooked Spicy Pork \$15.99

Joyee's Dumpling House			
Joyee Dumpling House-Vista 858-388-7688 1711 University Dr Ste 150, Vista, CA 92083			
Vegetables			
Green Bean With Garlic \$12.99	Broccoli W/ Garlic \$11.99	Bok Choy W/ Garlic \$11.99	Mapo Tofu \$11.99
Eggplant With Szechuan Sauce \$12.99	Eggplant With Brown Sauce \$12.99	Garlic Snowpea Leaves \$15.99	Braised Tofu With Brown Sauce \$11.99
Bun			
Creamy Custard Bun \$6.99	Pork Soup Dumpling (xiao long bao) \$11.99	Char Siew Bun \$6.99	Sweet Taro Bun \$6.99
Pork Fried Bun \$11.99	Pork And Green Onion Bun \$10.99	Walnut Chocolate Bun \$6.99	Black Sesame Bun \$6.99
Dumpling			
Chives And Fish (12) \$13.99	Chicken And Corn (12) \$12.99	Pork And Chives (12) \$12.99	Beef With Onion (12) \$13.99
Chives And Egg (12) \$12.99	Pork And Cabbage (12) \$12.99	Chives And Fish (12) \$13.99	Chicken And Corn (12) \$12.99
Noodle & Rice			
Rice Noodle With Beef \$14.99	Braised Beef Noodle Soup \$13.99	Singapore fried rice noodle \$14.99	Pork Soybean Paste Noodle \$10.99
Shrimp Chow Mein \$13.99	Beef Chow Mein \$13.99	Vegetable Fried Rice Chow Mein \$12.99	Shrimp Fried Rice \$12.99
Sausage Fried Rice \$13.99	Beef Fried Rice \$13.99	Yangzhou Fried Rice \$13.99	Seafood Wonton Soup \$14.99
Soup			
Beef With Tofu Soup \$13.99	Egg Drop Soup \$10.99	Hot And Sour Soup \$10.99	Seafood Wonton Soup \$14.99

Joyee's Dumpling House			
Joyee Dumpling House-Torrey Highlands 858-240-7206			
Joyee Dumpling House-Oceanside 442-266-8416			
Joyee Dumpling House-Poway 858-486-1483			
Joyee Dumpling House-45 Ranch 858-899-8808			
7825 Highlands Village Pl, Suite E106, San Diego, CA 92129			
3460 Marron Rd, Suite 107, Oceanside, CA 92056			
12334 Poway Rd, Poway, CA 92064			
10550 Craftsman Way, #185, San Diego, CA 92127			

REVISIONS

PLAN CHECK CORRECTION

R-1

R-2

R-1

R-1

1ST. SUBMITAL:

2ND. SUBMITAL:

3RD. SUBMITAL:

PERMIT#

CITY PLANING:

CITY BUILDING:

TOPWAY ARCHI

DESIGN/BUILD

COMMERCIAL AND RESIDENTIAL

CAROLYN ZENG 626-400-0736

JOYEE'S DUMPLING HOUSE

6011 EL CAJON BLVD STE A

SAN DIEGO, CA 92115

DETAIL 3

SHEET

D-3

DATE

11/ 6 / 2024