


Steven Truong Residence– New ADU

6633 Electric Ave
La Jolla, CA 92037

ABBREVIATIONS

A.B.	ANCHOR BOLT	F.B.	FLAT BAR	O.C.	ON CENTER
A.B.C.	AGGREGATE BASE COURSE	F.D.	FLOOR DRAIN	O.D.	OUTSIDE DIAMETER
A.C.	ASPHALTIC CONCRETE/ AIR CONDITIONING	FDN	FOUNDATION	O.F.	OVERFLOW/OUTSIDE FACE
ACOUST.	ACOUSTICAL	F.E.	FIRE EXTINGUISHER	O.F.C.I.	OWNER FURNISHED CONTRACTOR INSTALLED
A.D.	ACCESS DOOR/AREA DRAIN	F.E.C.	FIRE EXTINGUISHER CABINET	O.F.O.I.	OWNER FURNISHED/ OWNER INSTALLED
ADD	ADDENDUM OR ADDITION	F.F.	FINISH FLOOR / FACTORY FINISH	O.H.	OPPOSITE HAND/OVERHEAD
ADJ	ADJUSTABLE	F.F.E	FINISHED FLOOR ELEVATION	OP'NG.	OPENING
A.F.F.	ABOVE FINISH FLOOR	F.P.E	FINISHED PAVING ELEVATION	OPP	OPPOSITE
A.E.F.F.	ABOVE EXISTING FINISH FLOOR	F.G.	FINISHED GRADE	P.L	PROPERTY LINE/PLATE
ALUM	ALUMINUM	F.H.C.	FIRE HOSE CABINET	PERIM	PERIMETER
ALT	ALTERNATE	FIN	FINISH	PERP()	PERPENDICULAR
∠	ANGLE	FLR	FLOOR	PLAM	PLASTIC LAMINATE
ANOD	ANODIZED	FLUOR	FLUORESCENT	PLAS	PLASTER
ARCH	ARCHITECT(URAL)	F.N.	FIELD NAILING	PLAST	PLASTIC
ASPH	ASPHALT	F.O.	FACE OF (SPECIFY ITEM)	P.D.	PLANTER DRAIN
@	AT	F.O.B.	FACE OF BRICK	PLWD	PLYWOOD
BD	BOARD	F.O.C.	FACE OF CONCRETE	P.S.F.	POUNDS PER SQUARE FOOT
BTWN	BETWEEN	F.O.F.	FACE OF FINISH	P.S.I.	POUNDS PER SQUARE INCH
B.F.	BOTTOM OF FOOTING	F.O.M.	FACE OF MASONRY	P.T.	PRESSURE TREATED
BLDG	BUILDING	F.O.P.	FACE OF PANEL	P.T.S.	POST TENSIONING SLAB
BLKG	BLOCKING	F.O.S.	FACE OF STUD	PVC	POLYVINYL CHLORIDE
BM	BEAM	FT	FOOT/FEET	R	RISE
B.N.	BOUNDARY NAIL	FTG	FOOTING	R.C.P.	REFLECTED CEILING PLAN
B.O.	BOTTOM OF	F.S.	FLOOR SINK	R.D.	ROOF DRAIN
BOT	BOTTOM	GA	GAUGE	REF	REFER(ENCE)
BRG	BEARING	GALV	GALVANIZED	REIN	REINFORCING
BSMT	BASEMENT	G.I.	GALVANIZED IRON	REQ(D)	REQUIRED
B.U.	BUILT-UP	GL	GLASS	REQMTS	REQUIREMENTS
C (or [)	CHANNEL	GLB	GLU LAM BEAM	RESIL	RESILIENT
CER	CERAMIC	GYP. BD.	GYPSUM BOARD	RET	RETAIN(ING)
CB	CATCH BASIN	H.B.	HOSE BIBB	RM	ROOM
C.I.P.	CAST-IN-PLACE	H.C.	HOLLOW CORE	R.O.	ROUGH OPENING
C.J.	CONTROL JOINT	HDR	HEADER	S	SOUTH
CL	CENTERLINE	HDWR	HARDWARE	S.C.	SOLID CORE
CLG	CEILING	HGR	HANGER	SCHED	SCHEDULE
CLR	CLEAR(ANCE)	H.M.	HOLLOW METAL	S.F.	SQUARE FEET
CMU	CONCRETE MASONRY UNIT	HORIZ	HORIZONTAL	SHT	SHEET
CLOS.	CLOSET	HR	HOUR	SIM	SIMILAR
C.O.	CLEAN OUT	HT	HEIGHT	S.M.F.E.	SURFACE MOUNTED FIRE EXTINGUISHER
COL	COLUMN	HVAC	HEATING, VENTILATING AND AIR CONDITIONING	SPEC	SPECIFICATION
CONC	CONCRETE	H.W.	HOT WATER	SO	SQUARE
CONSTR	CONSTRUCTION	I.D.	INSIDE DIAMETER	S.S.	STAINLESS STEEL
CONT	CONTINUOUS	I.N.	INCH	STAGG	STAGGERED
COORD	COORDINATE	INCL	INCLUDED	STD	STANDARD
CORR	CORRIDOR	I.E.	INVERT ELEVATION	STIFF	STIFFENED
CSK	COUNTERSINK	INSUL	INSULATION	STR	STRUCTURAL
CTR	CENTER	INT	INTERIOR	STL	STEEL
DP	DAMP/PROOFING	JAN	JANITOR	SYM	SYMMETRICAL
D.F.	DRINKING FOUNTAIN/	JST	JOIST	T	TREAD
DBL	DOUGLAS FIR	JT	JOINT	T.C.	TOP OF CURB OR CONCRETE
DIA ()	DIAMETER	KIT	KITCHEN	T&G	TONGUE AND GROOVE
DIAG	DIAGONAL	KJ	KEYED JOINT	THR	THRESHOLD
DIAPH	DIAPHRAGM	KO	KNOCKOUT	T.I.	TENANT IMPROVEMENT
DIM	DIMENSION	KIT	KITCHEN	T.J.	TOOLED JOINT
D.L.	DEAD LOAD	KJ	KEYED JOINT	T.N.	TOE NAILED
DN.	DOWN	KO	KNOCKOUT	T.O.	TOP OF (SPECIFY ITEM)
D.S.	DOWNSPOUT	LAM	LAMINATED	T.O.C.	TOP OF CURB
DTL	DETAIL	LAV	LAVATORY	T.O.S.	TOP OF SLAB
DWG	DRAWING	L.G.	LAG BOLT	T.O.W.	TOP OF WALL
DWLS	DOWELS	L.L.	LIVE LOAD	TRANS	TRANSVERSE
DWR	DRAWER	LLH	LONG LEG HORIZONTAL	TYP	TYPICAL
E	EAST	LLV	LONG LEG VERTICAL	U.B.C.	UNIFORM BUILDING CODE
EA	EACH	LONGIT	LONGITUDINAL	U.N.O.	UNLESS NOTED OTHERWISE
E.B.	EXPANSION BOLT	L.P.	LOW POINT	V.C.T.	VINYL COMPOSITION TILE
E.D.F.	ELECTRIC DRINKING FOUNTAIN	L.W.C.	LIGHT WEIGHT CONCRETE	VENT	VENTILATOR/VENTILATION
E.J.	EXPANSION JOINT	MAS	MASONRY	VERT	VERTICAL
EL	ELEVATOR	M.O.	MASONRY OPENING	V.R.	VAPOR RETARDER
ELEC	ELECTRIC(AL)	MAT'L	MATERIAL	VTR	VENT THRU ROOF
ELEV	ELEVATION	MAX	MAXIMUM	VWC	VINYL WALL COVERING
E.N.	EDGE NAIL	MECH	MECHANICAL	W	WEST
ENC	ENCLOSURE	MEMB	MEMBRANE	WDW	WINDOW
EQ	EQUAL	MET	METAL	W/	WITH
EQUIP	EQUIPMENT	MFR	MANUFACTURER	W.GL.	WIRE GLASS
E.W.	EACH WAY	MIN	MINIMUM	W.H.	WATER HEATER
EWC	ELECTRIC WATER COOLER	MISC	MISCELLANEOUS	W/O	WITHOUT
EXT	EXTERIOR	N	NORTH	WP	WATERPROOF
EXST	EXISTING	N.A.	NOT APPLICABLE	W.P.J.	WEAKENED PLANE JOINT
		N.I.C.	NOT IN CONTRACT	W.R.	WATER RESISTANT
		N.T.S.	NOT TO SCALE	WT	WEIGHT
		NO	NUMBER	W.W.F.	WELDED WIRE FABRIC
				W.W.M.	WELDED WIRE MESH

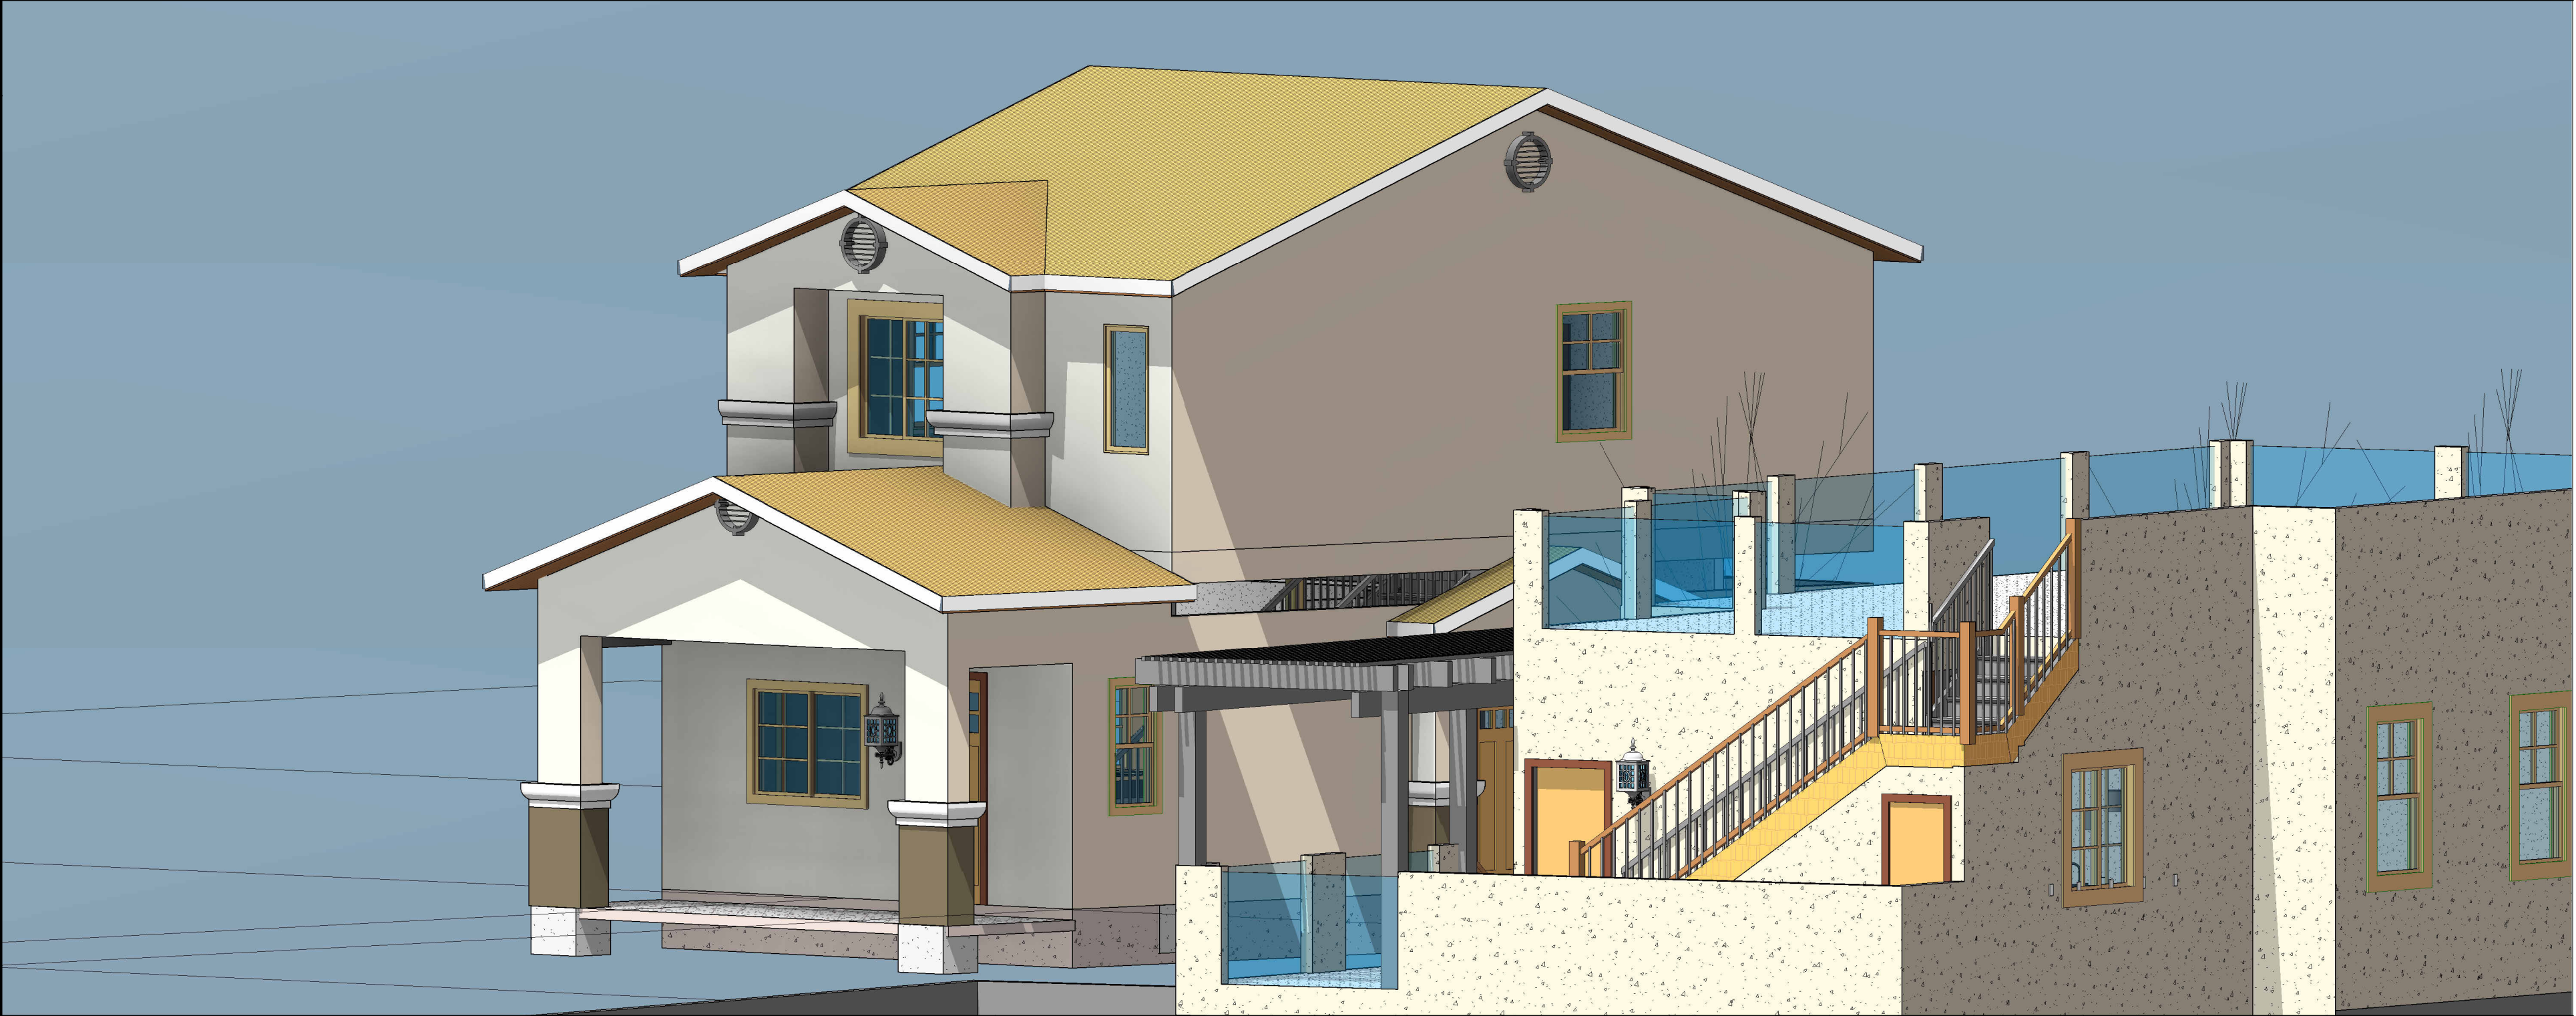

SCOPE OF WORK :

EXISTING 2-STORY SINGLE FAMILY RESIDENCE TO REMAIN.
DEMOLISH EXISTING DETACHED GARAGE (~400 SF).
PROPOSED NEW DETACHED TWO-STORY ADU BLDG
W/ ATTACHED GARAGES AND ROOF DECK.


DEFERRED SUBMITTAL

SOLAR PV SYSTEM


BUILDING CODE DATA

TYPE OF CONSTRUCTION: V-B
OCCUPANCY GROUP: R-3
GOVERNING CODES: 2022 California Residential Code
2022 California Building Code
2022 California Electrical Code
2022 California Mechanical Code
2022 California Plumbing Code
2022 California Existing Building Code
2022 California Fire Code

VINCINITY MAP

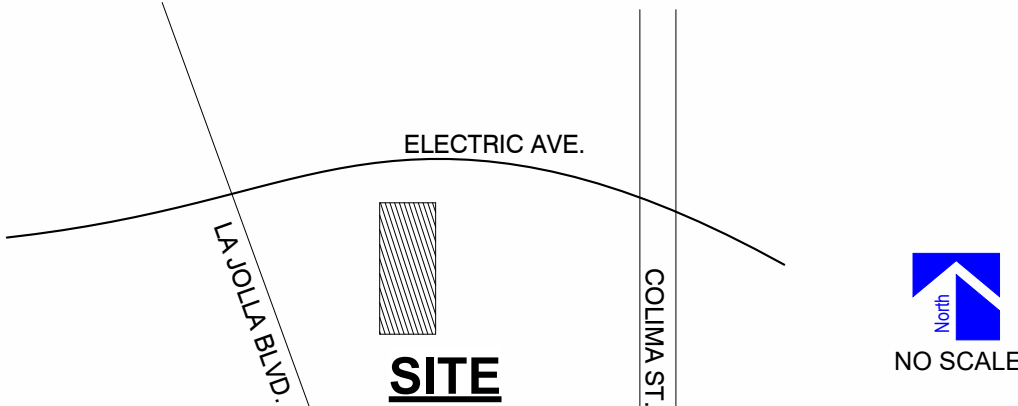

DRAWING SYMBOLS

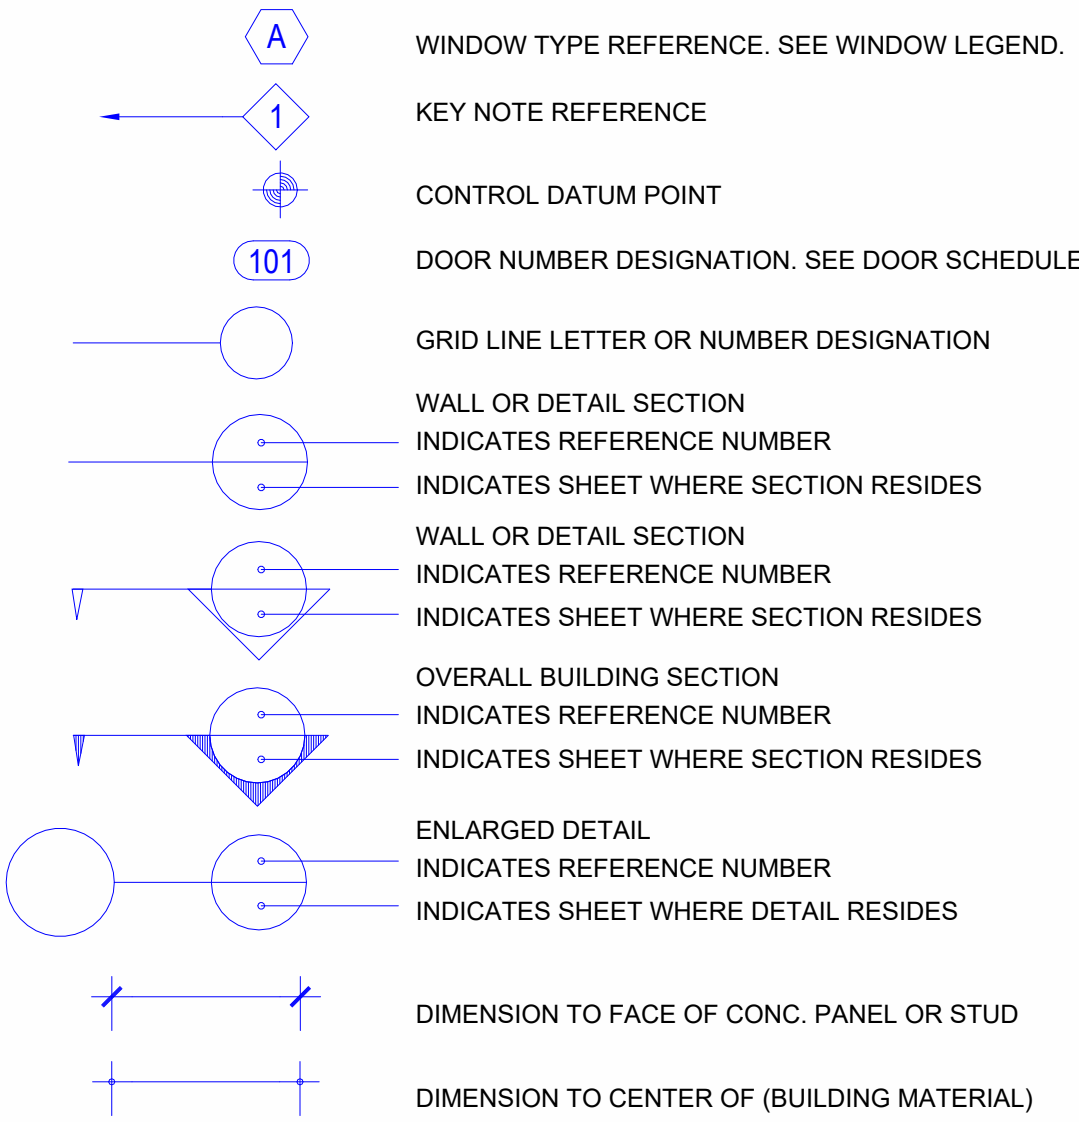

PROJECT DATA

PROJECT NAME: STEVEN TRUONG RES - NEW ADU
PROJECT ADDRESS: 6633 Electric Ave,
La Jolla, CA 92037
OWNER (Responsible for Water & Sewer Fees):
STEVEN TRUONG
LEGAL DESCRIPTION: POR. LOT 10, HYMAN'S ADDITION,
MAP NO. 1808, DOC NO. 2019-0311700
ZONE: -
PARCEL NUMBER: 351-493-10
YEAR OF BUILT: -
EXISTING BLDG FIRE SPRINKLER: NO
COASTAL ZONE: YES
BUILDING ANALYSIS:
EXISTING RESIDENCE (2-STORY): TO REMAIN
EXISTING DETACHED GARAGE: ~400 SF (DEMOLISH)
PROPOSED ADU BLDG:
1ST FLOOR LIVING: 900 SF
GARAGE (2-CAR): 228 SF
GARAGE (1-CAR): 222 SF
2ND FLOOR LIVING: 1,093 SF
2ND FLOOR DECK: 263 SF
ROOF DECK: 1,148 SF
TOTAL PROPOSED LIVING SF: 1,993 SF

INFOMATION INDEX

Title Page	A01
Site Plan	A02
General Notes & Specification	A03
CALGREEN	A04
CALGREEN	A05
BMP Plan	A06
Floor Plan	A101
Door-Windows Schedule	A102
Sections	A103
Roof Plan	A104
Elevations	A105
TITLE-24 Unit-A	A106
TITLE-24 Unit-A	A107
TTTLE 24	A108
TITLE 24 Unit-B	A109
TITLE-24 Unit-B	A110
Mechanical Plan	A200
Electrical Plan	A201
Landscpaing Plan	L1
Irrig. & Planting Details	L2
Landscaping Details	L3
Foundation / Framing Plan	S101
Structure Notes	SD0
Structure Details	SD1
Structure Details	SD2