




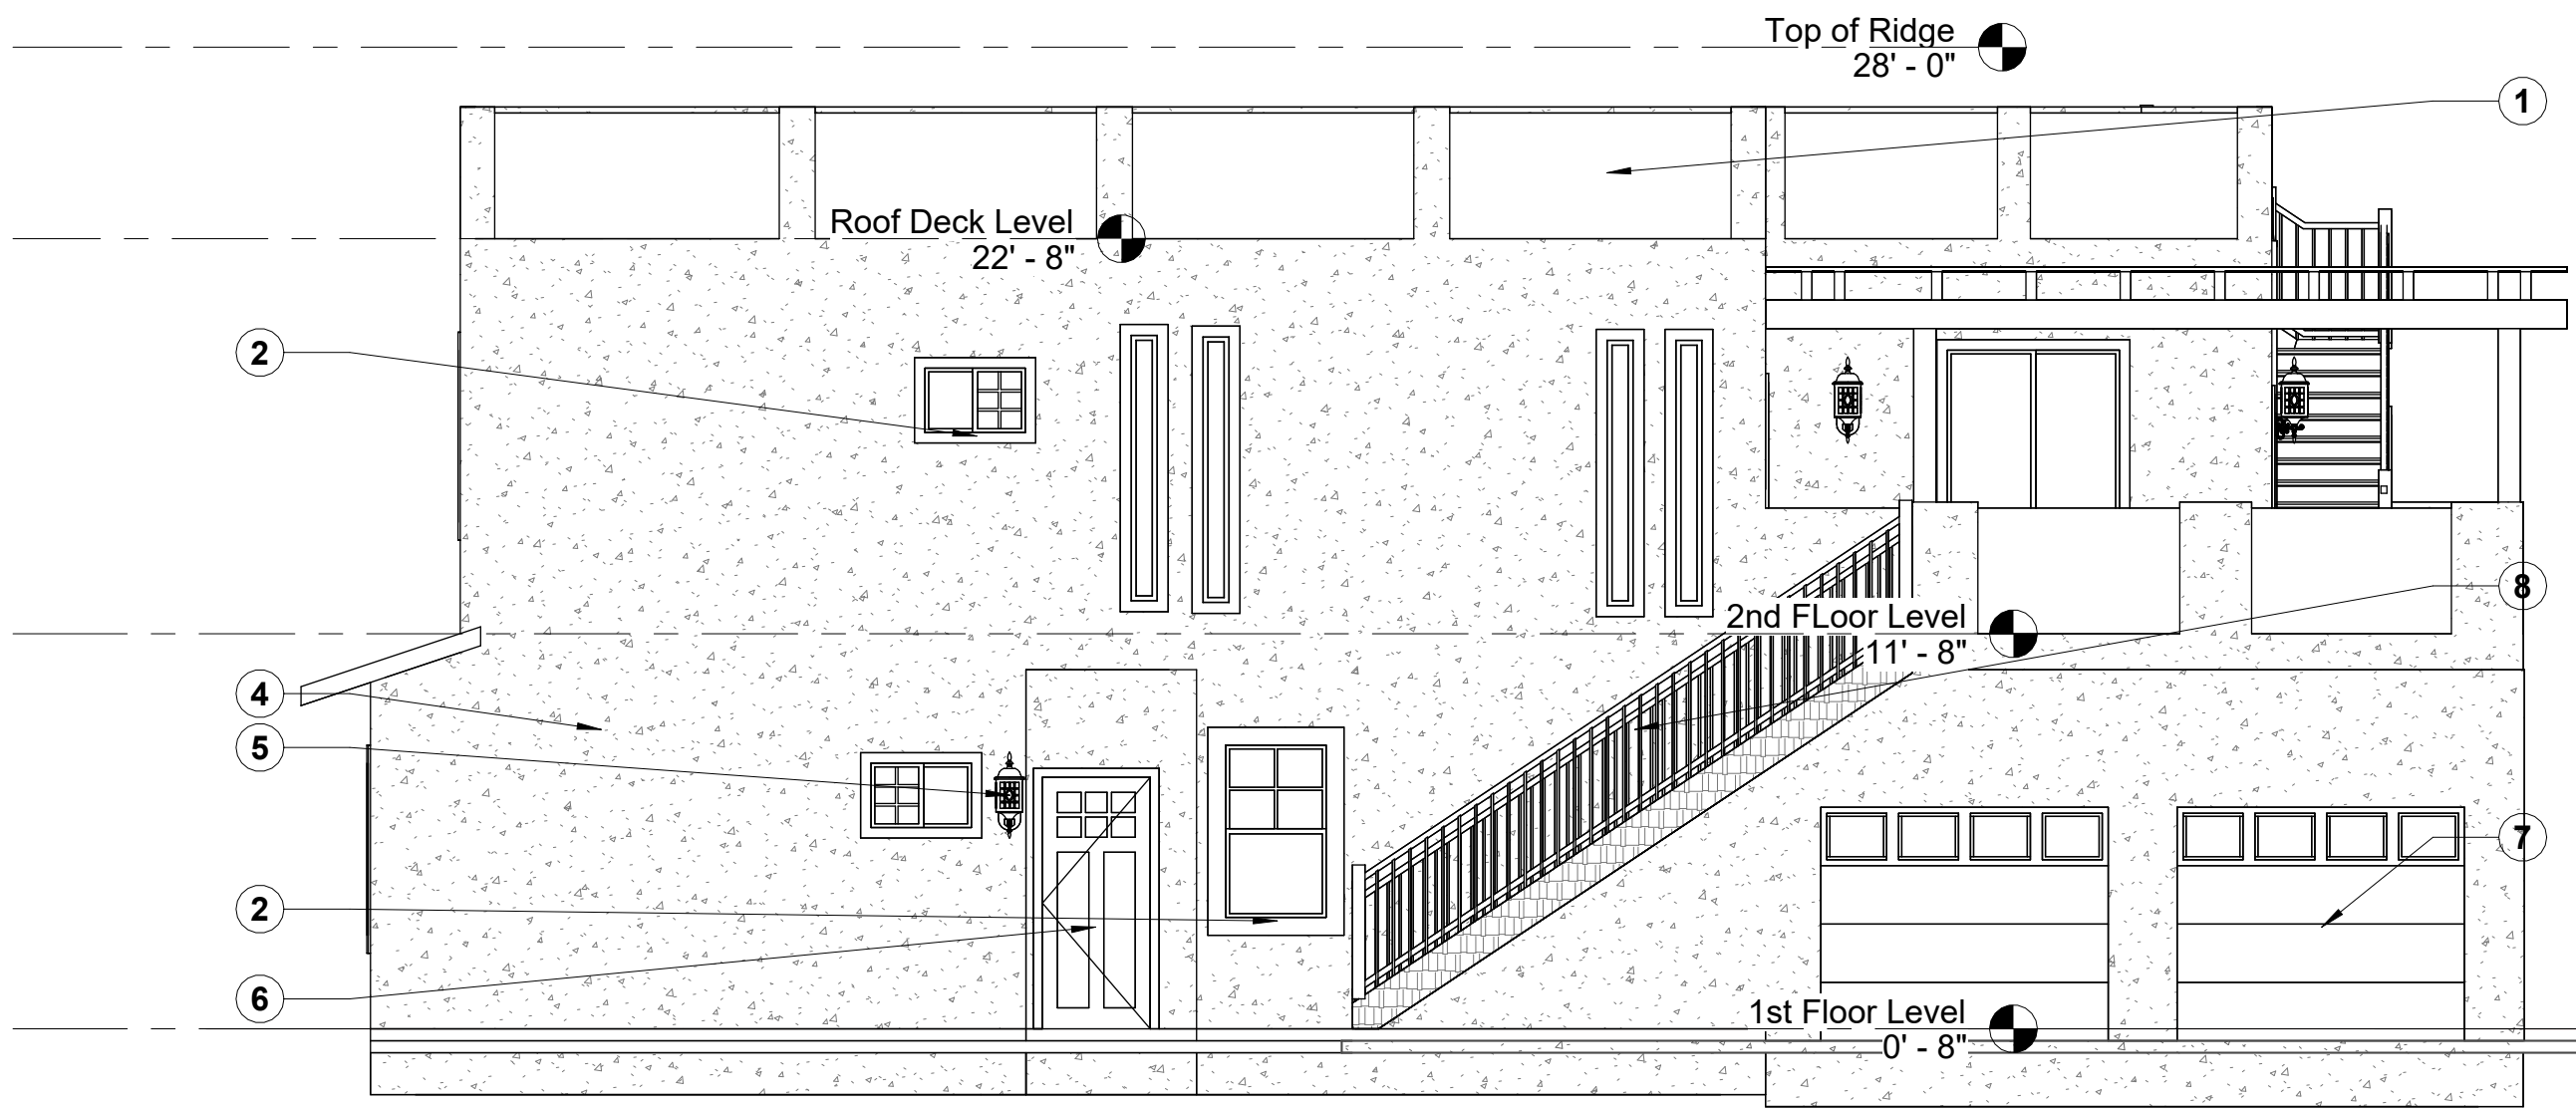


1 **South Elev.**
3/16" = 1'-0"

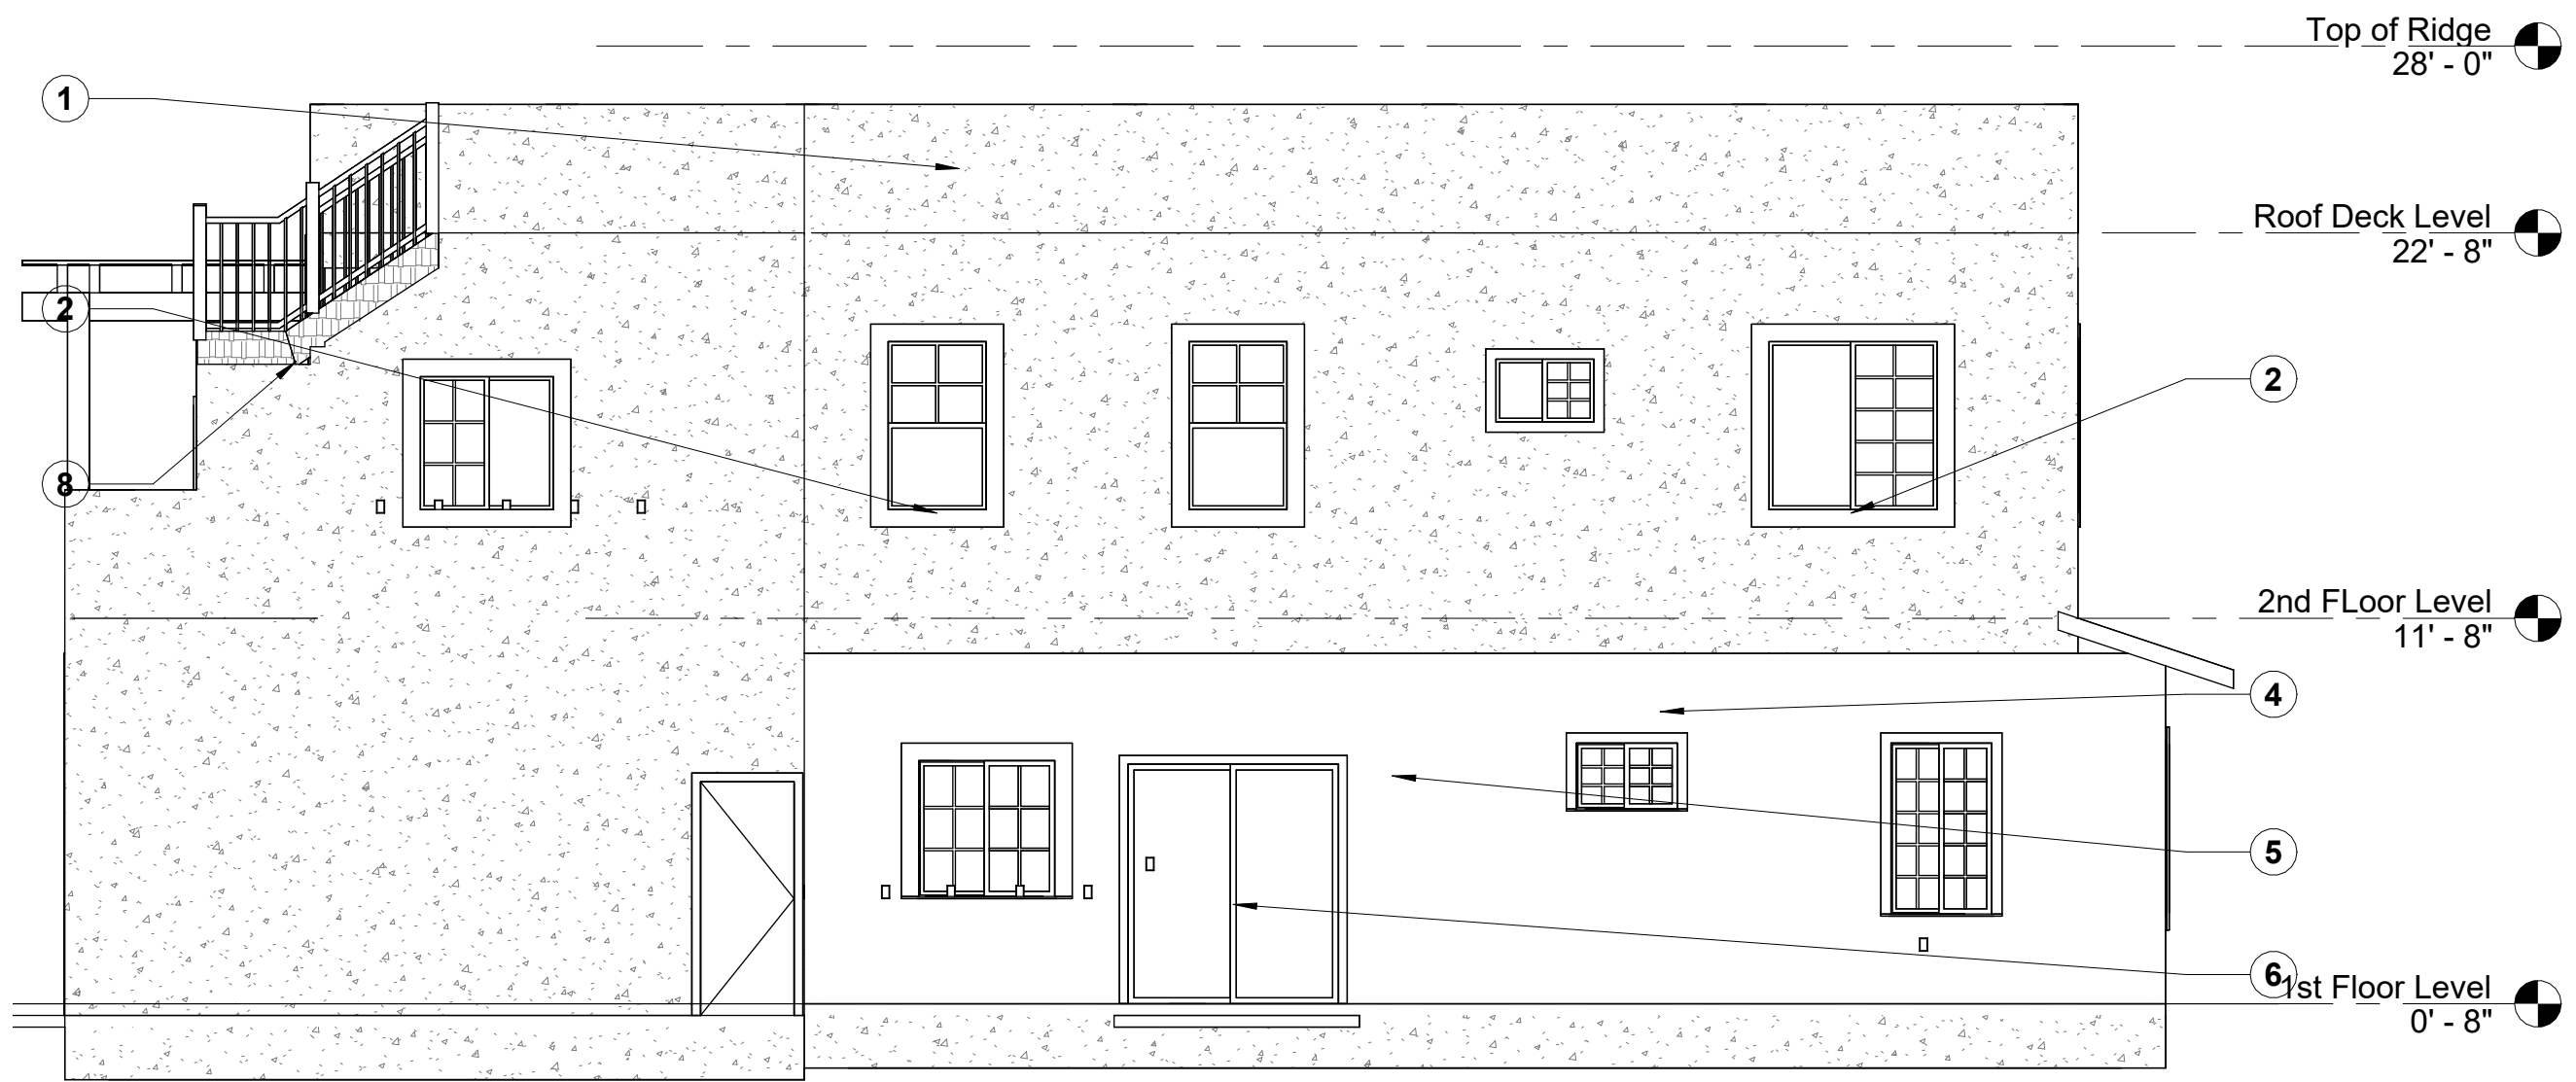

2 **North Elev.**
3/16" = 1'-0"

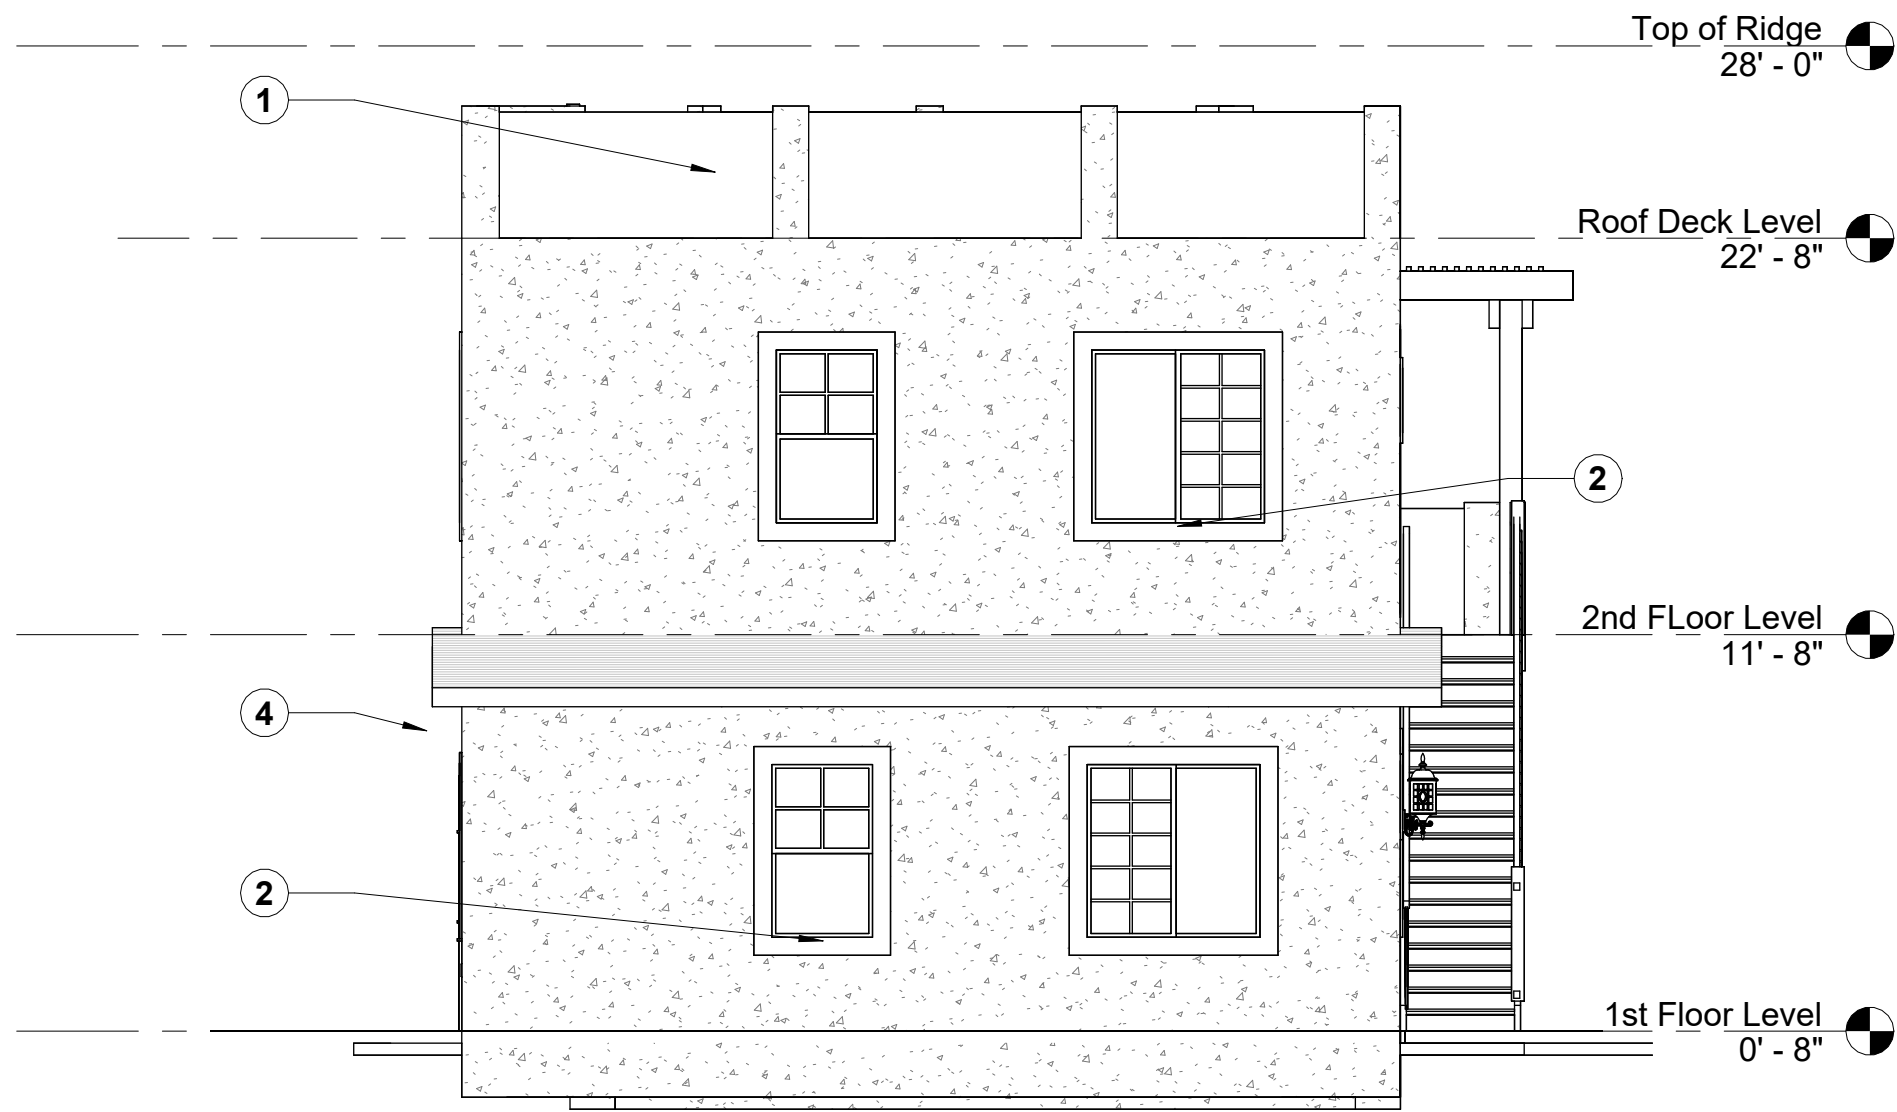

3 **West Elev.**
3/16" = 1'-0"

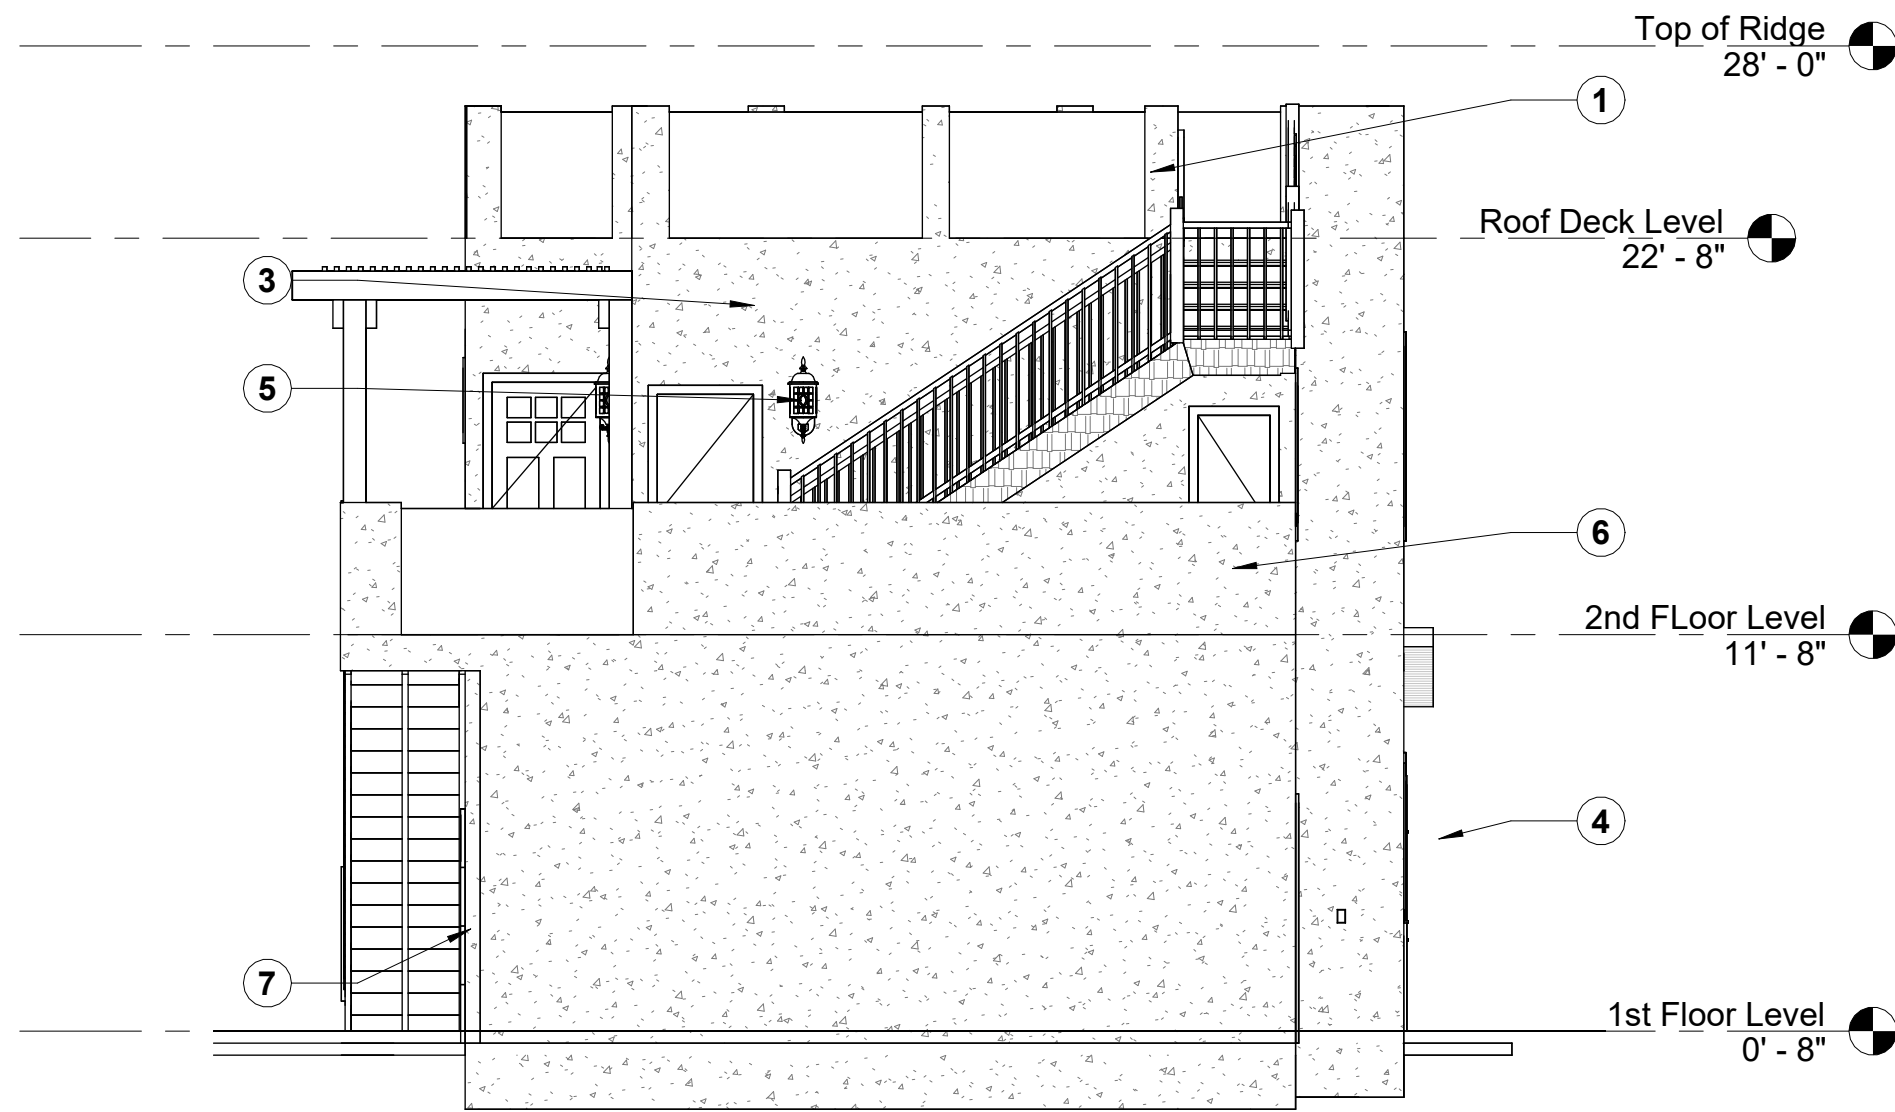

4 **East Elev.**
3/16" = 1'-0"

KEYNOTES:

- 42" HIGH GUARDRAIL @ ROOF DECK
- WINDOW PER SCHEDULE
- OPEN WOOD TRELLIS @ ROOF DECK
- STUCCO AT EXTERIOR WALL TO MATCH EXISTING
- EXTERIOR LIGHT
- EXTERIOR DOOR PER SCHEDULE
- SECTIONAL GARAGE DOOR
- EXTERIOR MTL STAIR W/ 42" GUARDRAIL

Revision Dates	
1	08.15.24
2	01.01.25

SHEET TITLE
Elevations

Drawing Date 08.27.26
Check By Checker
Drawn By Author
Scale As indicated
Job Number 022225
Sheet Number