




SHEET TITLE
Irrigation Plan


Sheet Number

L33

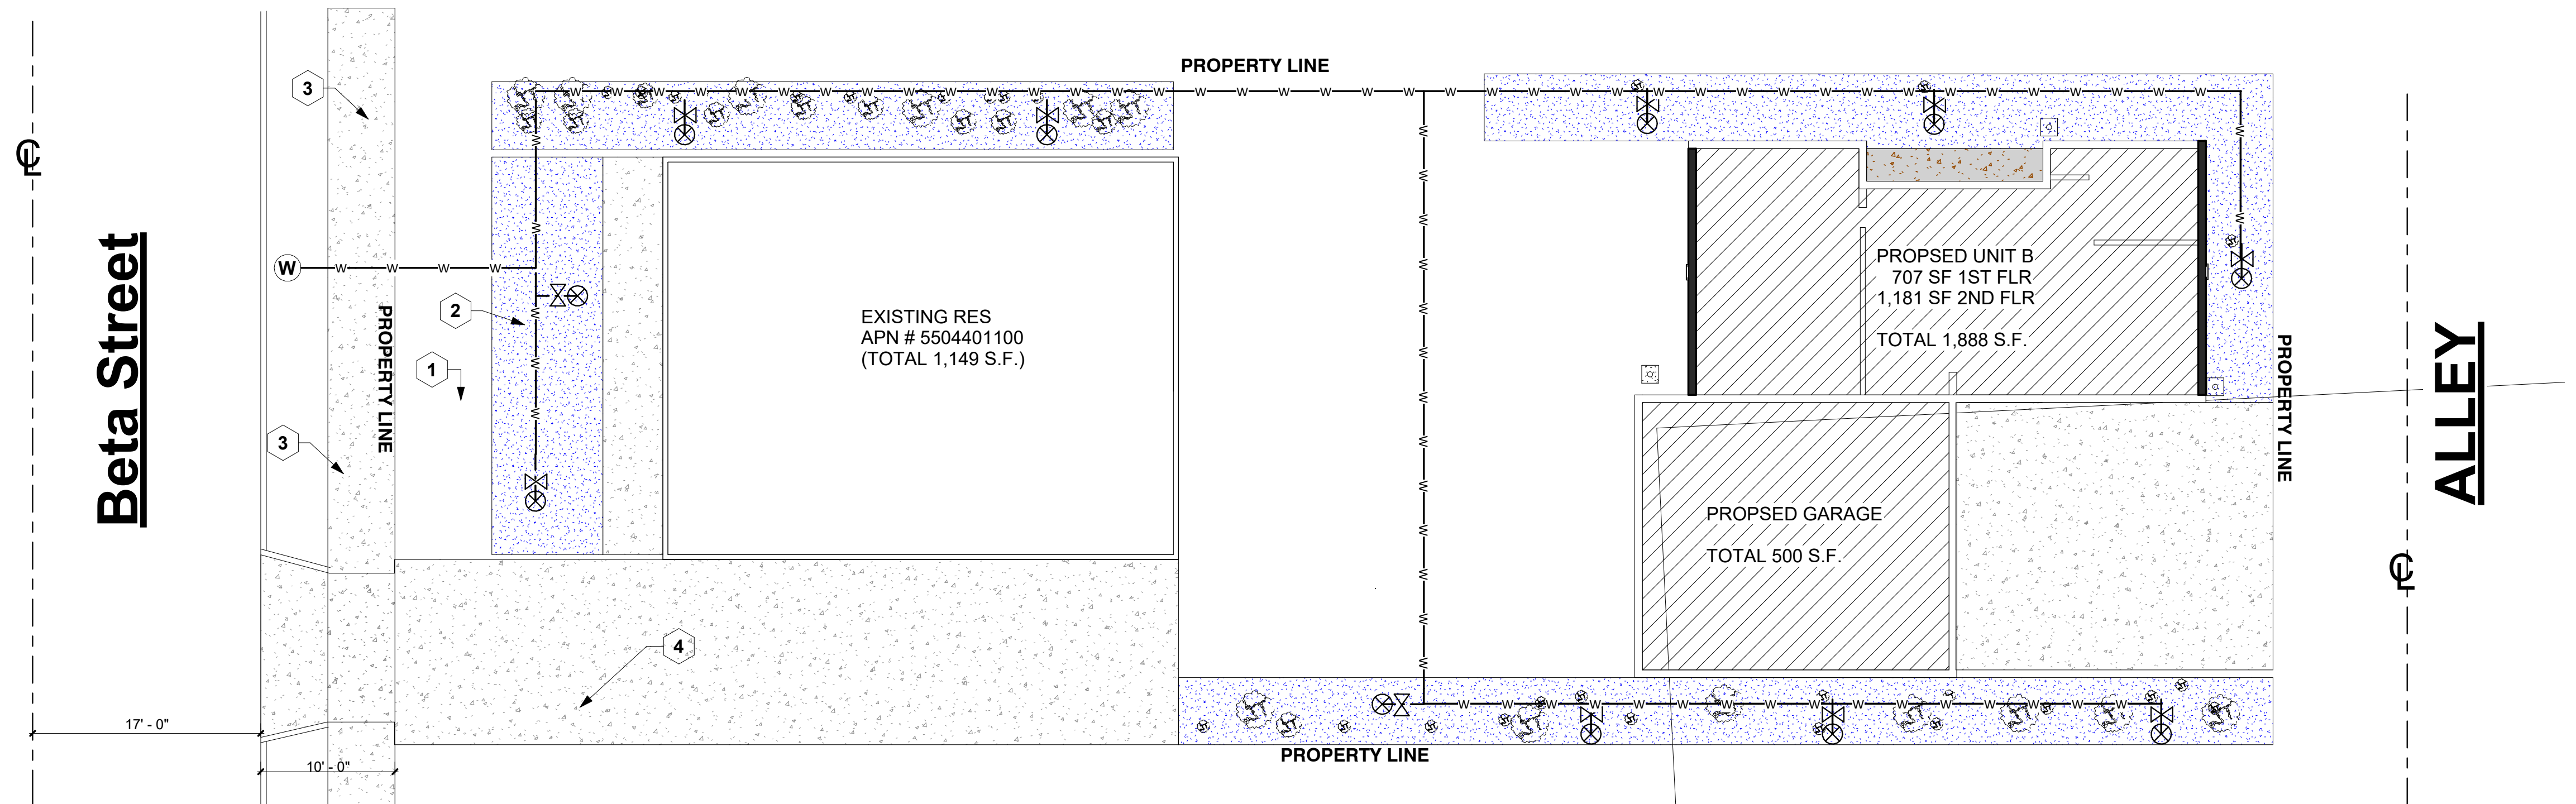

1 *Irrigation Plan*

Irrigation

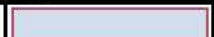Quantity	Symbol	Description
Meters/Pumps		
1		1 inch meter
1		1 inch meter
Backflow Devices		
2		Febco 850 - 1"
Control Valves		
8		Rain Bird XACZ-100-PRF-BF
Y-Strainers / Filters		
2		Febco 650A-1"
Irrigation Accessories		
2		Irritrol Systems RS1000
2		Nibco 1 1/2" isolation valve
10		Nibco 1" isolation valve
2		Rain Bird ESP-8LXi Plus
2		Wilkins 70-1 Pressure Reducing Valve (75-45psi)
Lateral Line Pipe		
46 ft		Class 200 3/4"
Mainline Pipe		
199 ft		Class 200 1"
Drip Tubing		
2263 ft		Rain Bird XFD-09-18
Wire		
213 ft		18 Gauge - Common