



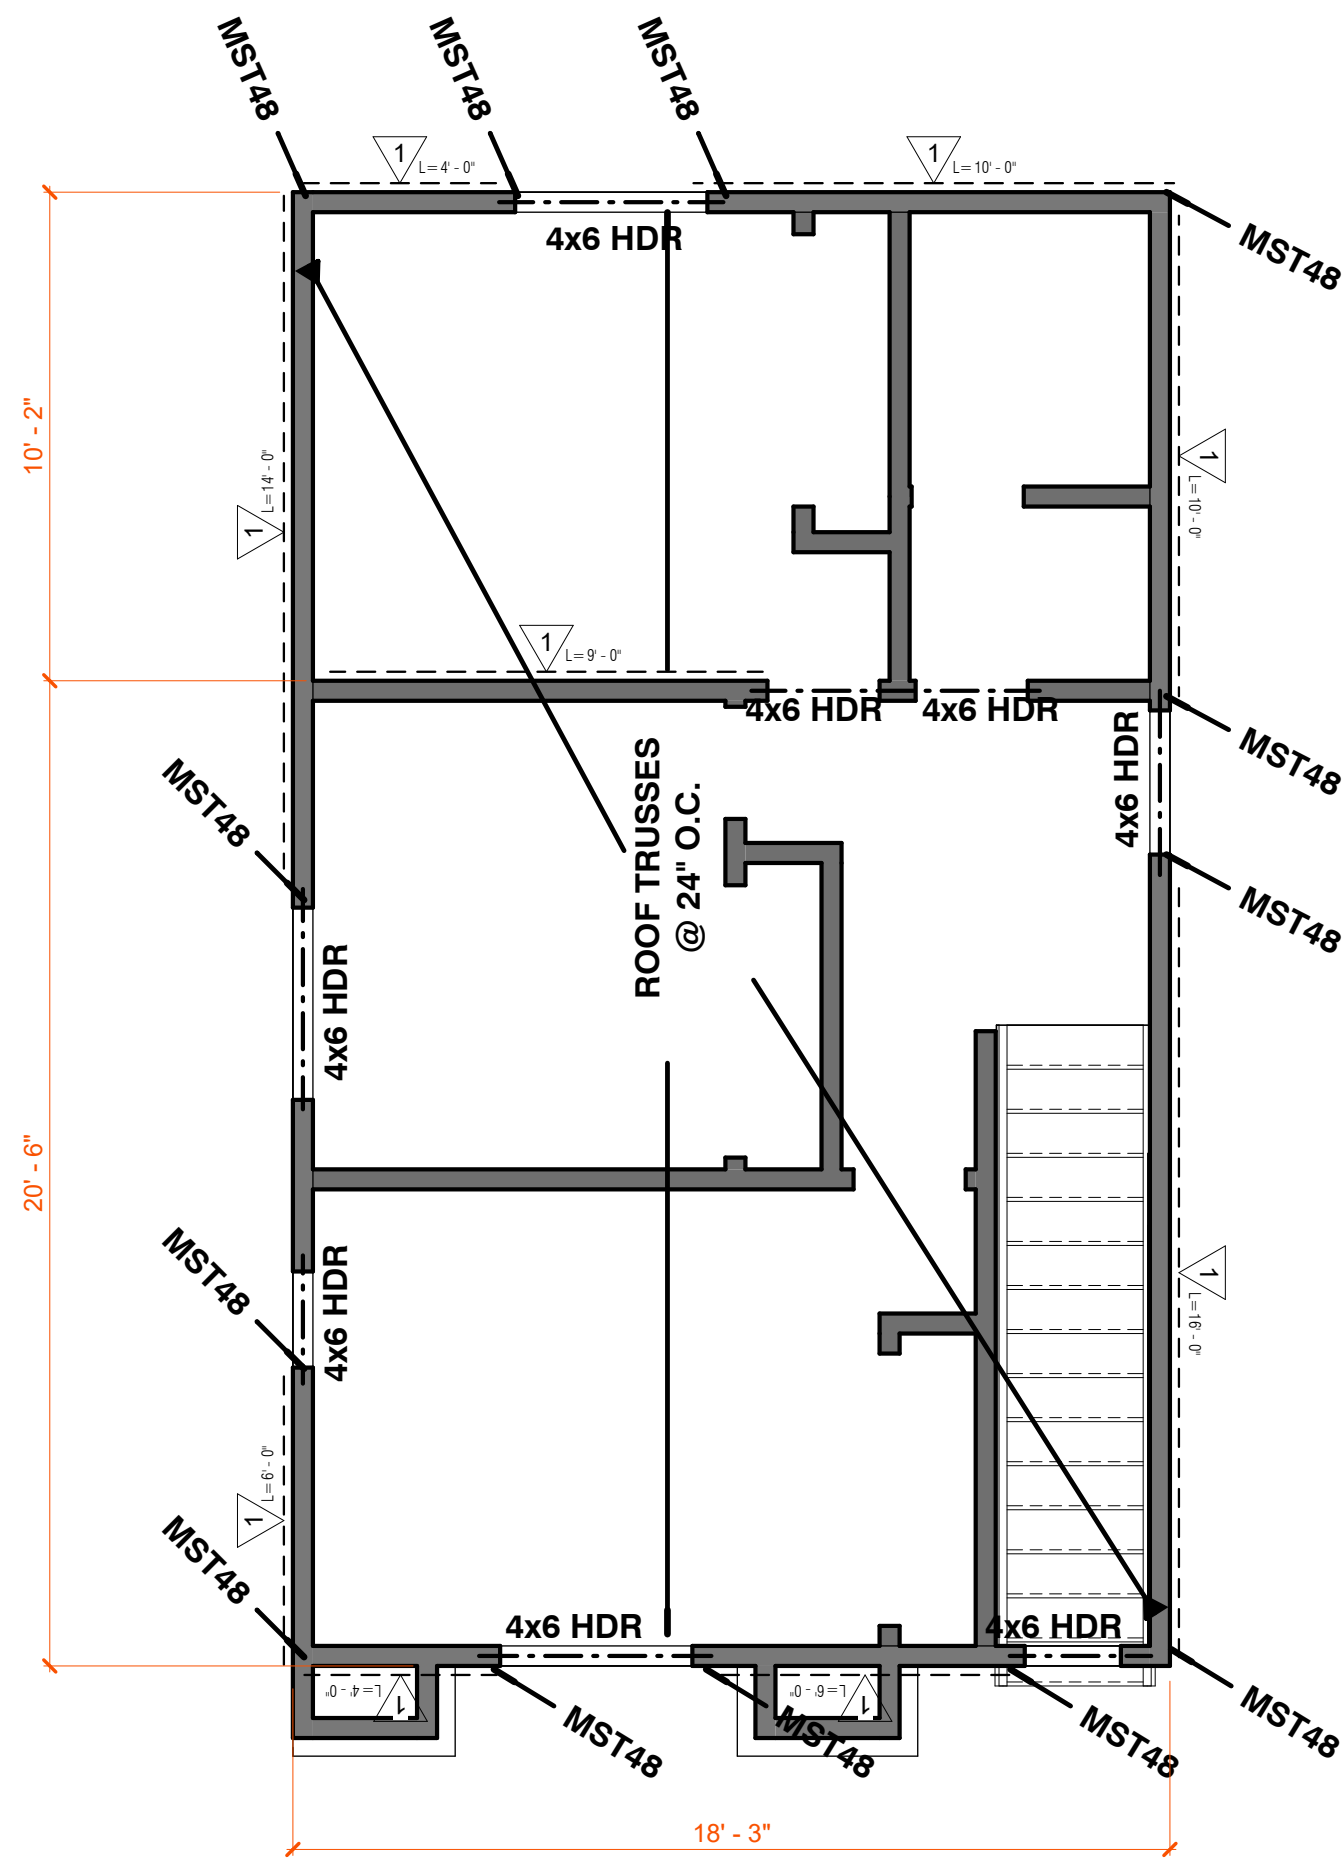


2 2nd Floor Framing Plan

1/4" = 1'-0"

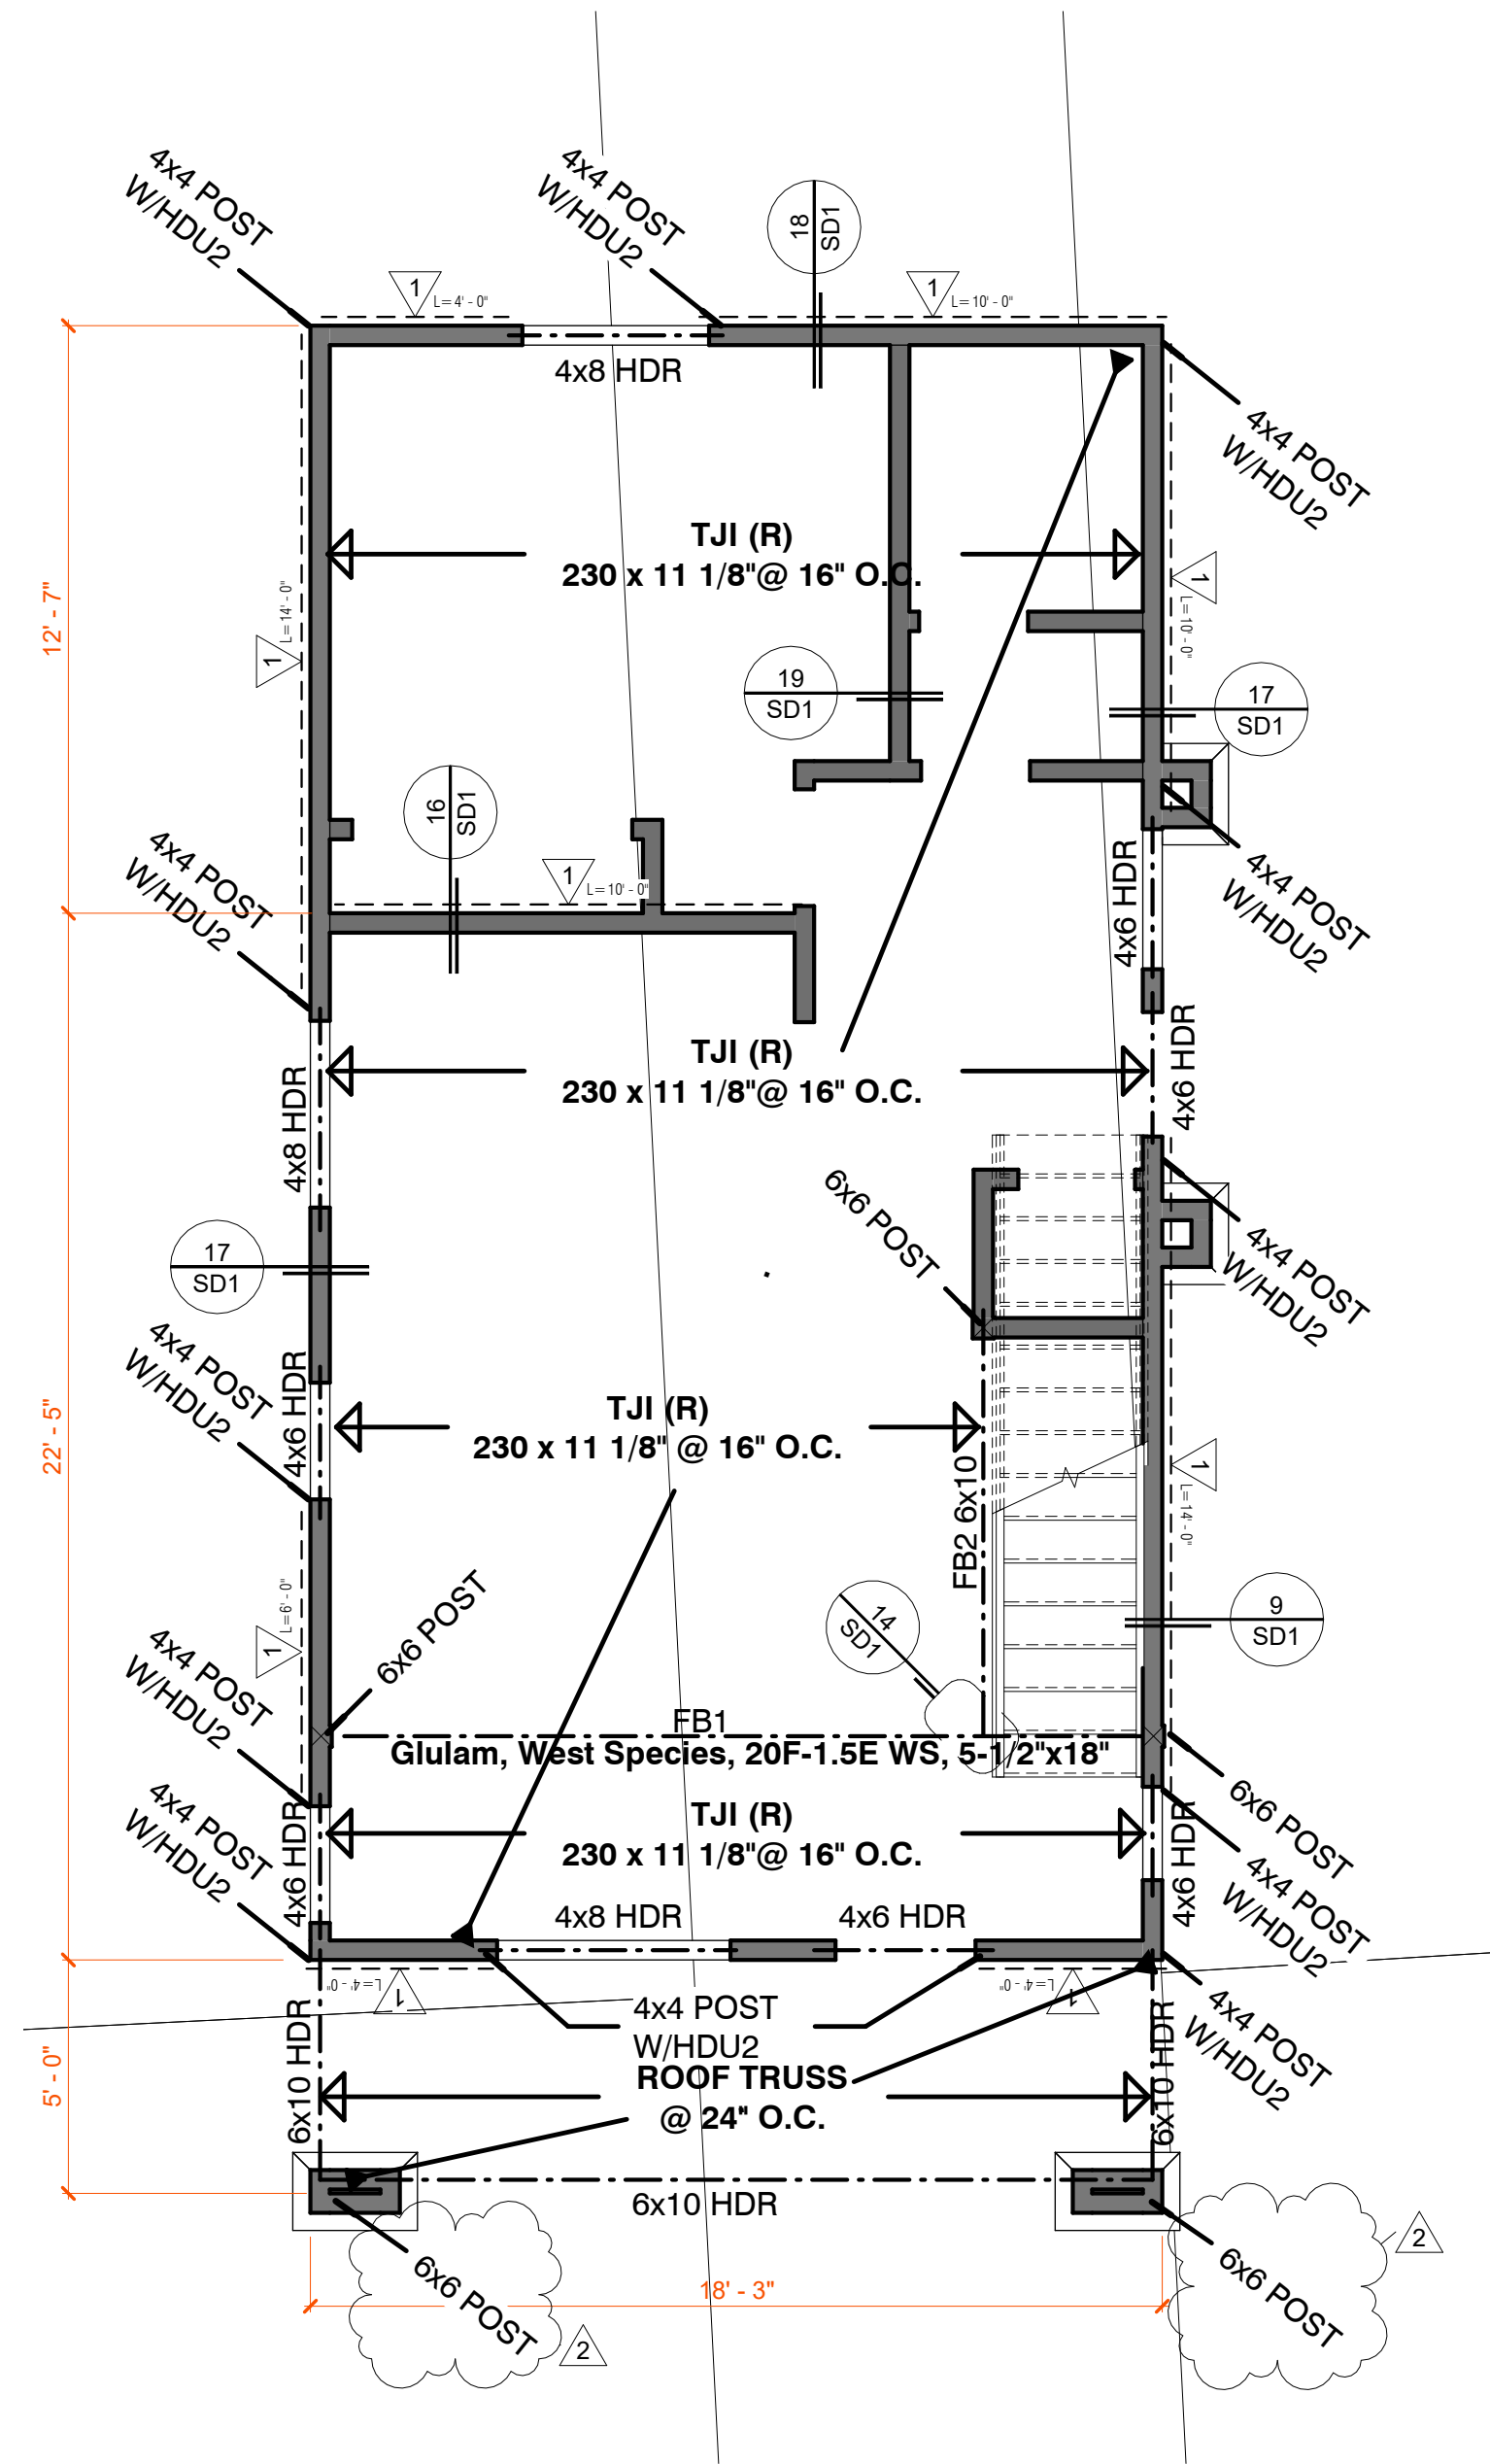

1 1st Floor Framing Plan

1/4" = 1'-0"

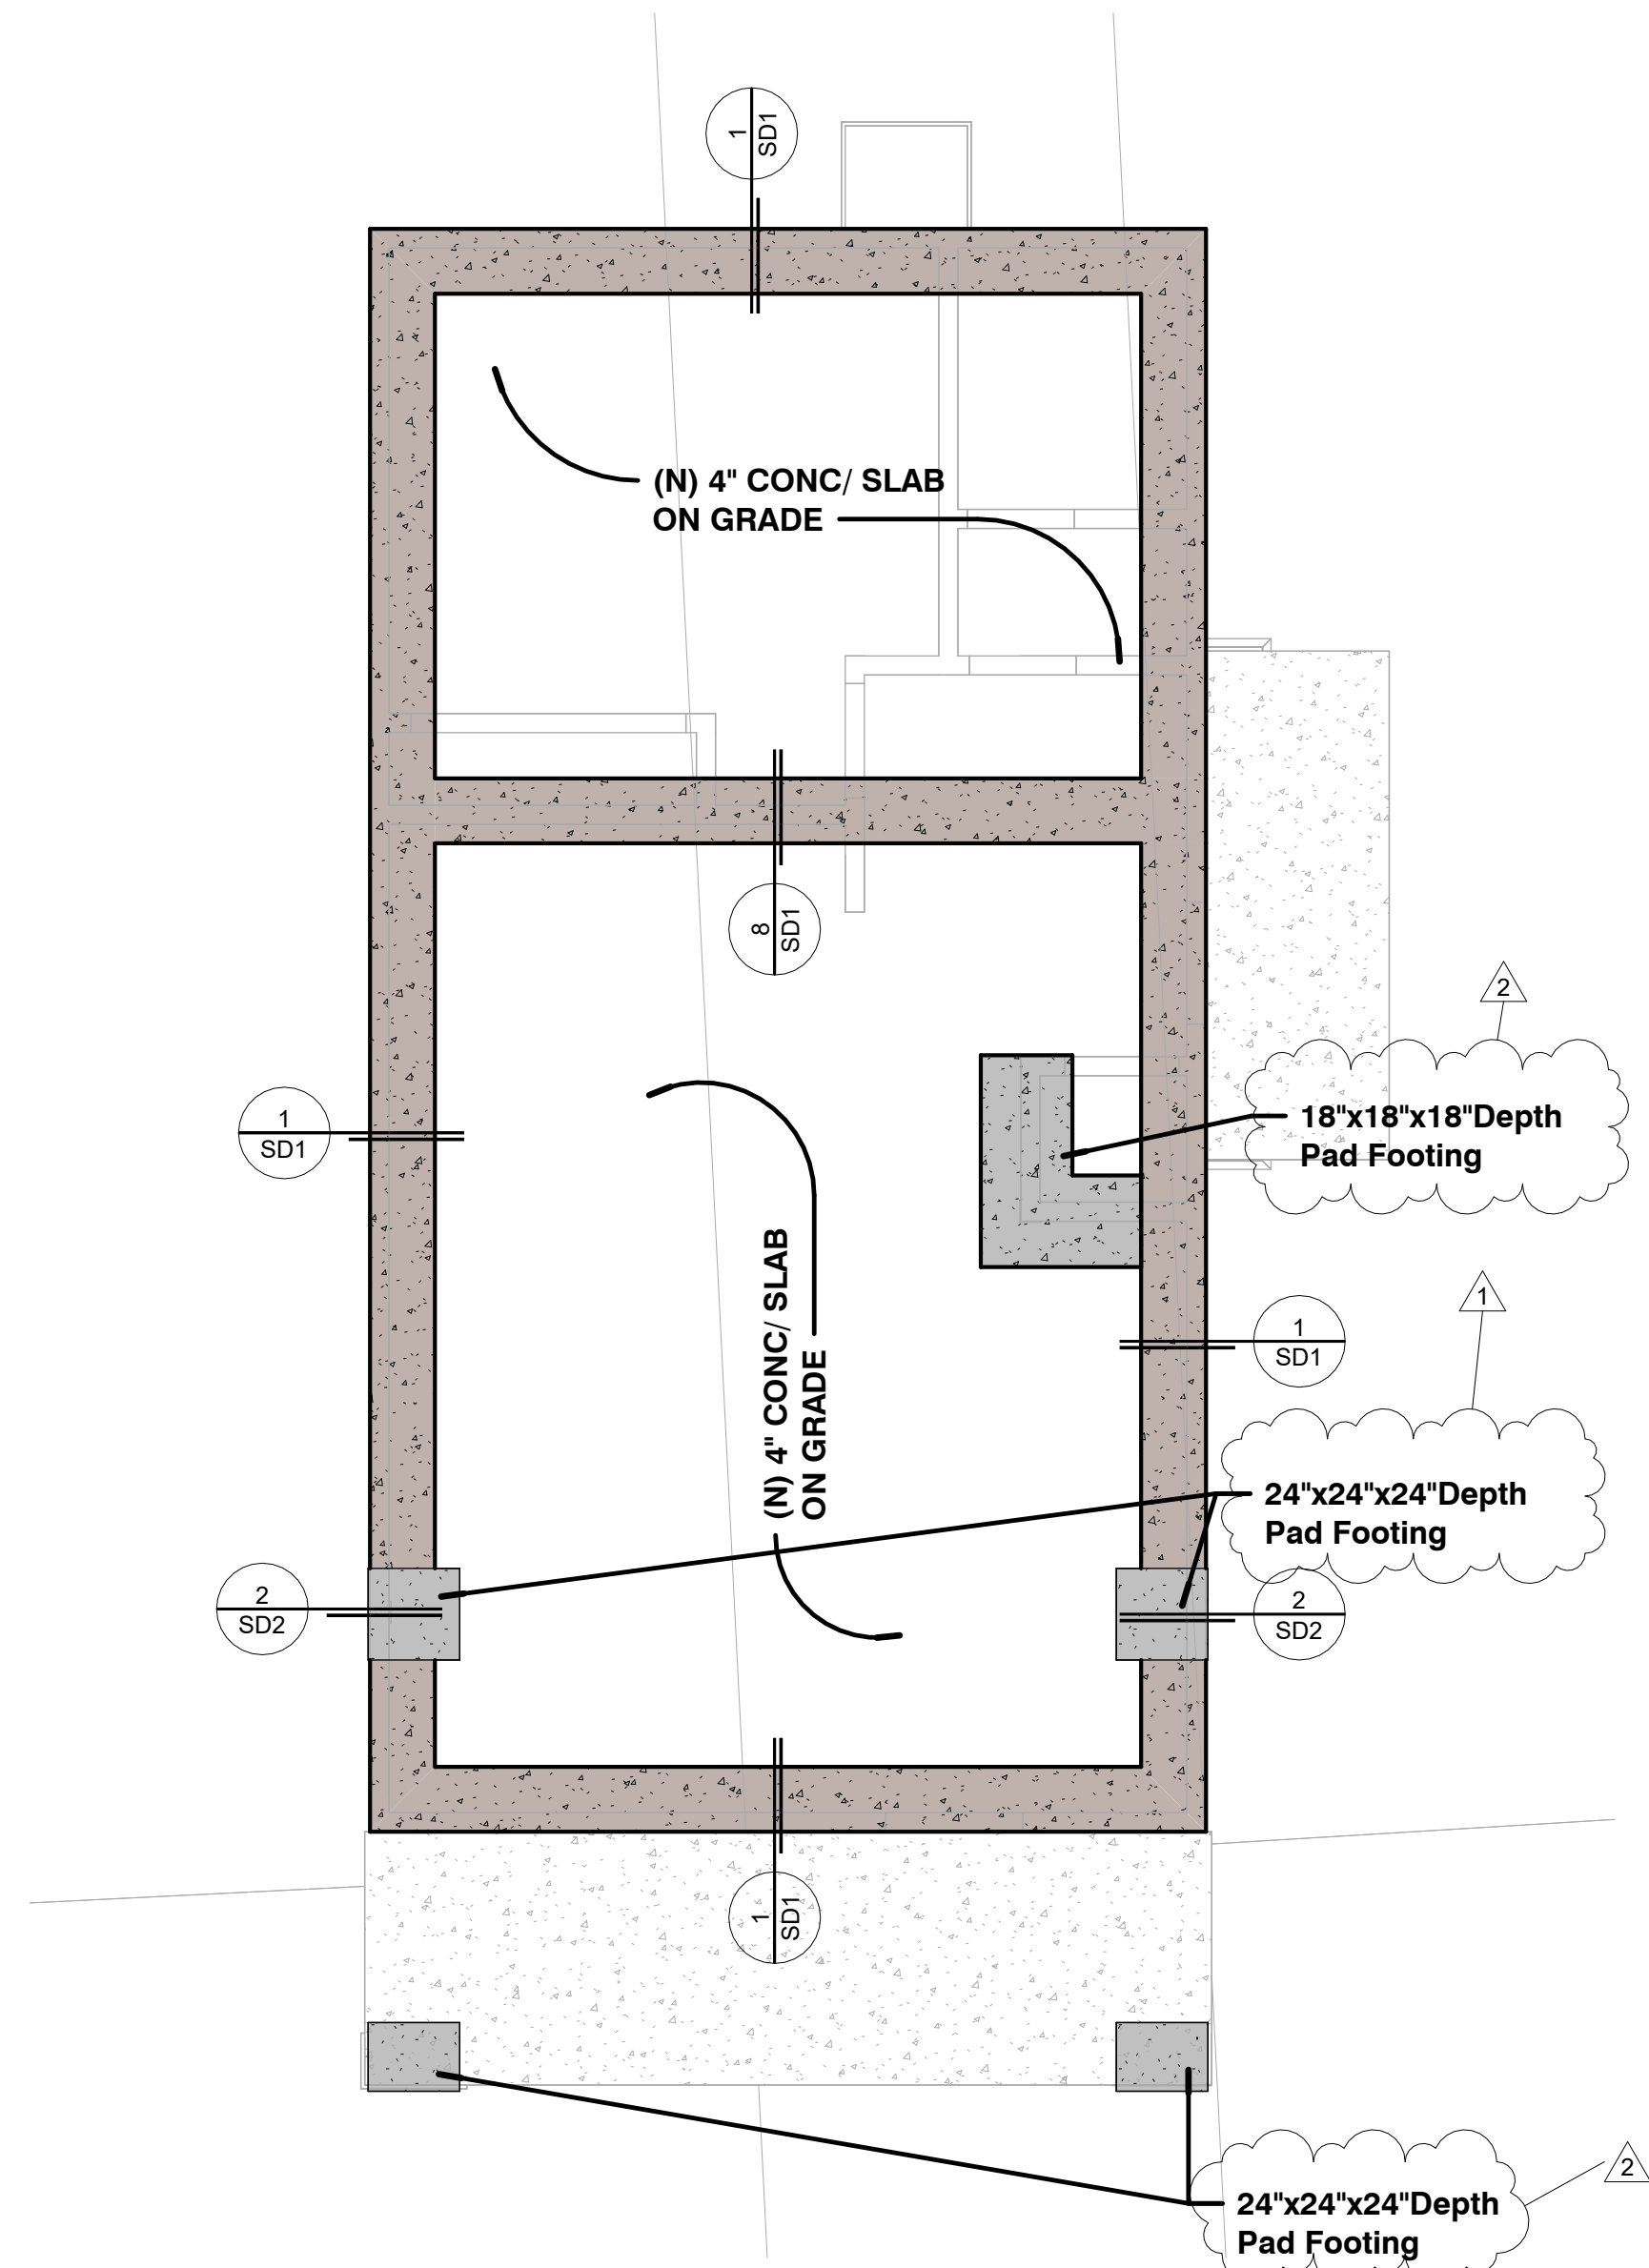

3 Foundation Floor Plan

1/4" = 1'-0"

THE APPLICANT/OWNER/ OWNER'S AGENT/ARCHITECT OR ENGINEER OF RECORD: BY USING THIS PERMITTED CONSTRUCTION DRAWINGS FOR CONSTRUCTION/INSTALLATION OF THE WORK SPECIFIED HEREIN, YOU AGREE TO COMPLY WITH THE REQUIREMENTS OF CITY OF SAN DIEGO FOR SPECIAL INSPECTIONS, STRUCTURAL OBSERVATIONS, CONSTRUCTION MATERIAL TESTING AND OFF-SITE FABRICATION OF BUILDING COMPONENTS, CONTAINED IN THE STATEMENT OF SPECIAL INSPECTIONS AND, AS REQUIRED BY THE CALIFORNIA CONSTRUCTION CODES.

NOTICE TO THE CONTRACTOR/BUILDER/INSTALLER/SUB-CONTRACTOR/OWNER-BUILDER: BY USING THIS PERMITTED CONSTRUCTION DRAWINGS FOR CONSTRUCTION/INSTALLATION OF THE WORK SPECIFIED HEREIN, YOU ACKNOWLEDGE AND ARE AWARE OF, THE REQUIREMENTS CONTAINED IN THE STATEMENT OF SPECIAL INSPECTIONS. YOU AGREE TO COMPLY WITH THE REQUIREMENTS OF CITY OF SAN DIEGO FOR SPECIAL INSPECTIONS, STRUCTURAL OBSERVATIONS, CONSTRUCTION MATERIAL TESTING AND OFF-SITE FABRICATION OF BUILDING COMPONENTS, CONTAINED IN THE STATEMENT OF SPECIAL INSPECTIONS AND, AS REQUIRED BY THE CALIFORNIA CONSTRUCTION CODES.

THE SPECIAL INSPECTIONS IDENTIFIED ON PLANS ARE, IN ADDITION TO , AND NOT A SUBSTITUTE FOR, THOSE INSPECTIONS REQUIRED TO BE PERFORMED BY A CITY'S BUILDING INSPECTOR.

THE SPECIAL INSPECTOR MUST BE REGISTERED BY THE CITY OF SAN DIEGO , DEVELOPMENT SERVICES, IN THE CATEGORY OF WORK REQUIRED TO HAVE SPECIAL INSPECTION.

A CERTIFICATE OF SATISFACTORY COMPLETION OF WORK REQUIRING SPECIAL INSPECTION MUST BE COMPLETED AND SUBMITTED TO THE INSPECTION SERVICES DIVISION".

1. ALL OTHER SPECIFICATION FOR STANDARD HOLD DOWN TO COMPLY WITH SIMPSON REQUIREMENTS
2. ALL HOLD DOWN MUST BE TIED INTO PLACE PRIOR TO FOUNDATION INSPECTION
3. DEPTH SPECIFIED ON SCHEDULE
4. ALL ANCHOR BOLTS SHALL HAVE A 3" 3" .229" MIN. WASHER ON TOP OF SILL PLATES

SHEAR WALL SCHEDULE										
NO.	SHEATING	EDGE NAILING	FEILD NAILING	FRAMING MEMBER	CONNECTION AT TOP PLATE	FOUNDATION ANCHORAGE	SILL PLATE NAILING TO WOOD FLOOR	CAPACITY (plf)	POST-HOL DOWN	SIMPSON HOLDOWN
1	23/32 OSB	8d @ 6"	8d @ 12"	2x	A-35 @ 16"	5/8" @ 48"	16d @ 5"	260	4x4 OR (2) 2X4	HDU5