


Steven Truong Res-New ADU
6633 Electric Ave
La Jolla, CA 92037



Revision Dates	
1	08.15.24
2	01.01.25
SHEET TITLE	
Structure Details	
Drawing Date	
	08.27.26
Check By	
-	
Drawn By	
Author	
Scale	
1/2" = 1'-0"	
Job Number	
022225	
Sheet Number	

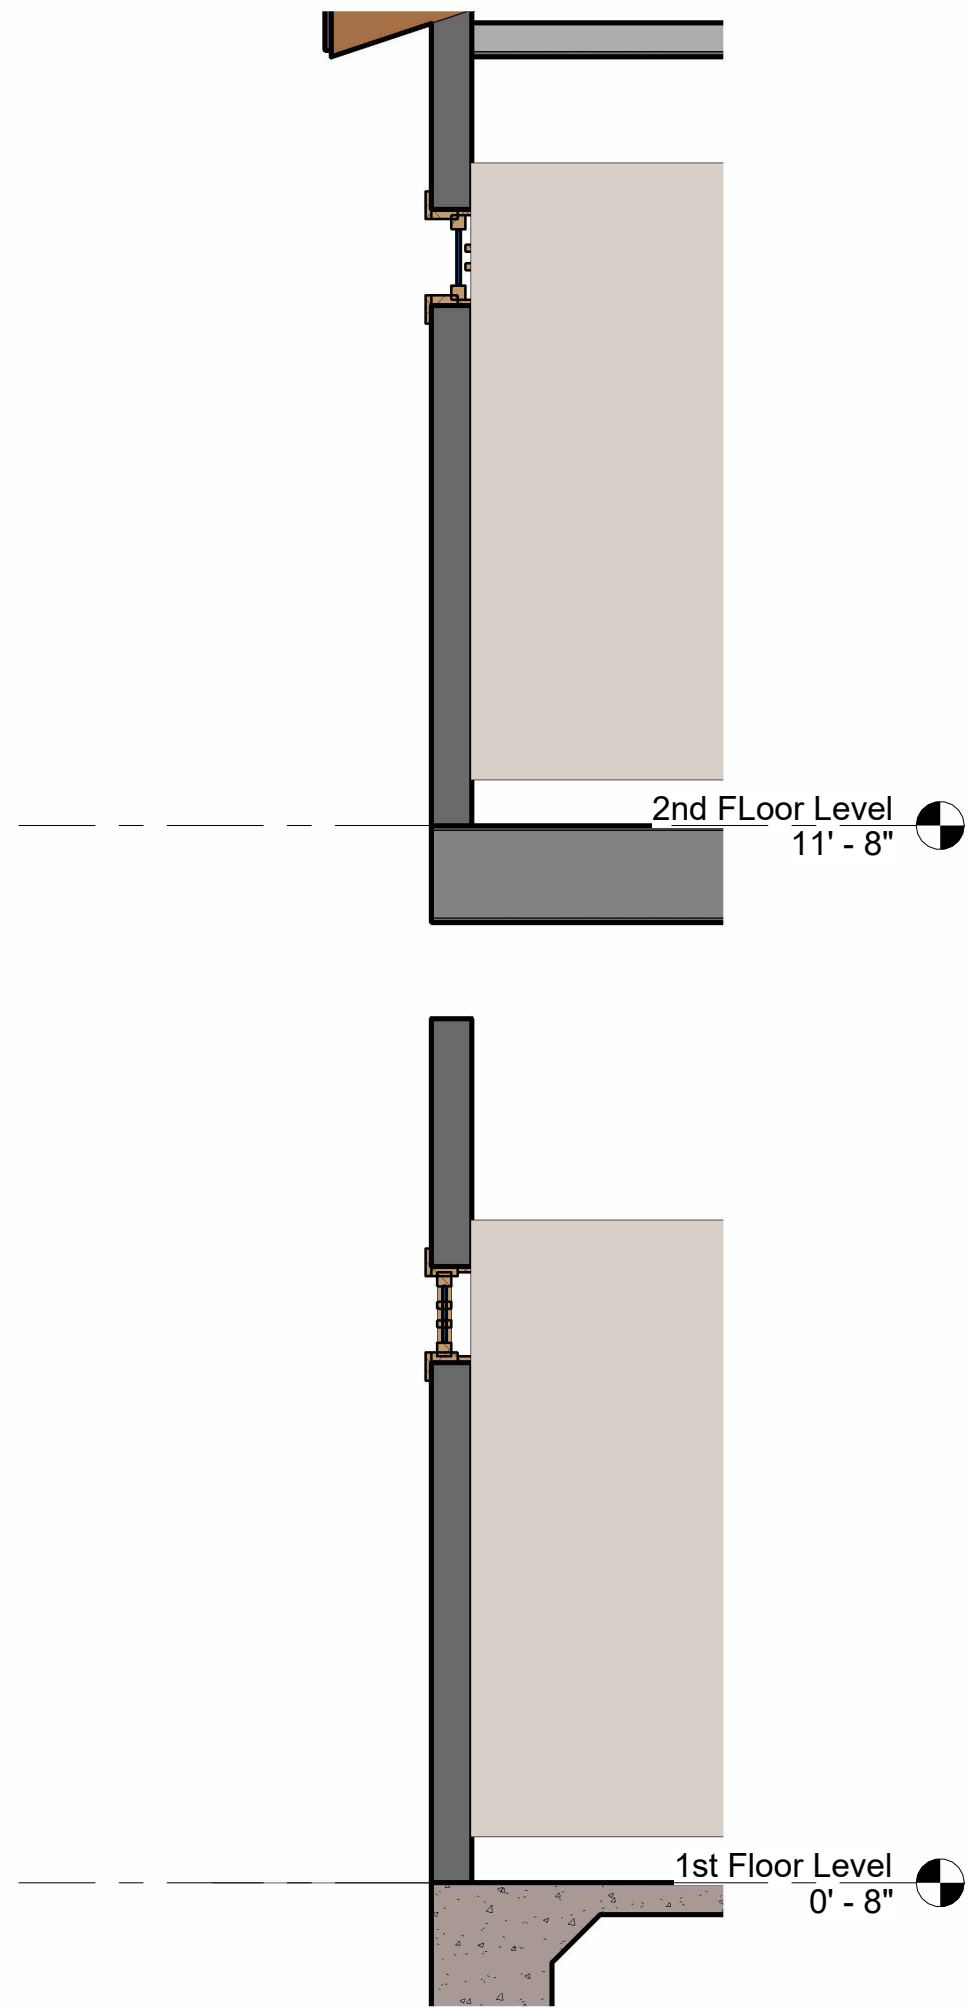

14 *Section 3 - Callout 1*
1/2" = 1'-0"



8 *Foundation Floor Plan - Callout 4*
1/2" = 1'-0"




10 *Foundation Floor Plan - Callout 5*
1/2" = 1'-0"




11 *Foundation Floor Plan - Callout 6*
1/2" = 1'-0"

3&4 *Foundation Floor Plan - Callout 3*
1/2" = 1'-0"

7 *Foundation Floor Plan - Callout 1*

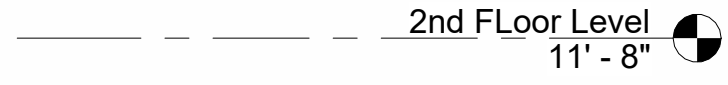

9 *Callout of Section AA*
1/2" = 1'-0"

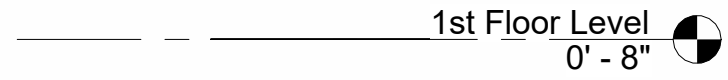

16 *Foundation Floor Plan - Callout 2*
1/2" = 1'-0"

1&2 *Detail 13*
1/2" = 1'-0"